

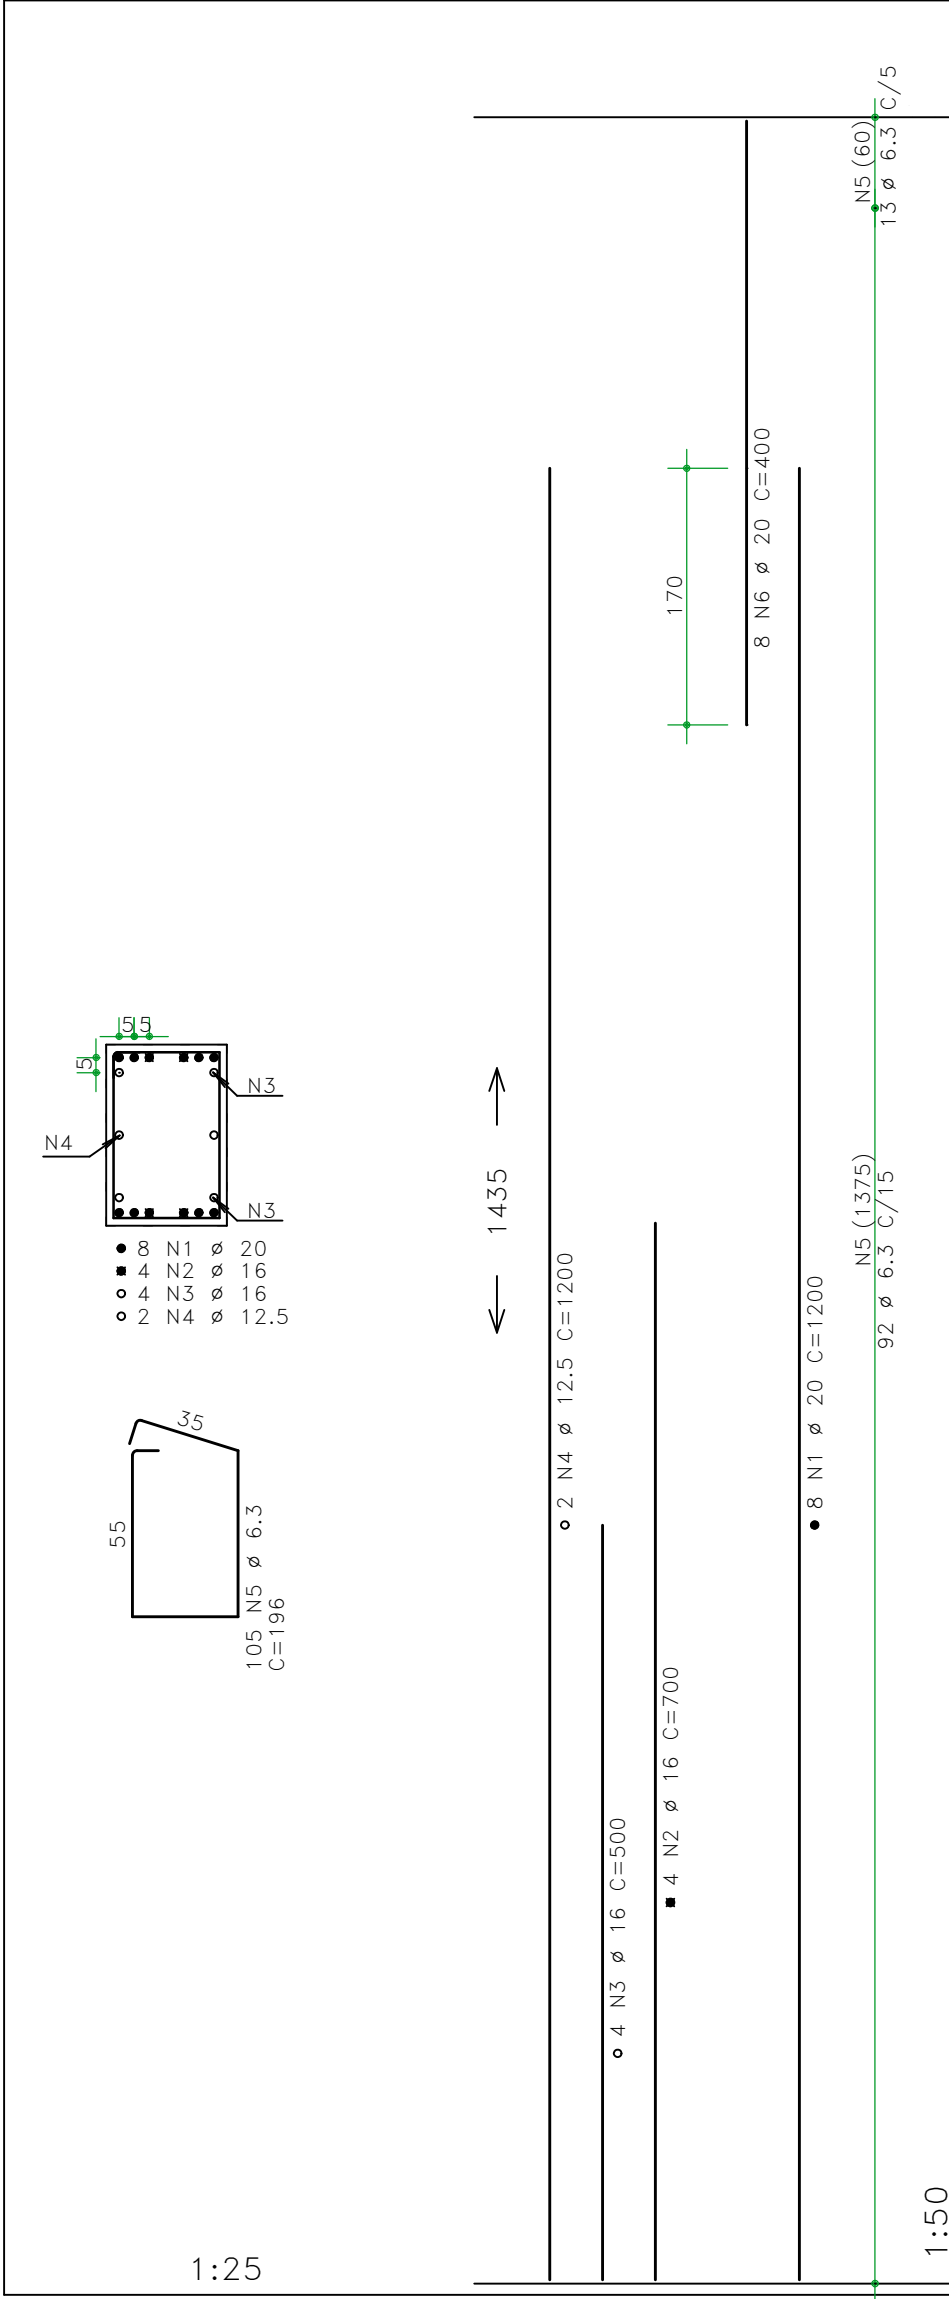
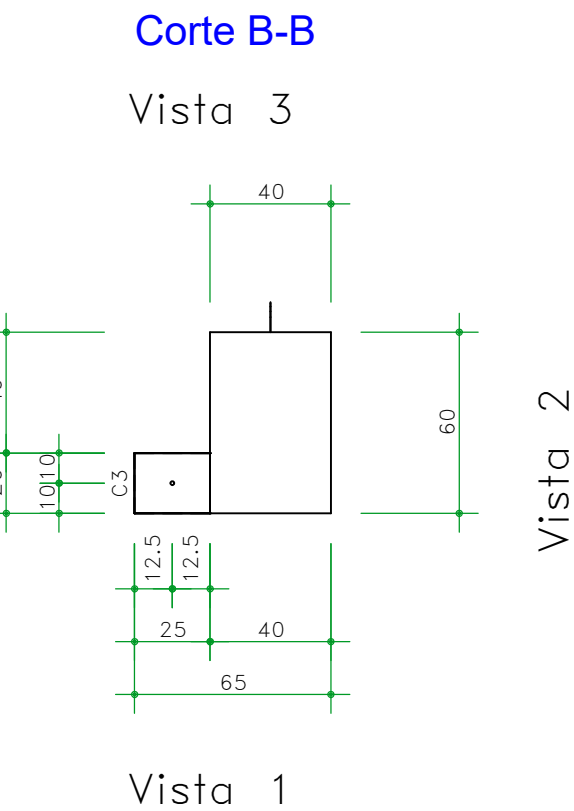





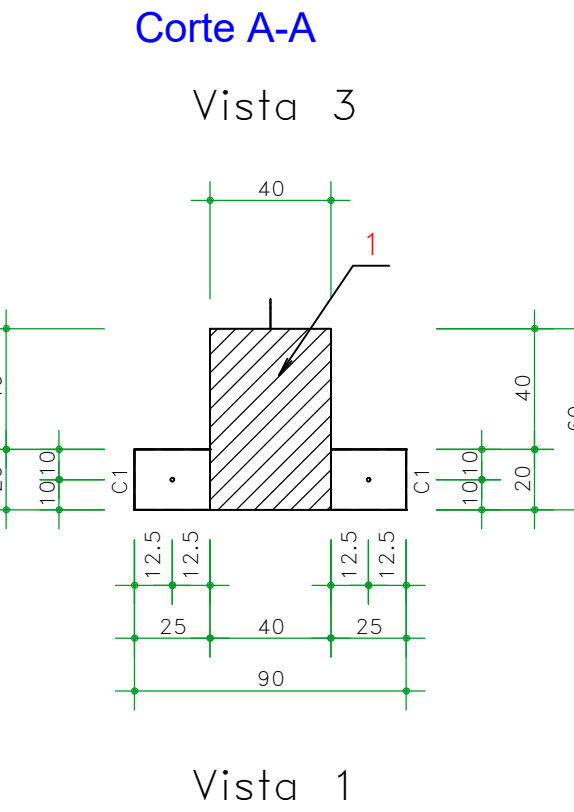


AÇO	POS	BIT	QUANT	COMPRIMENTO	
				UNIT	TOTAL
		mm		cm	cm
50A	1	20	8	1200	9600
50A	2	16	4	700	2800
50A	3	16	4	500	2000
50A	4	12.5	2	1200	2400
50A	5	6.3	10.5	196	20580
50A	6	20	8	400	3200

RESUMO DE AÇO			
AÇO	BIT	COMPR	PESO
	mm	m	kgf
50A	6.3	206	50
50A	12.5	24	23
50A	16	48	76
50A	20	128	316
Peso Total	50A =		465 kgf

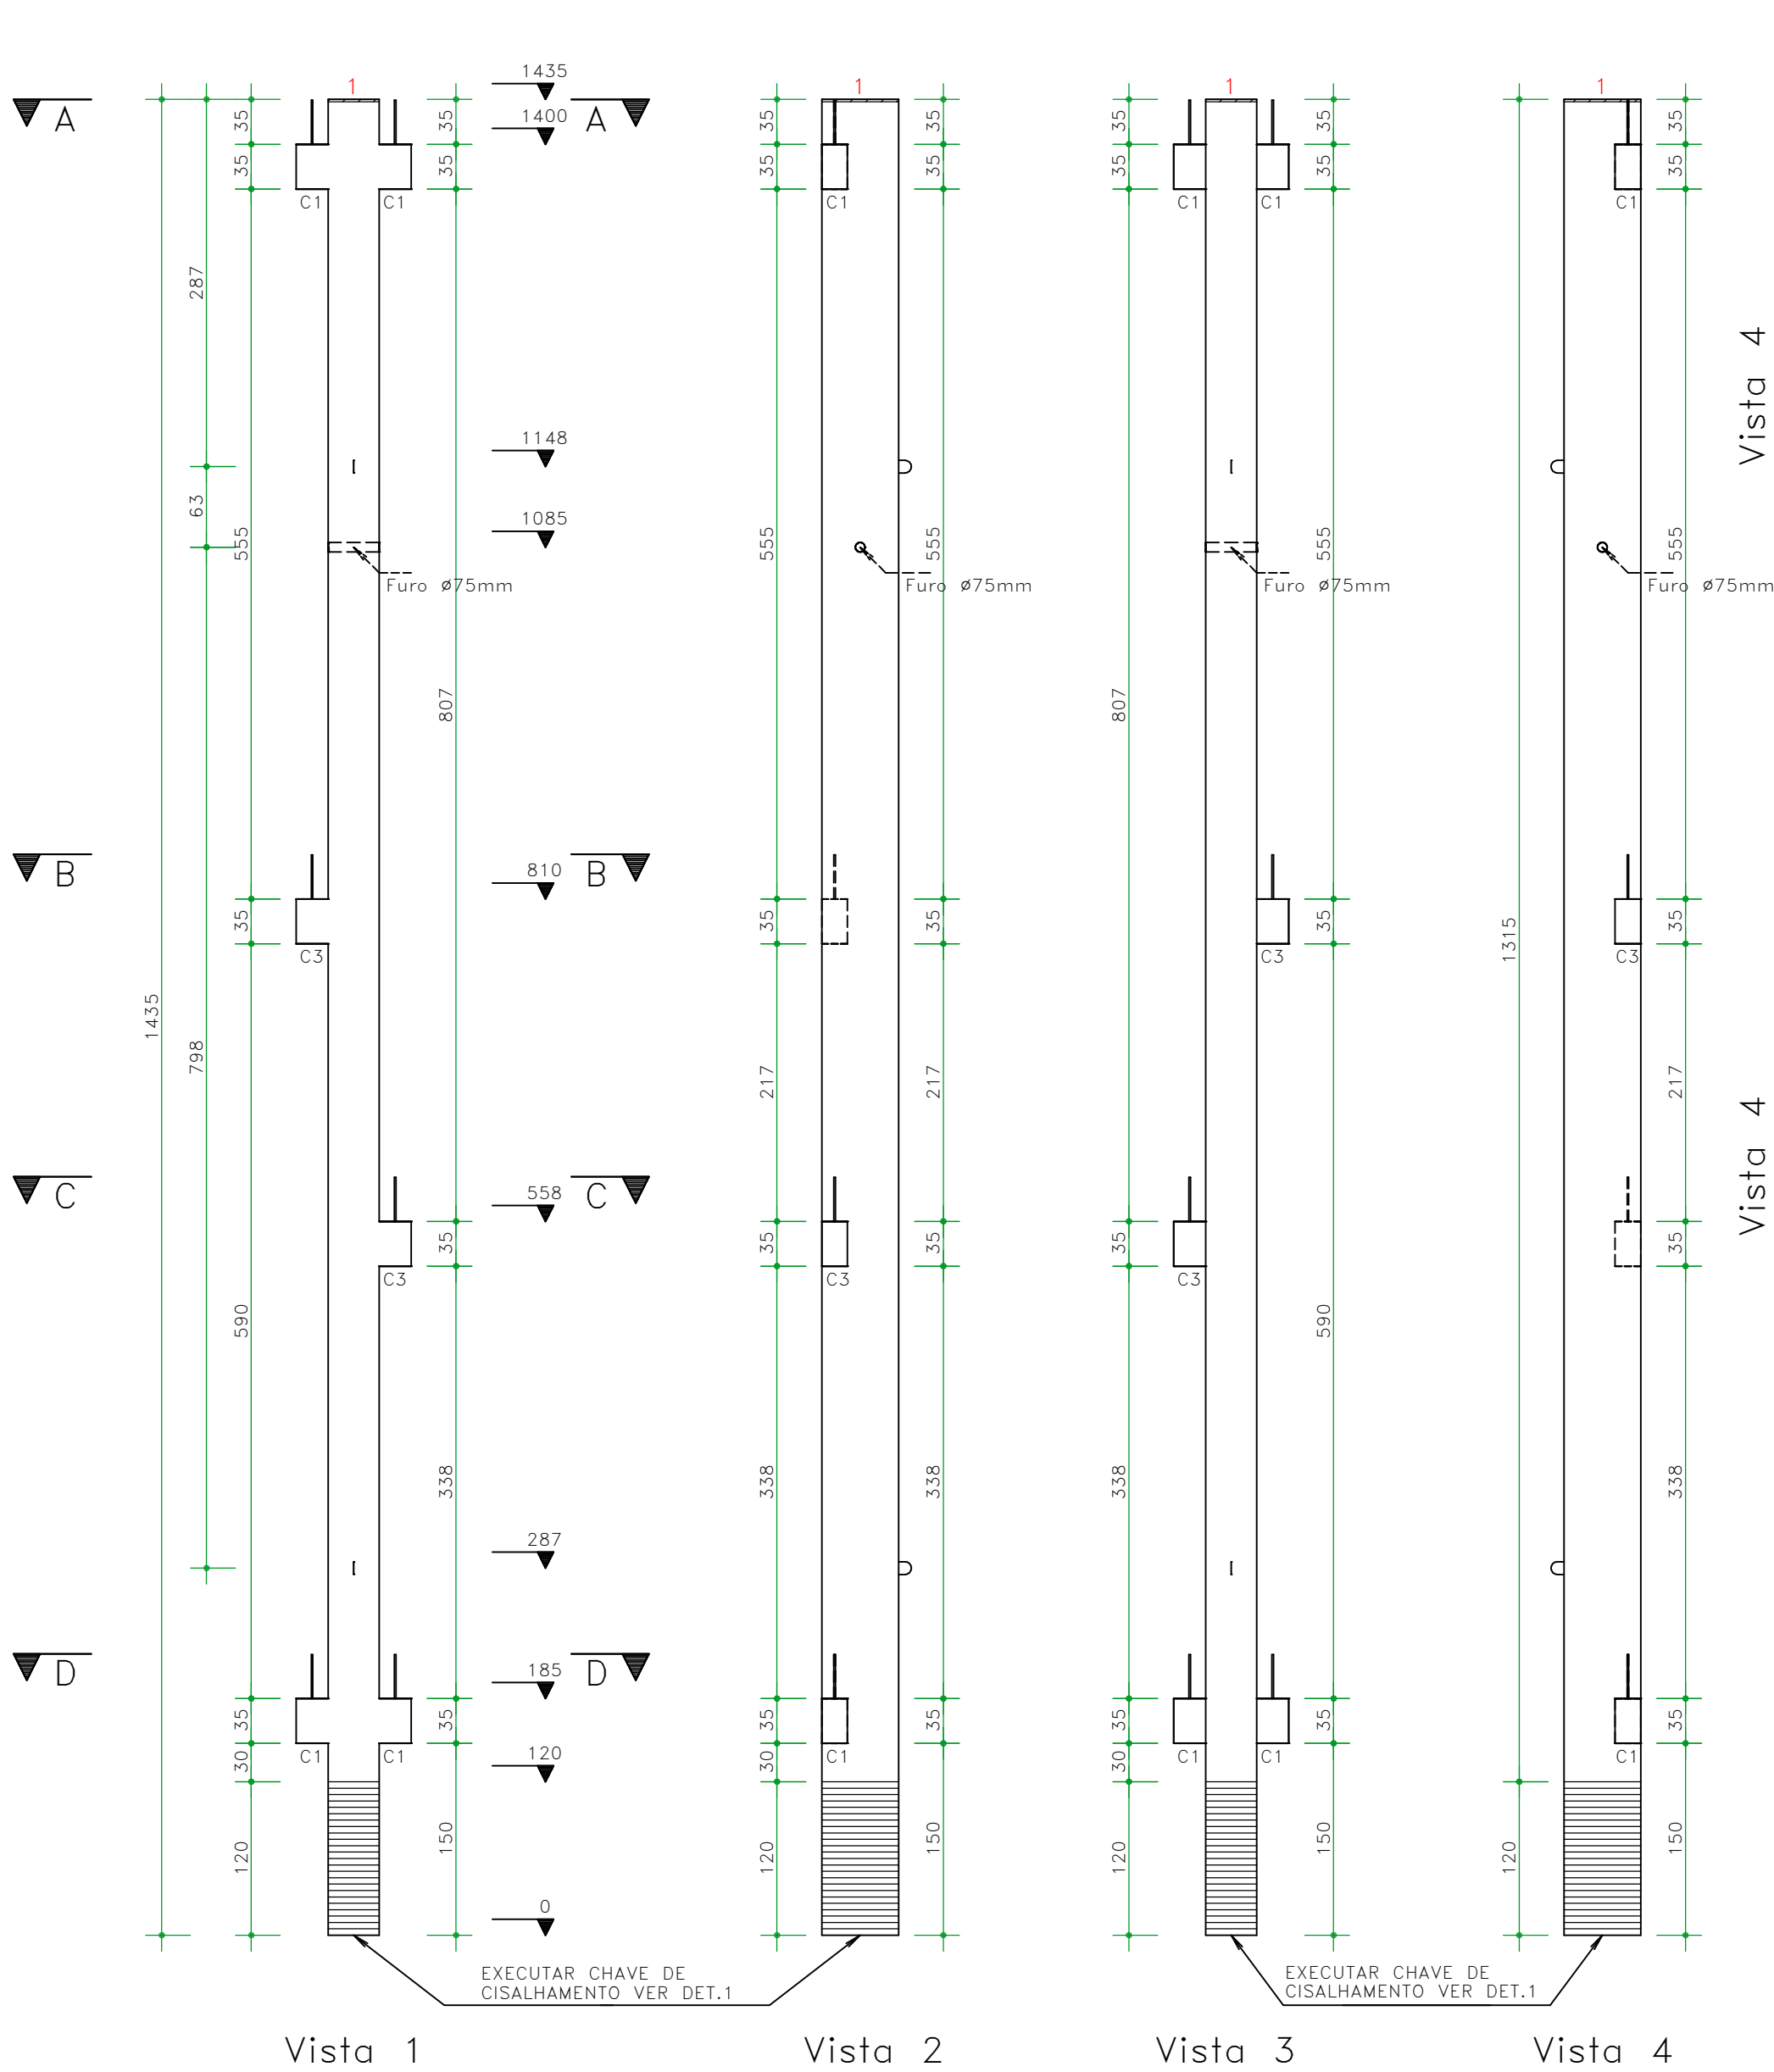

LEGENDA INSERTOS	
1	MG-INS-101

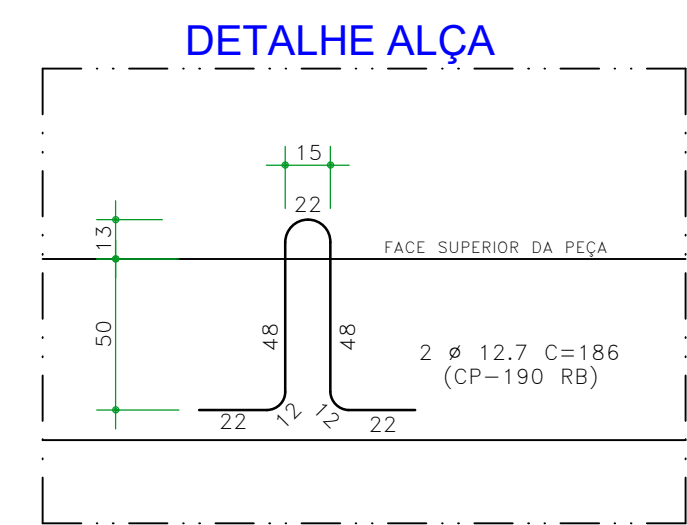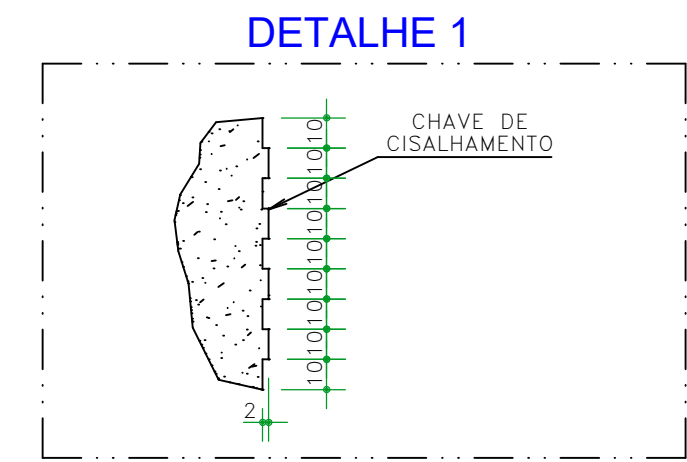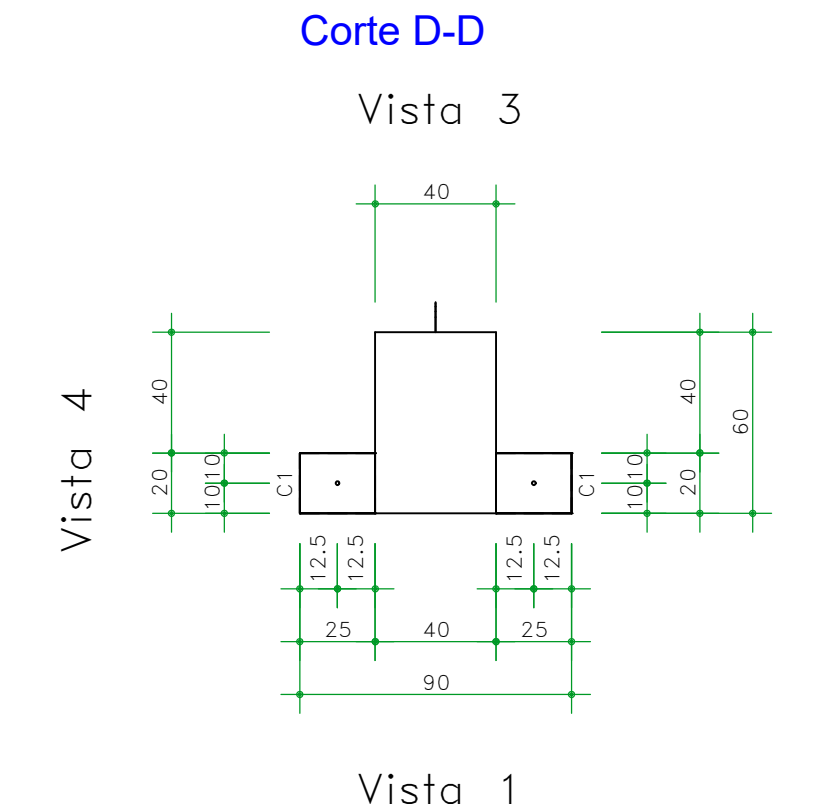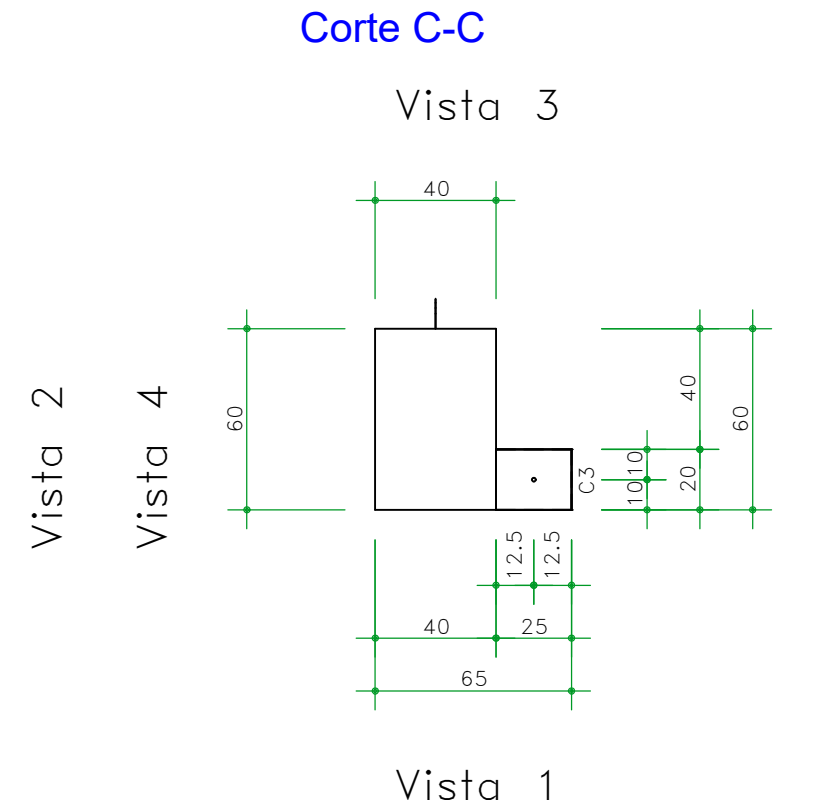

RESUMO AÇO CP 190			
AÇO	BIT	COMPR	PESO
	mm	m	kgf
CP-190 RB	12.7	3.72	3
Peso Total	CP =		3 kg

NOTAS E OBSERVAÇÕES

- MEDIDAS EM "cm"
- CARACTERÍSTICAS DO CONCRETO (CLASSE DE AGRESSIVIDADE AMBIENTAL CAA II)
CLASSE (NBR-8953): **C40** $E_c > 30$ GPa; Relação $a/c < 0.45$
NA DESFORMA E/OU DESPOTENSÃO: $f_{cj} = 15$ MPa e $E_c = 20$ GPa
- VOLUME / PESO DA PEÇA = **3.550** m³ / **8.870** Kg/m³
- TAXA DE AÇO NA PEÇA = **132** Kg/m³
- COBRIMENTO SOBRE A ARMAÇÃO = **2,5** cm



CLIENTE INBRAC	ESCALA 1:25	
	DATA 25/03/2026	
OBRA CENTRO DE EVENTOS CUIABÁ	DESENHO CM	
	REVISÃO 0	
TÍTULO PAVILHÃO 2 - P10 FORMA E ARMAÇÃO (1x)	OBRA N. 25/016	FOLHA N. F068
VERIFICAÇÃO RFB		

+55 (11) 98199-8507

@ruybentes.engest

/ruybentes.engest