

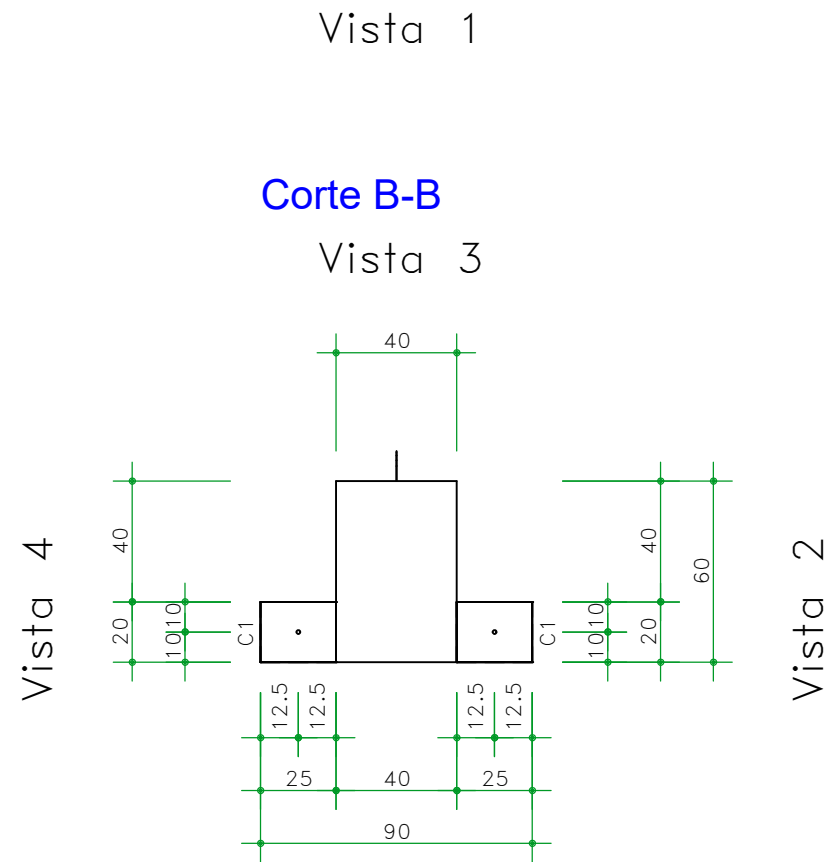
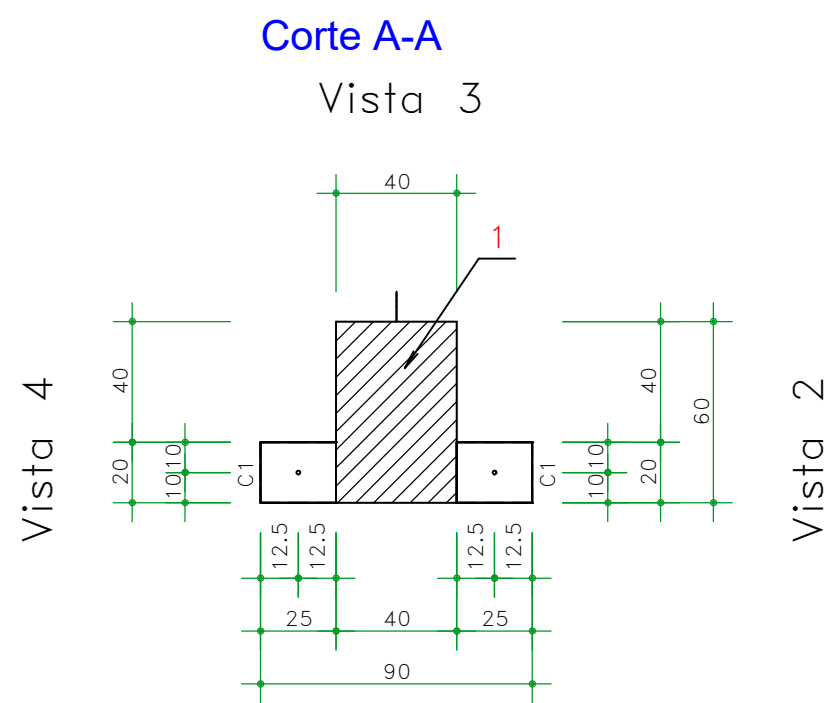
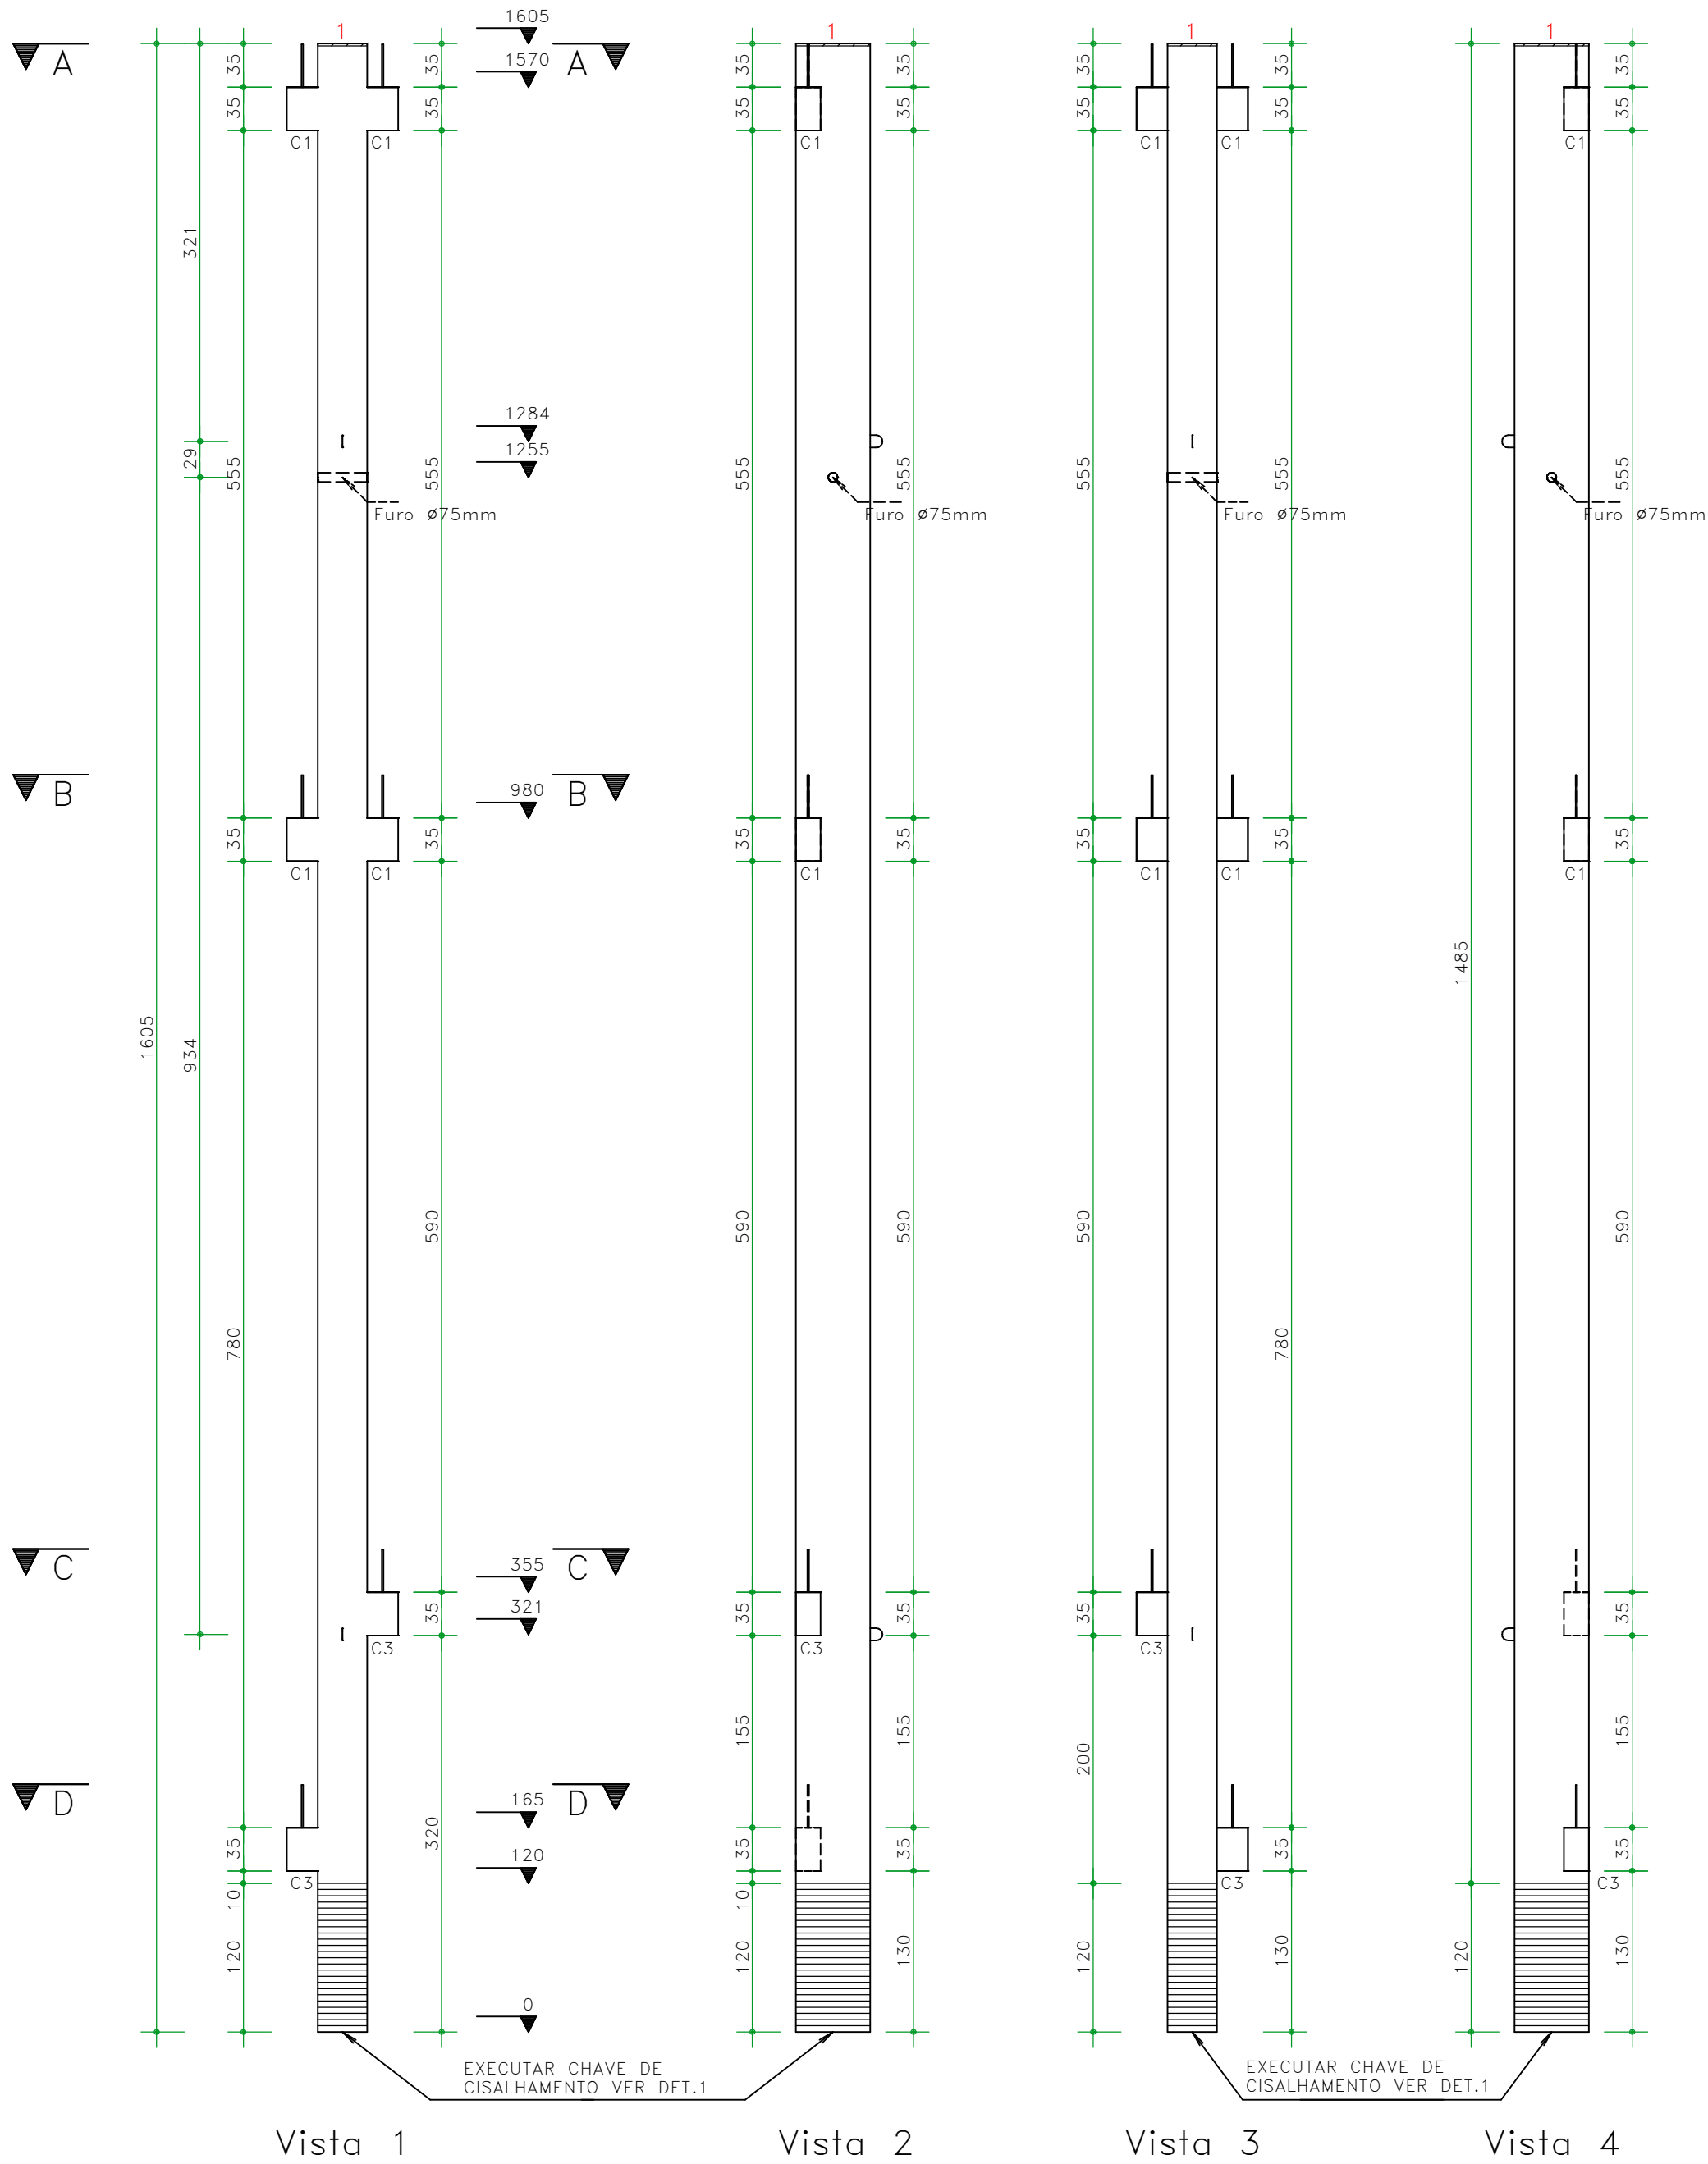
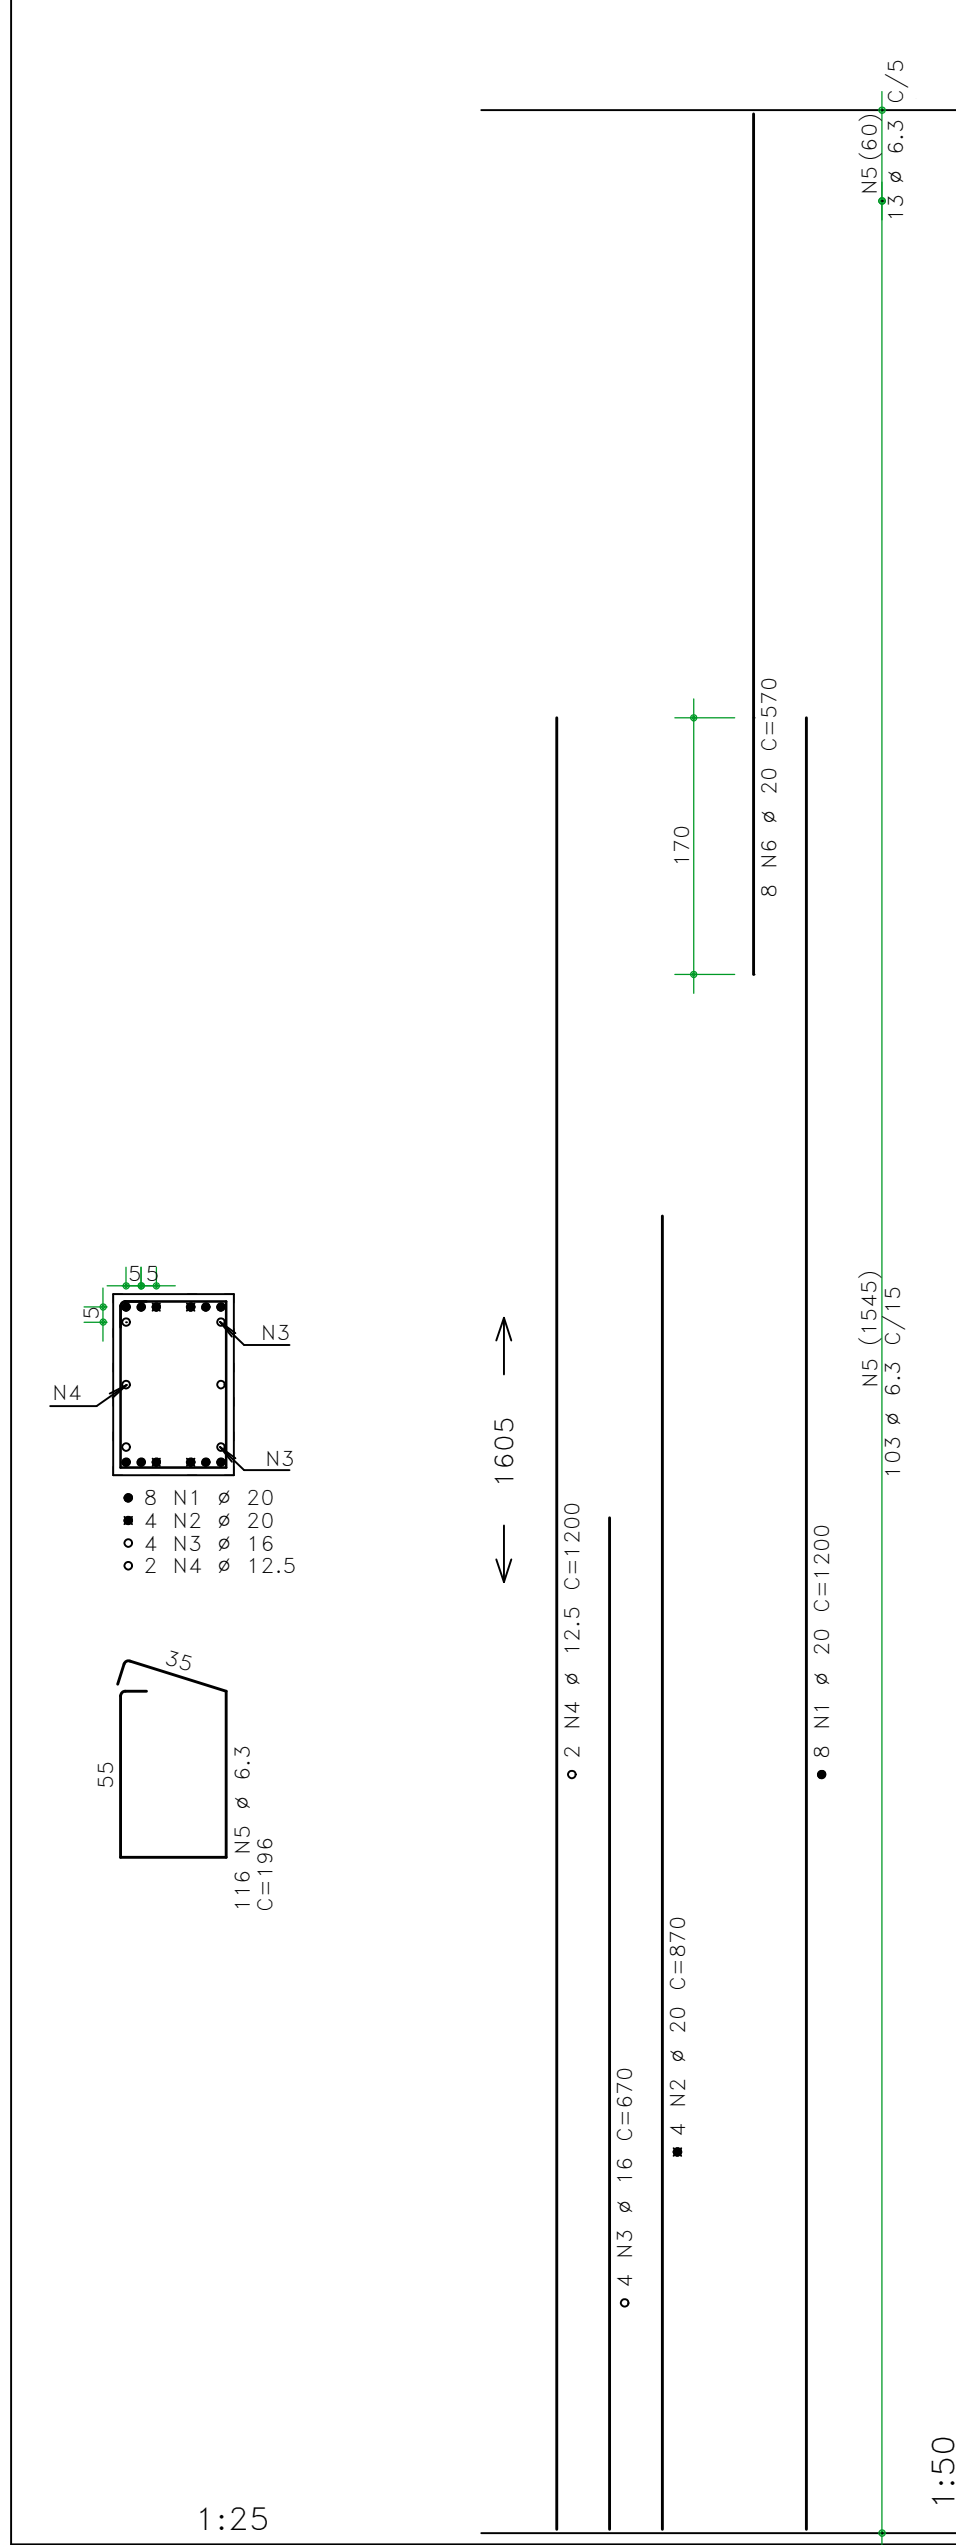
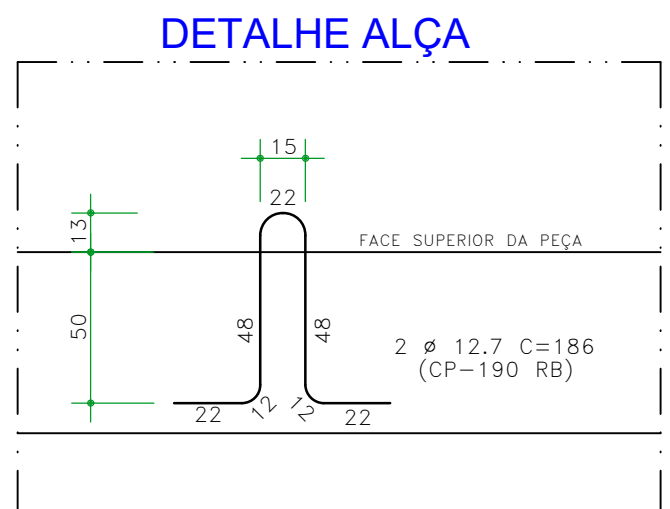
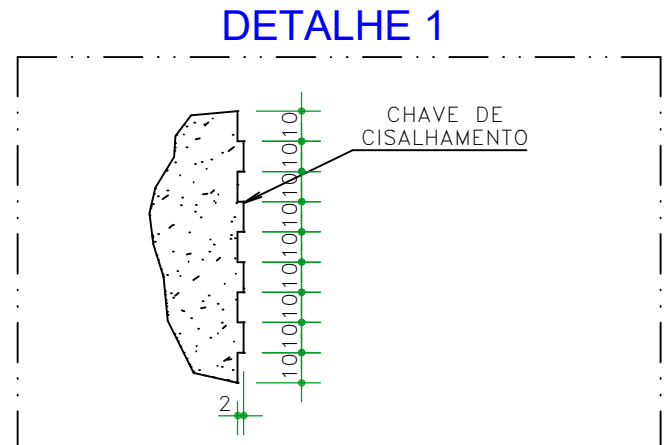


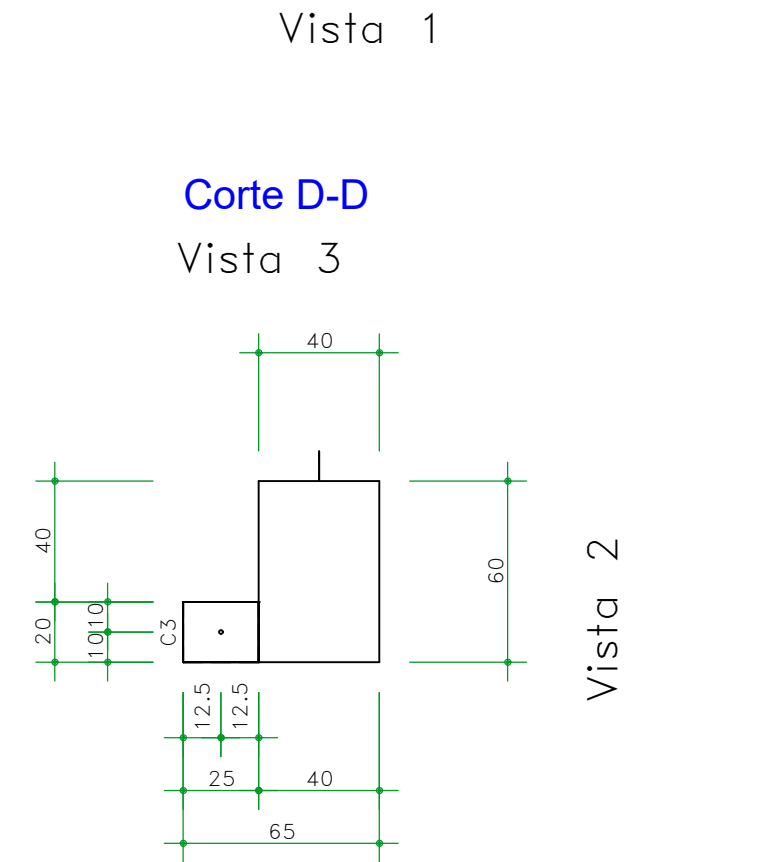

LEGENDA INSERTOS

1 MG-INS-101

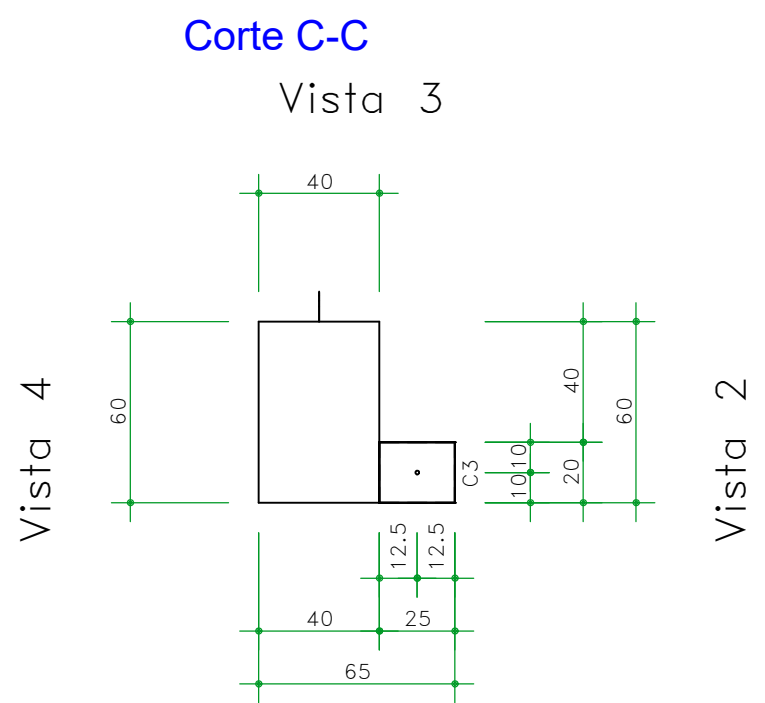

RESUMO AÇO CP 190			
AÇO	BIT	COMPR	PESO
CP-190 RB	mm	m	kgf
	12.7	3.72	3
Peso Total		CP =	3 kg

NOTAS E OBSERVAÇÕES

- MEDIDAS EM "cm"
- CARACTERÍSTICAS DO CONCRETO (CLASSE DE AGRESSIVIDADE AMBIENTAL CAA II)
CLASSE (NBR-8953): **C40** $E_c > 30$ GPa; Relação $a/c < 0.45$
NA DESFORMA E/OU DESPOTENSÃO: $f_{cj} = 15$ MPa e $E_c = 20$ GPa
- VOLUME / PESO DA PEÇA = **3,960** m³ / **9.890** Kg/m³
- TAXA DE AÇO NA PEÇA = **141** Kg/m³
- COBRIMENTO SOBRE A ARMAÇÃO = **2,5** cm



BENTES
ENGENHARIA DE PROJETOS

CLIENTE
INBRAC

OBRA
CENTRO DE EVENTOS CUIABÁ

TÍTULO
**PAVILHÃO 2 - P11
FORMA E ARMAÇÃO (1x)**

ESCALA
1:25

DATA
23/03/2026

DESENHO
CM

REVISÃO
0

VERIFICAÇÃO
RFB

OBRA N.
25/016

FOLHA N.
F069

+55 (11) 98199-8507

@ruybentes.engest

/ruybentes.engest