

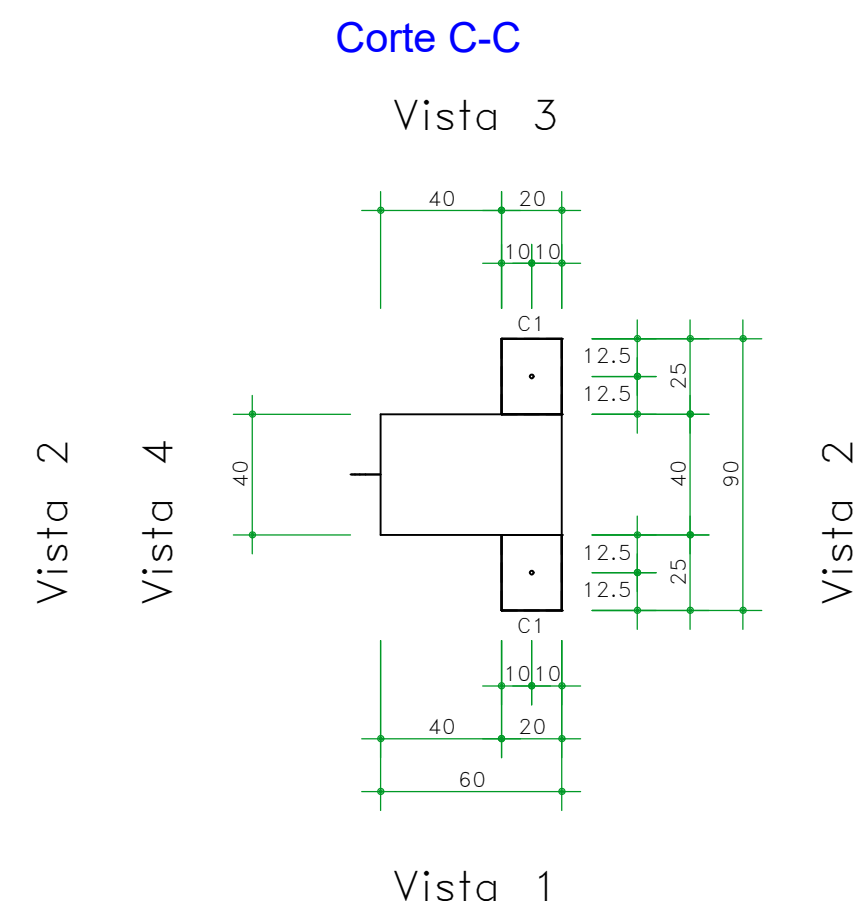
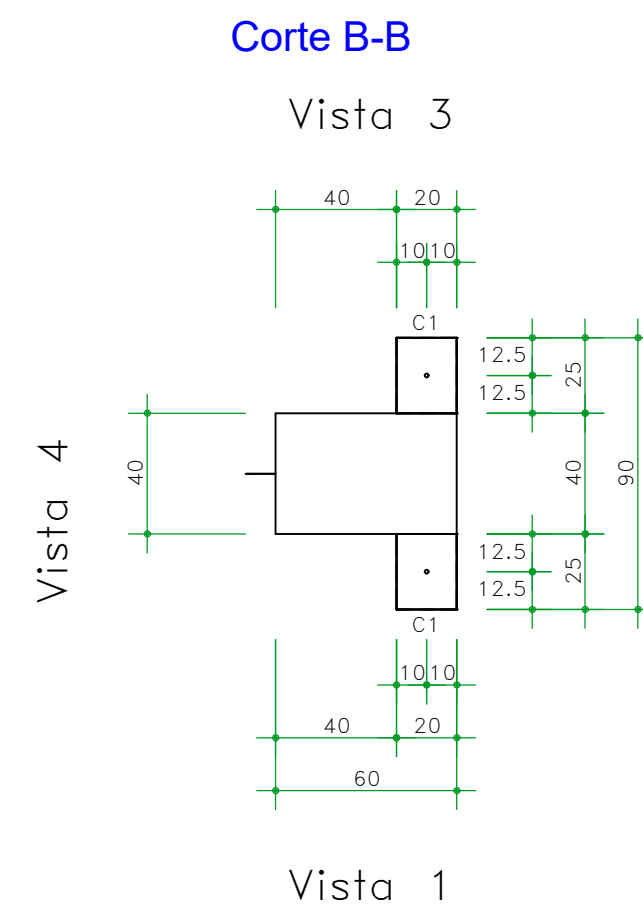
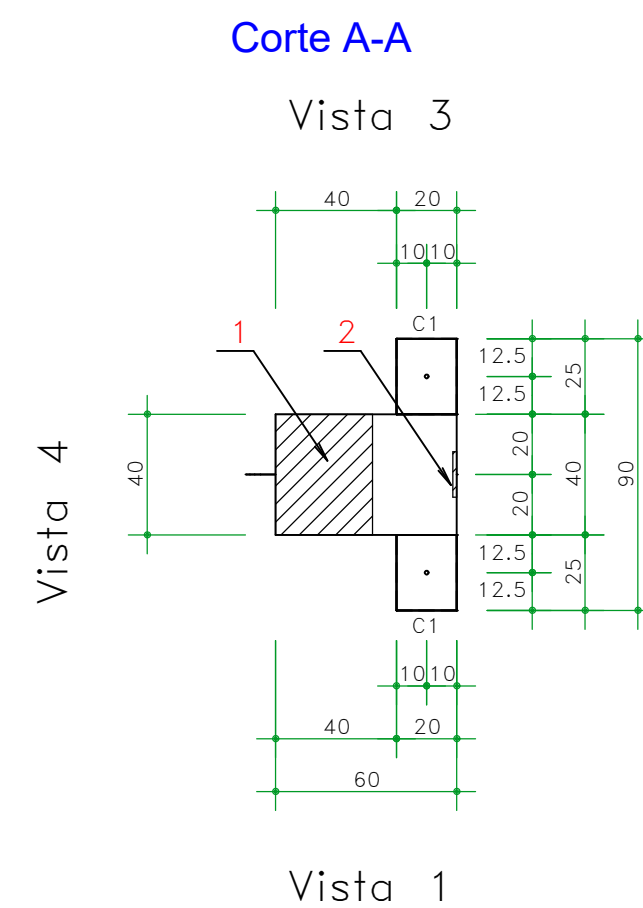
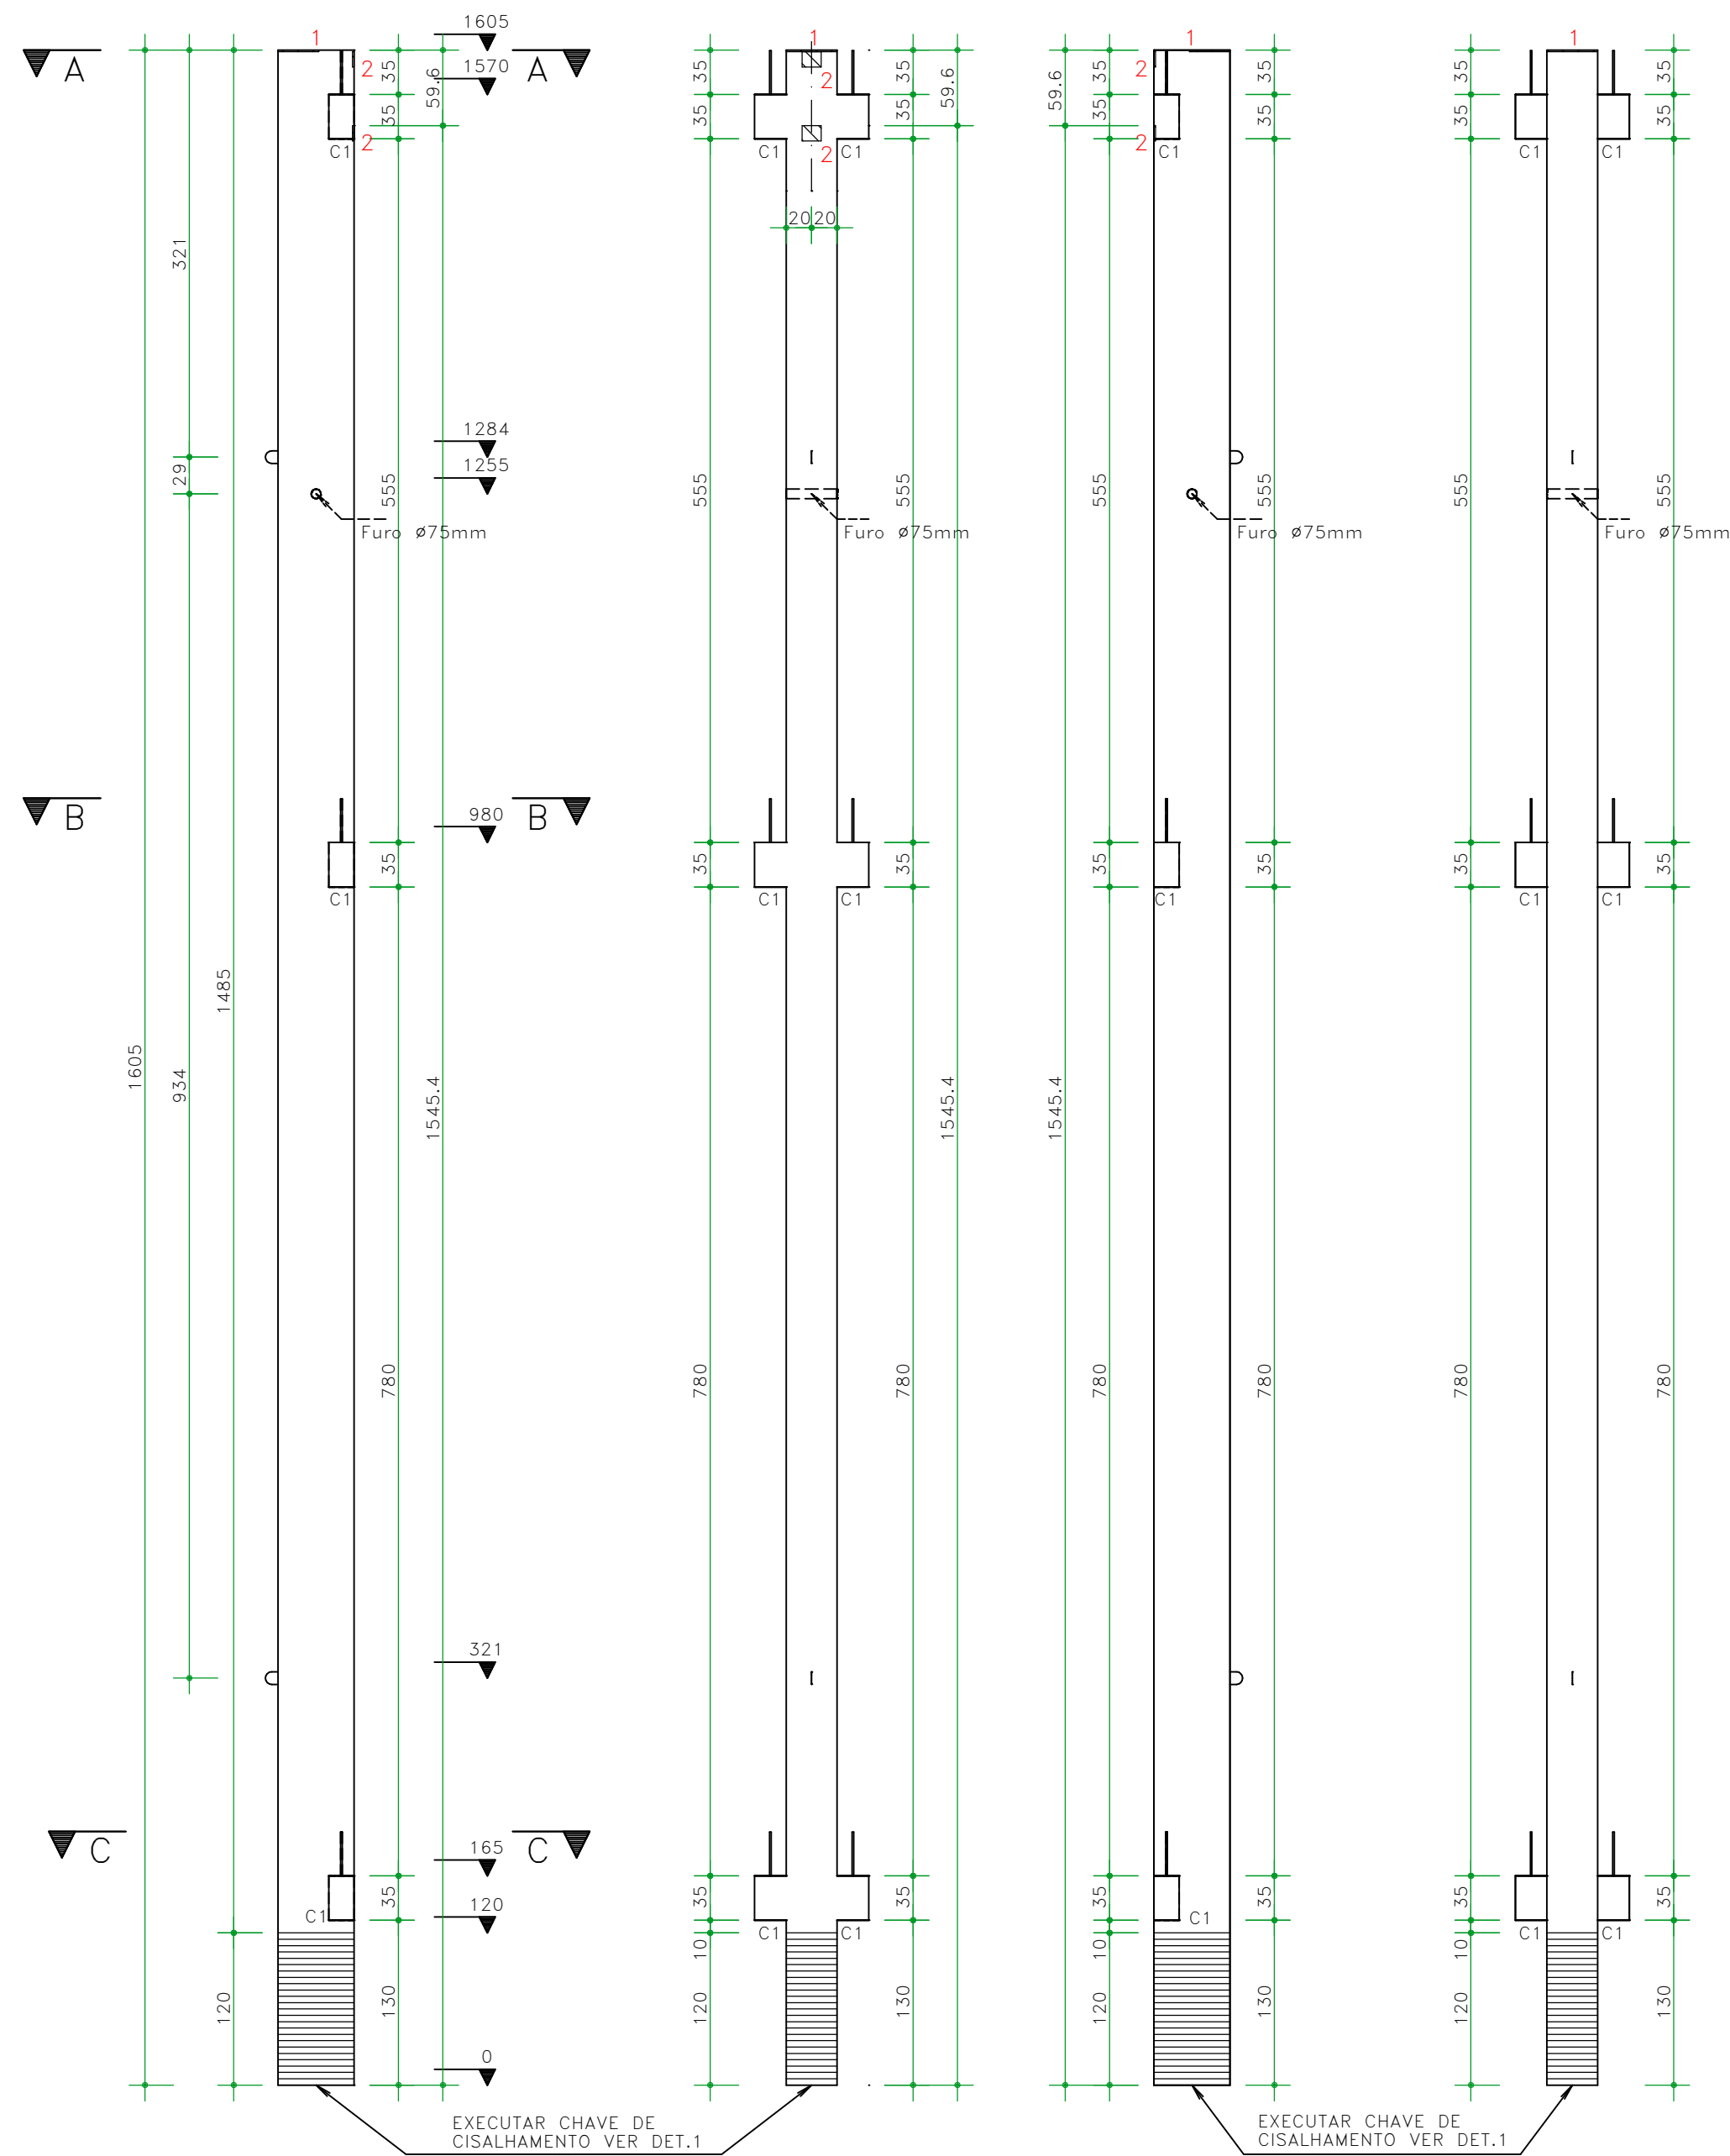
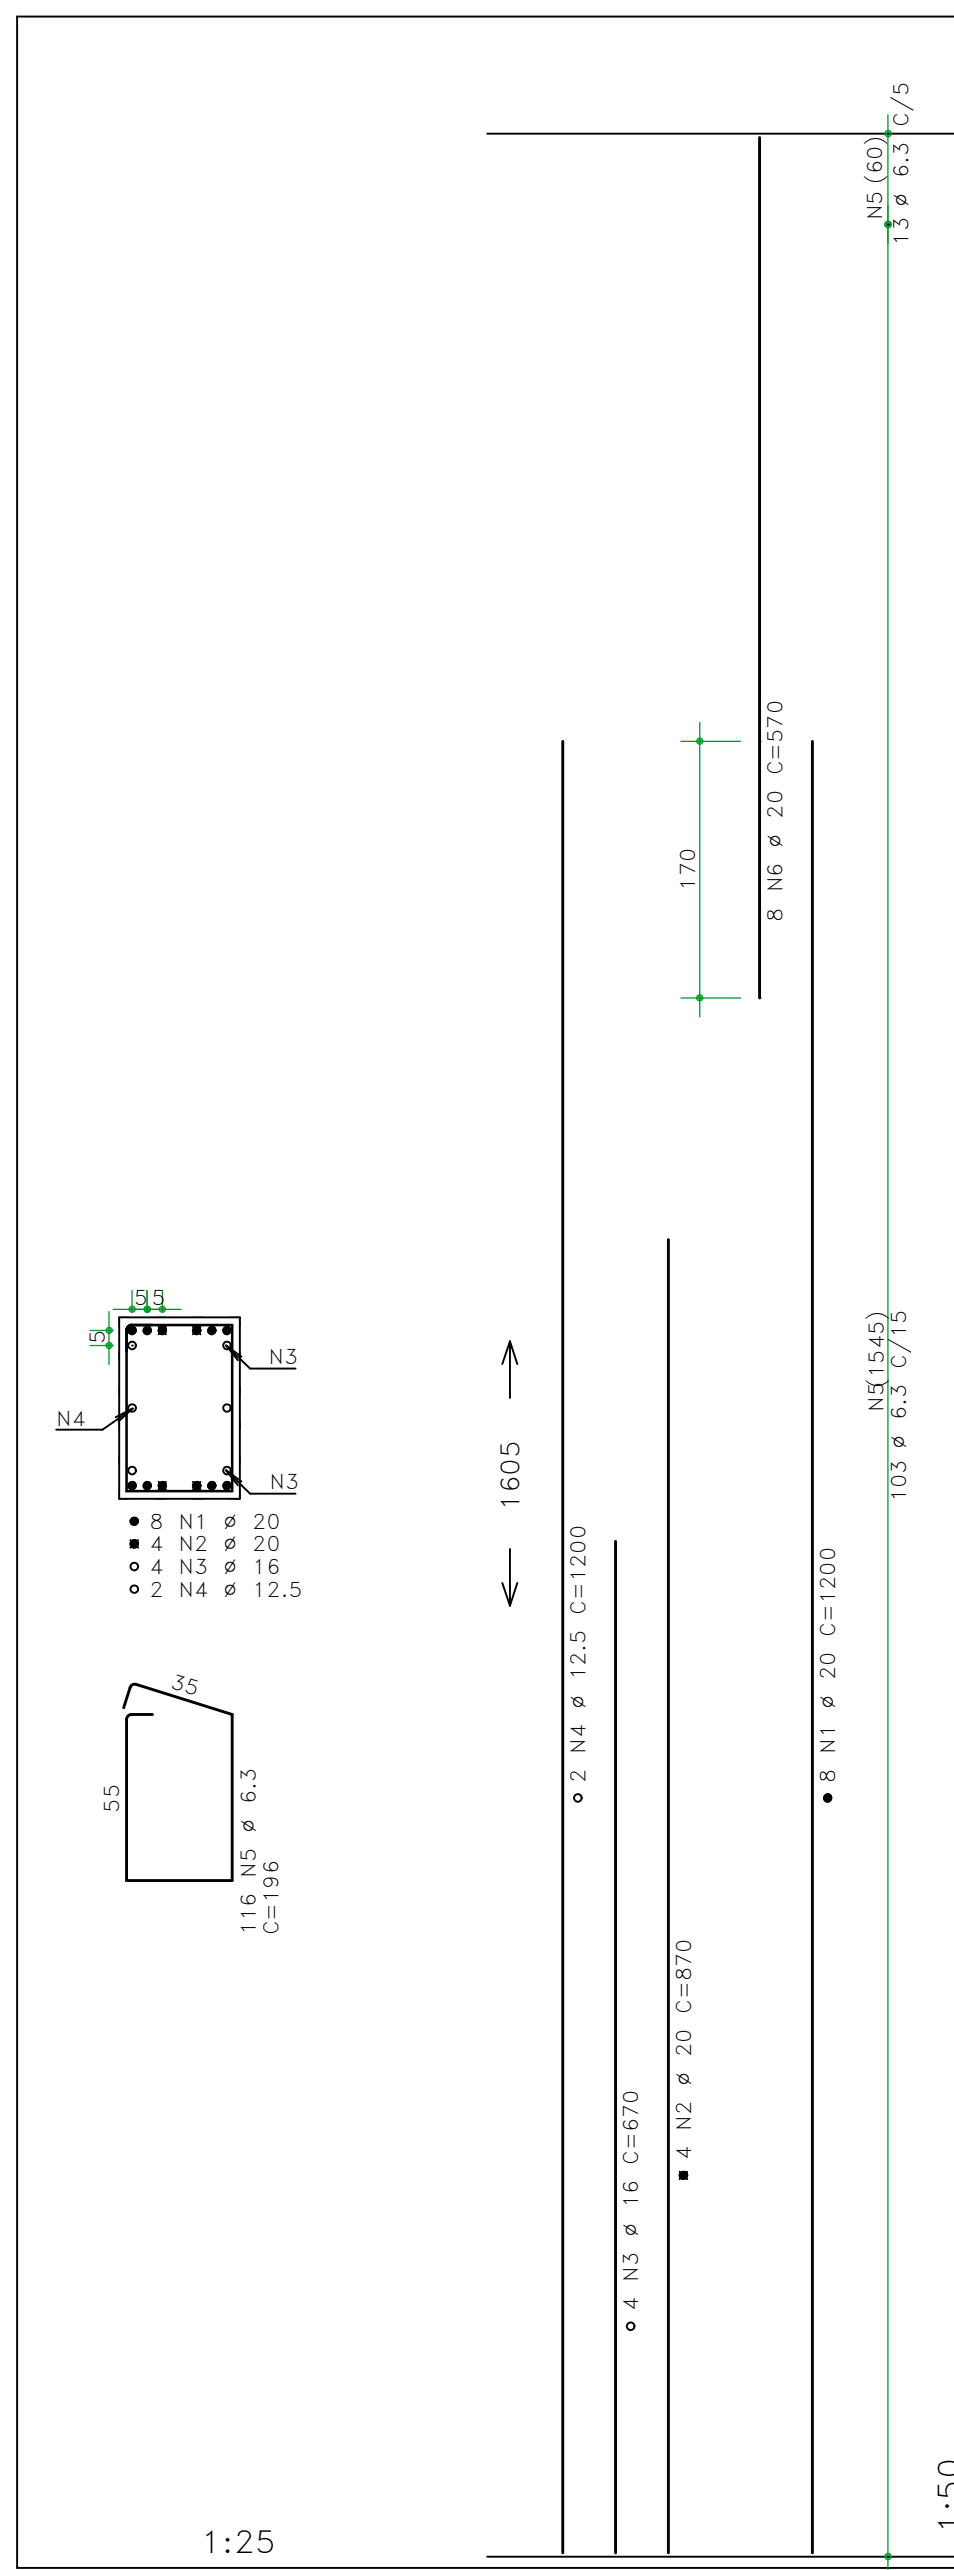


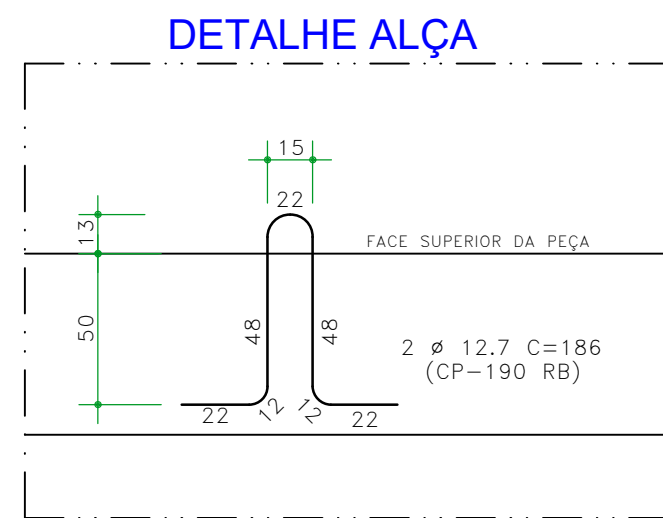

AÇO	POS	BIT	QUANT	COMPRIMENTO	
				UNIT	TOTAL
		mm		cm	cm
50A	1	20	8	1200	9600
50A	2	20	4	870	3480
50A	3	16	4	670	2680
50A	4	12,5	2	1200	2400
50A	5	6,3	116	196	22736
50A	6	20	8	570	4560

RESUMO DE AÇO			
AÇO	BIT mm	COMPR m	PESO kgf
50A	6,3	227	56
50A	12,5	24	23
50A	16	27	42
50A	20	176	435
Peso Total		50A =	556 kgf

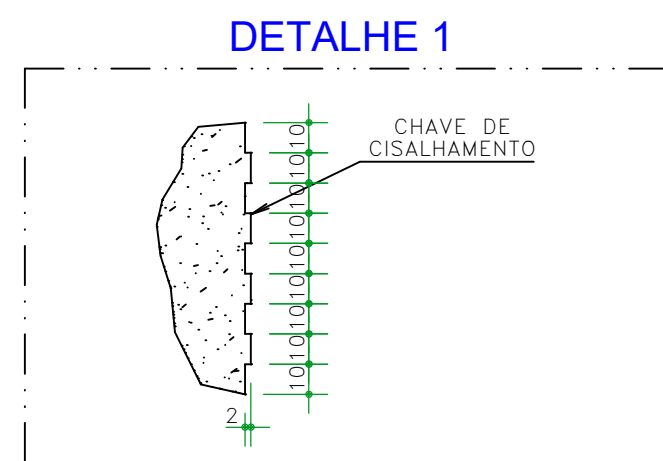

RESUMO AÇO CP 190			
AÇO	BIT mm	COMPR m	PESO kgf
CP-190 RB	12.7	3.72	3
Peso Total		CP =	3 kg

NOTAS E OBSERVAÇÕES

- 1 - MEDIDAS EM "cm"
- 2 - CARACTERÍSTICAS DO CONCRETO (CLASSE DE AGRESSIVIDADE AMBIENTAL CAA CLASSE (NBR-8953): **C 40** $E_c > 30$ GPa; Relação a/c **< 0.45**
NA DESFORMA E/OU DESPROTENSÃO: $f_{cj} = 15$ MPa e $E_c = 20$ GPa
- 3 - VOLUME / PESO DA PEÇA = **3.960** m³ / **9.890** Kg/m³
- 4 - TAXA DE AÇO NA PEÇA = **141** Kg/m³
- 5 - COBRIMENTO SOBRE A ARMAÇÃO = **2,5** cm

 BENTES ENGENHARIA DE PROJETOS	CLIENTE	INBRAC	ESCALA	1:25
	OBRA	CENTRO DE EVENTOS CUIABÁ		DATA
TÍTULO	PAVILHÃO 2 - P24 FORMA E ARMAÇÃO (1x)		DESENHO	CM
	OBRA N.	25/016	REVISÃO	0
			VERIFICAÇÃO	RFB
	 +55 (11) 98199-8507  @ruybentes.engest  /ruybentes.engest		F103	