

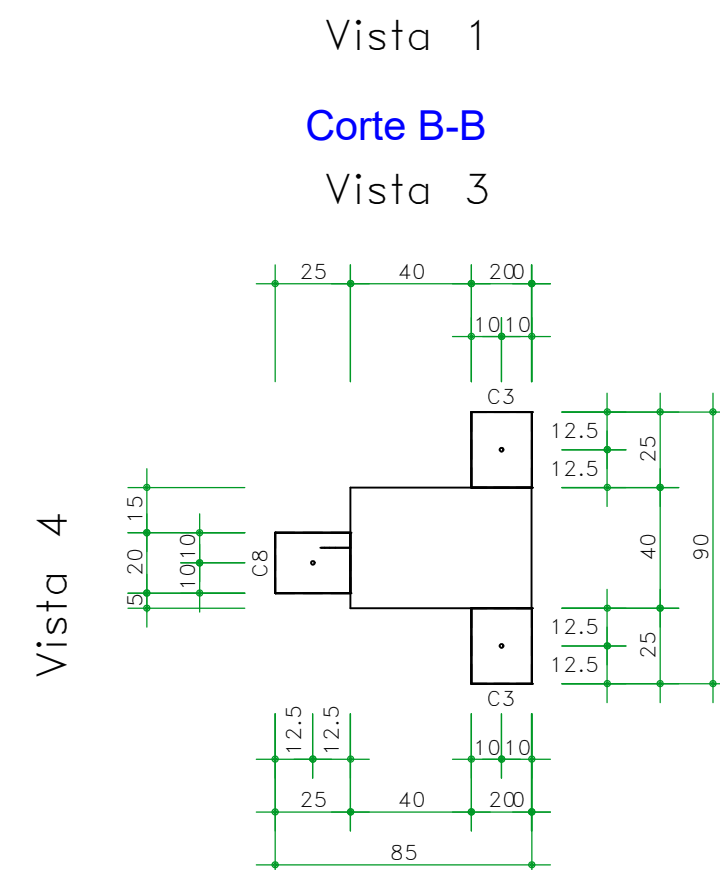
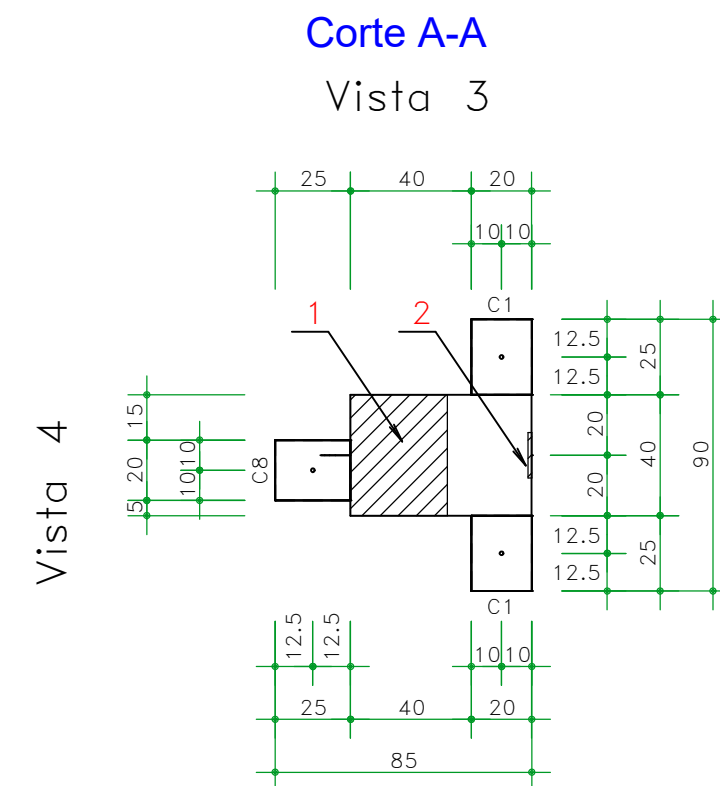
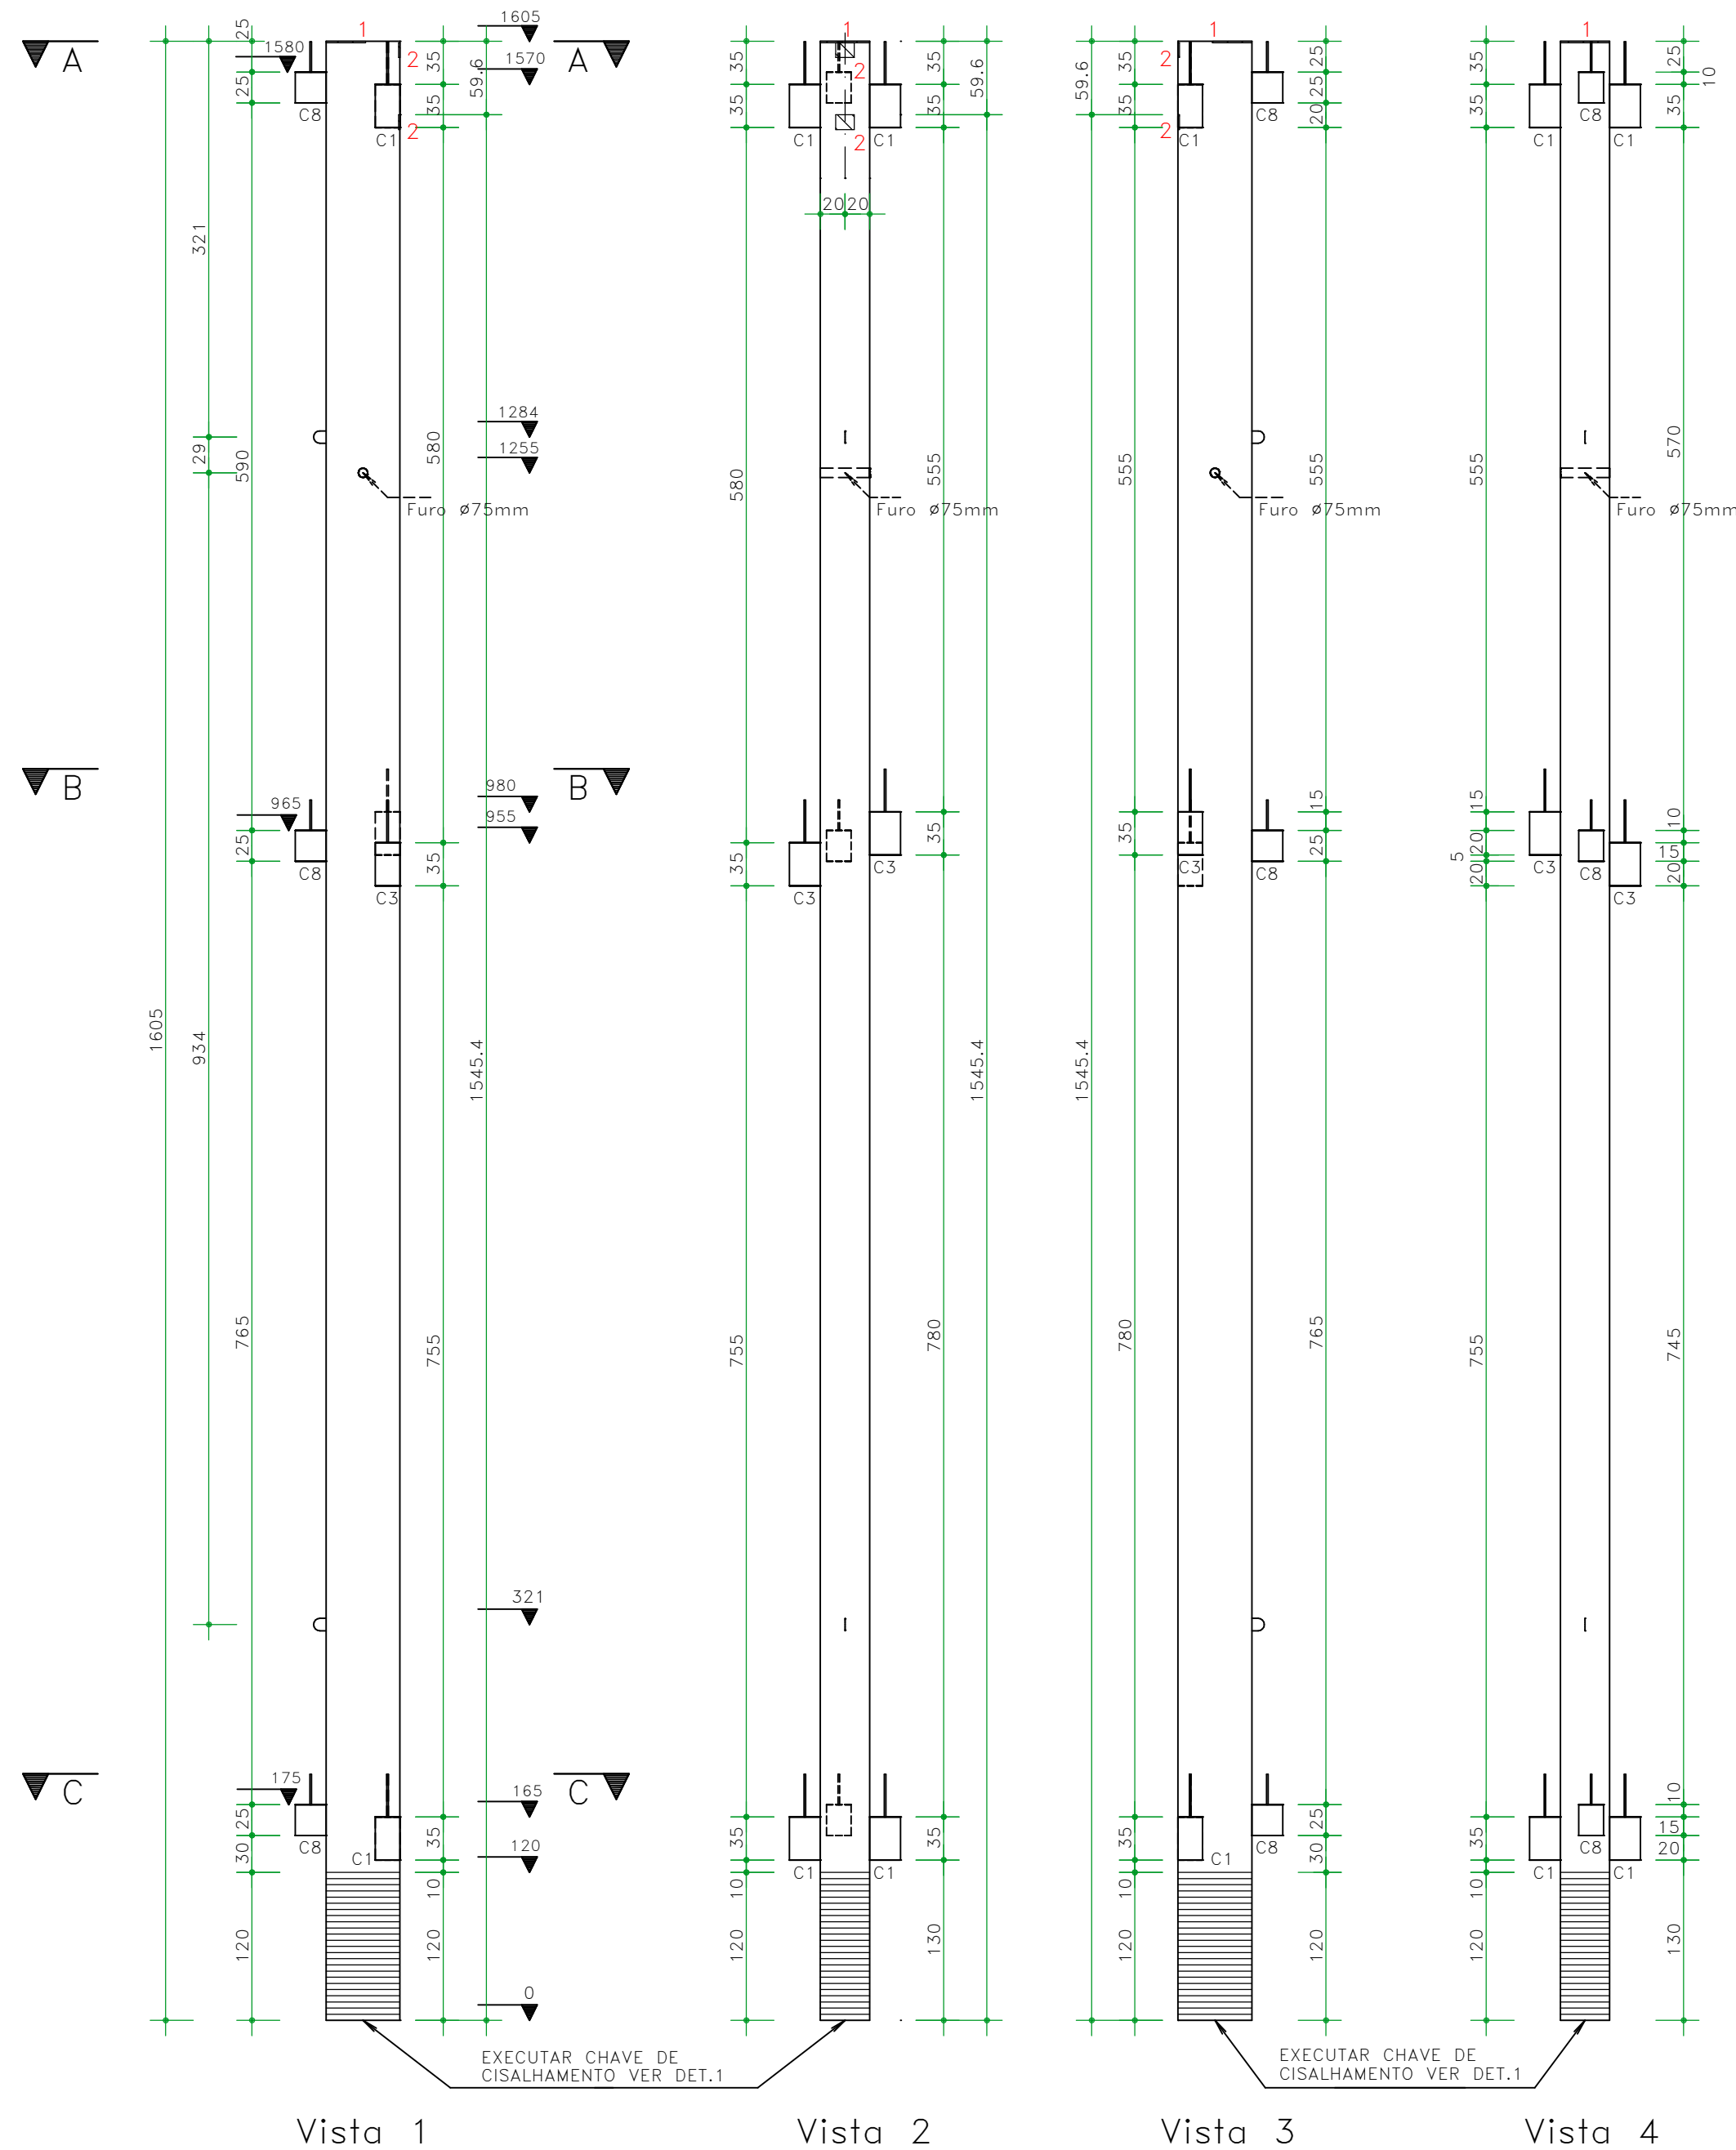


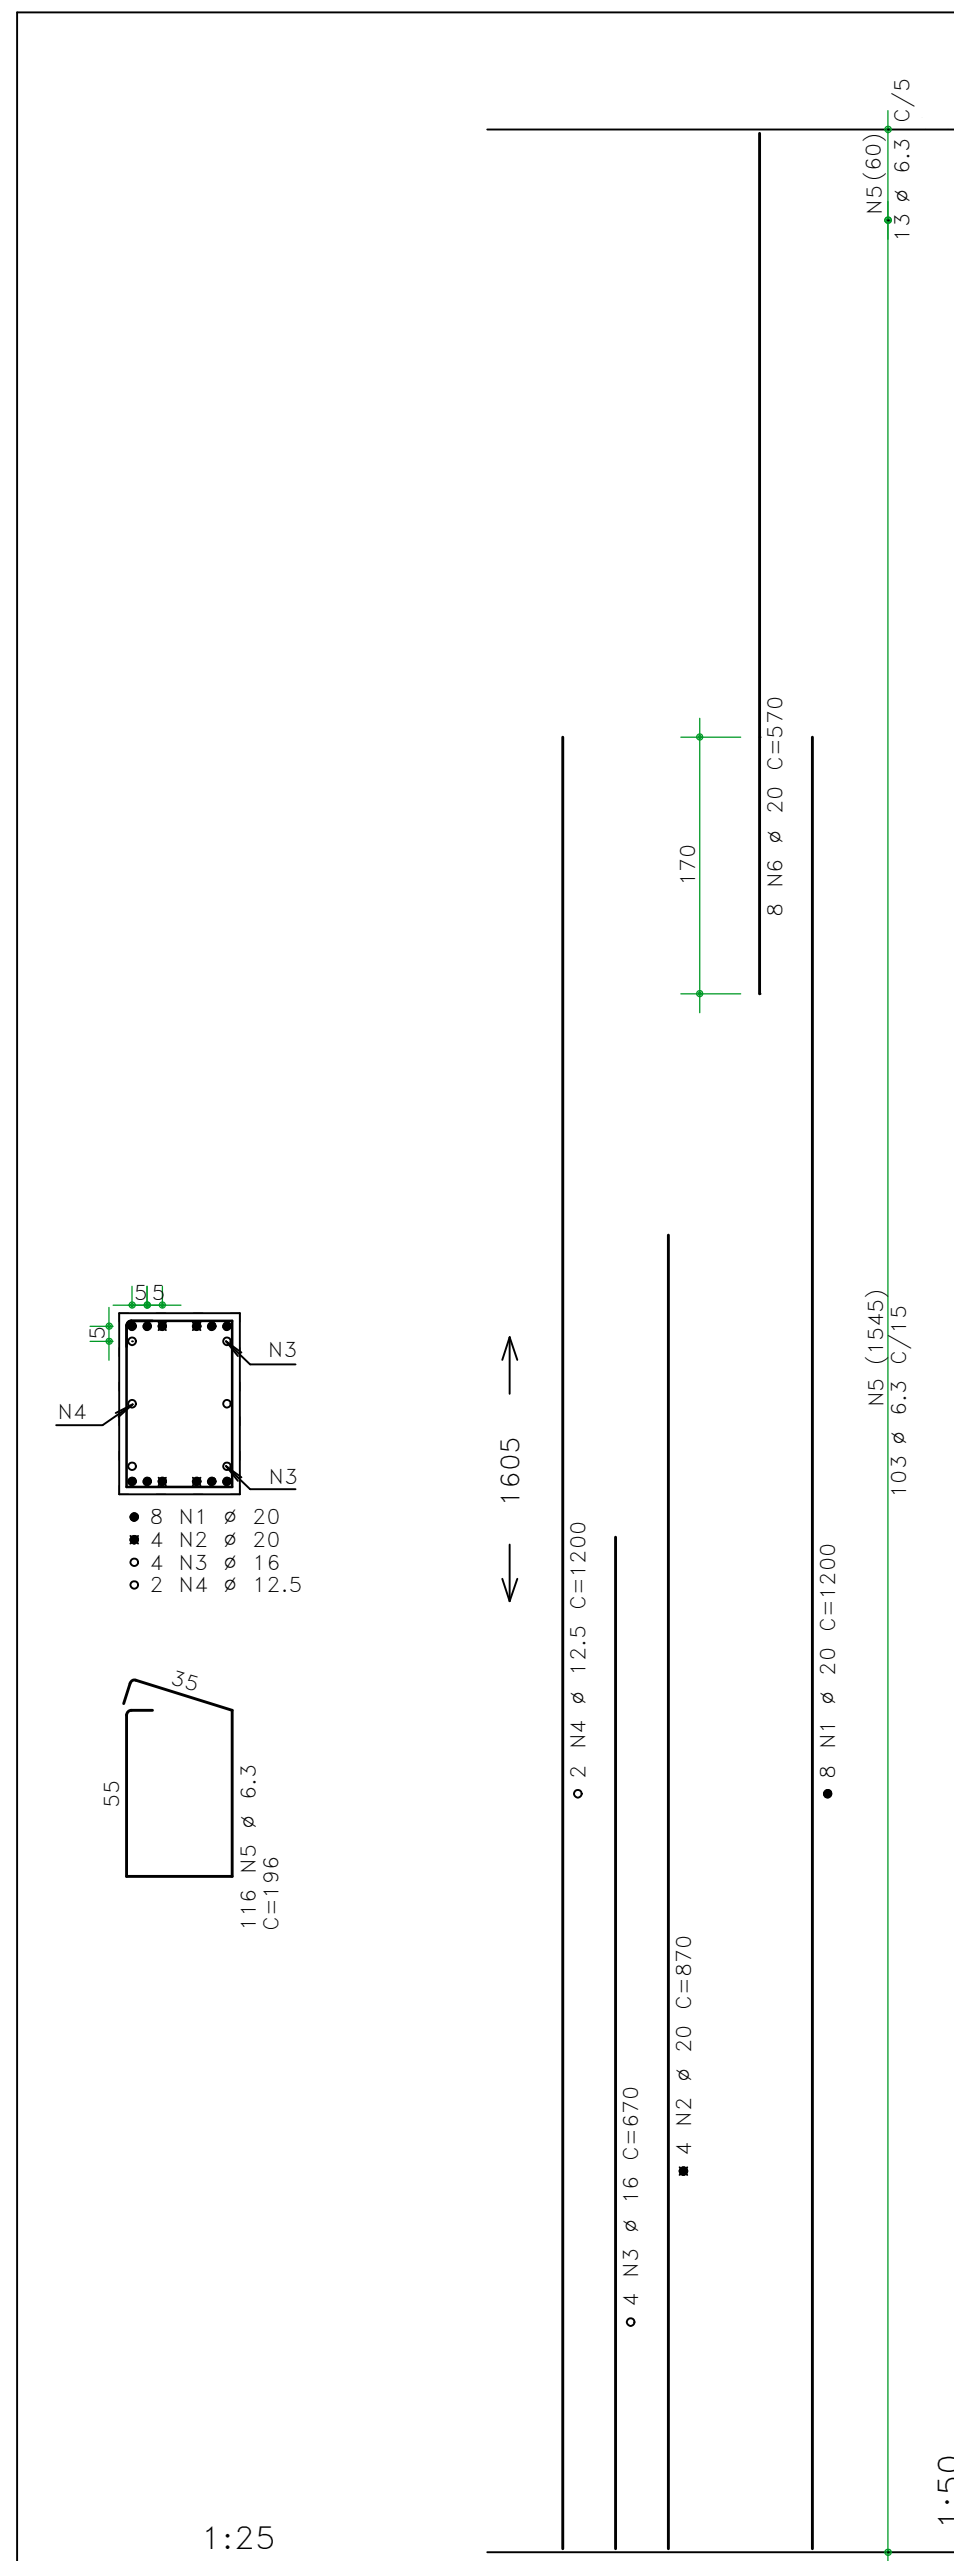



LEGENDA INSERTOS

1	MG-INS-106
2	MG-INS-105

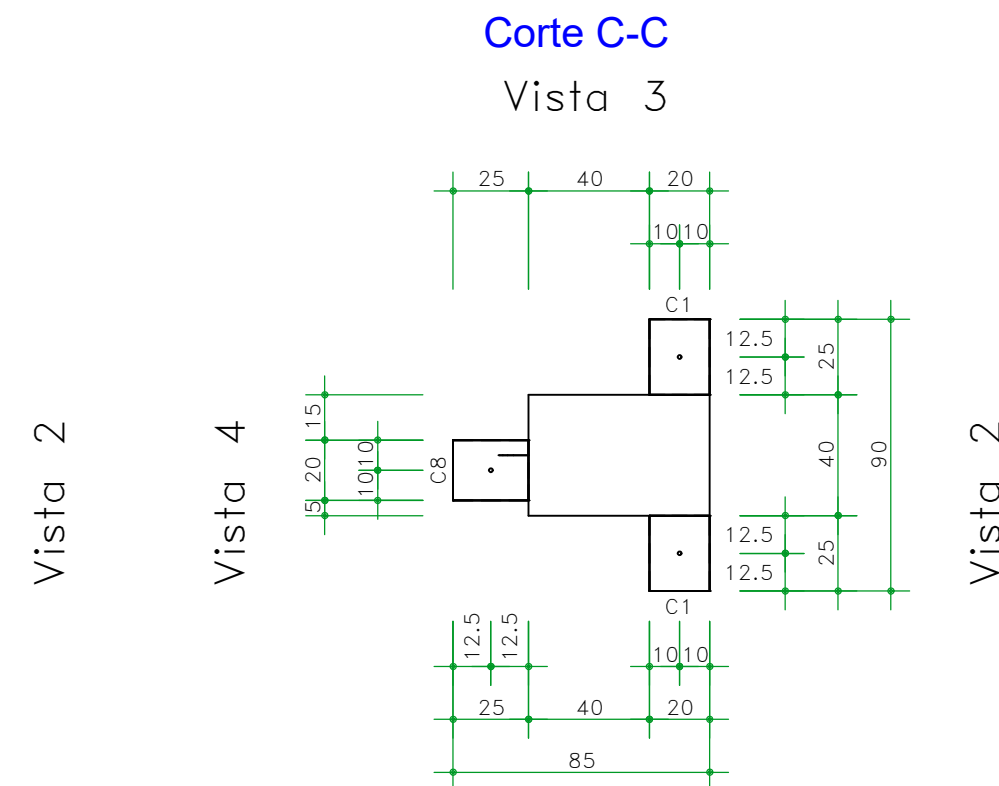

AÇO	POS	BIT	QUANT	COMPRIMENTO	
				UNIT	TOTAL
		mm		cm	cm
50A	1	20	8	1200	9600
50A	2	20	4	870	3480
50A	3	16	4	670	2680
50A	4	12,5	2	1200	2400
50A	5	6,3	116	196	22736
50A	6	20	8	570	4560

RESUMO DE AÇO			
AÇO	BIT mm	COMPR m	PESO kgf
50A	6,3	227	56
50A	12,5	24	23
50A	16	27	42
50A	20	176	435
Peso Total		50A =	556 kgf

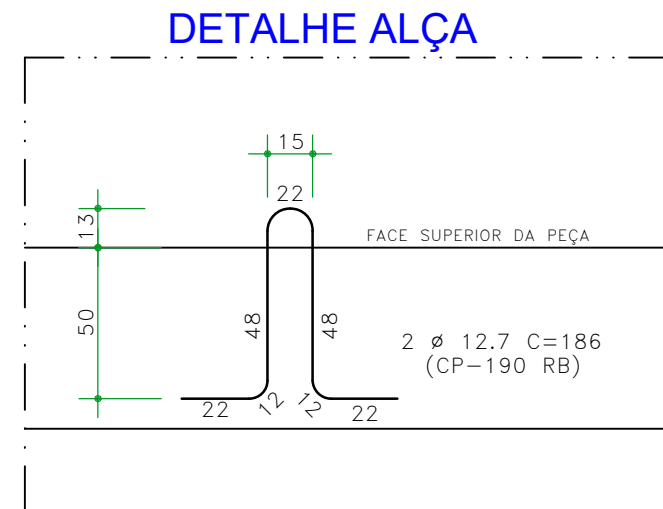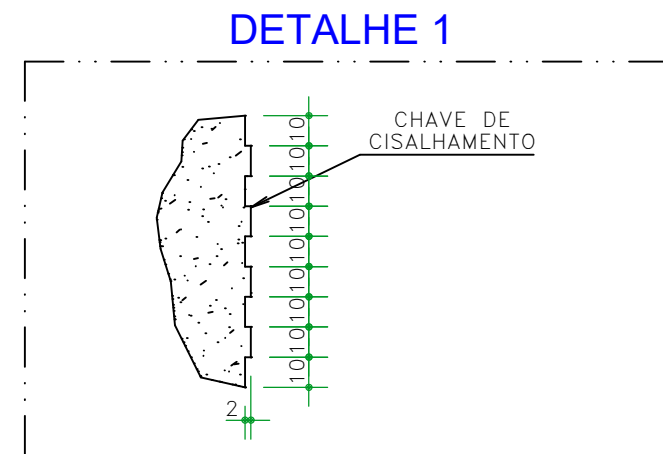

RESUMO AÇO CP 190			
AÇO	BIT mm	COMPR m	PESO kgf
CP-190 RB	12.7	3.72	3
Peso Total		CP =	3 kg

NOTAS E OBSERVAÇÕES

- 1 – MEDIDAS EM "cm"
- 2 – CARACTERÍSTICAS DO CONCRETO (CLASSE DE AGRESSIVIDADE AMBIENTAL CAA CLASSE (NBR-8953): **C 40** $E_c > 30$ GPa; Relação $\sigma/c < 0.45$ NA DESFORMA E/O DESPROTENSÃO: $f_{cj} = 15$ MPa e $E_c = 20$ GPa
- 3 – VOLUME / PESO DA PEÇA = **3.990** m³ / **9.980** Kg/m³
- 4 – TAXA DE AÇO NA PEÇA = **140** Kg/m³
- 5 – COBRIMENTO SOBRE A ARMAÇÃO = **2,5** cm

 BENTES ENGENHARIA DE PROJETOS	CLIENTE	INBRAC	ESCALA	1:25	
	OBRA	CENTRO DE EVENTOS CUIABÁ	DATA	24/03/2026	
	TÍTULO	PAVILHÃO 2 - P40 FORMA E ARMAÇÃO (1x)	DESENHO	CM	
	OBRA N.	25/016	FOLHA N.	0	
		F104		VERIFICAÇÃO	RFB