

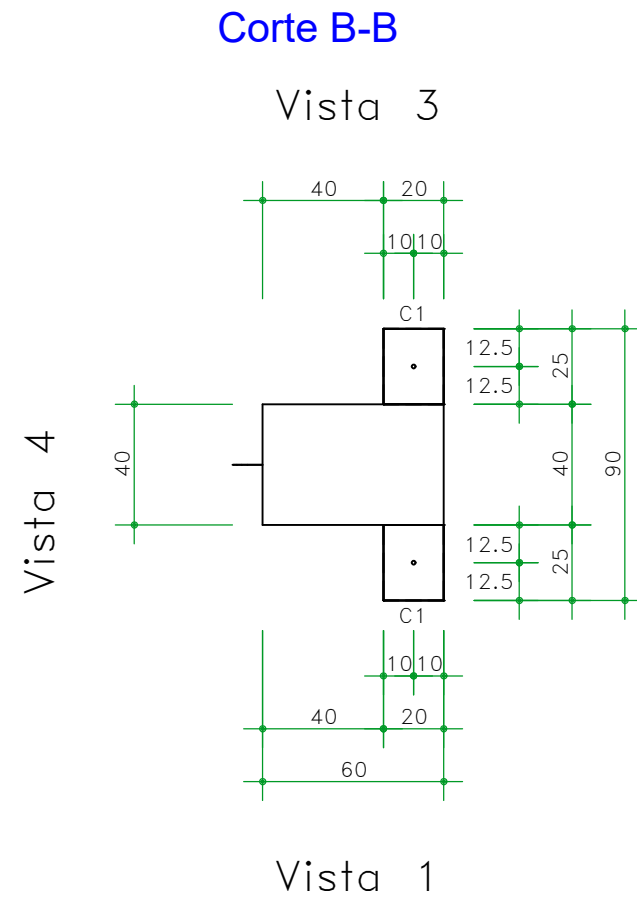
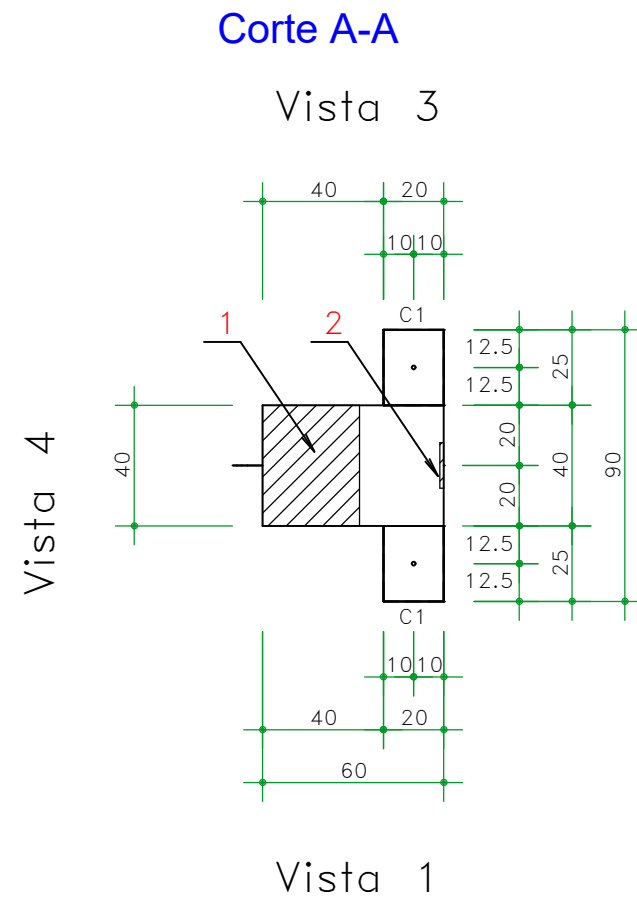
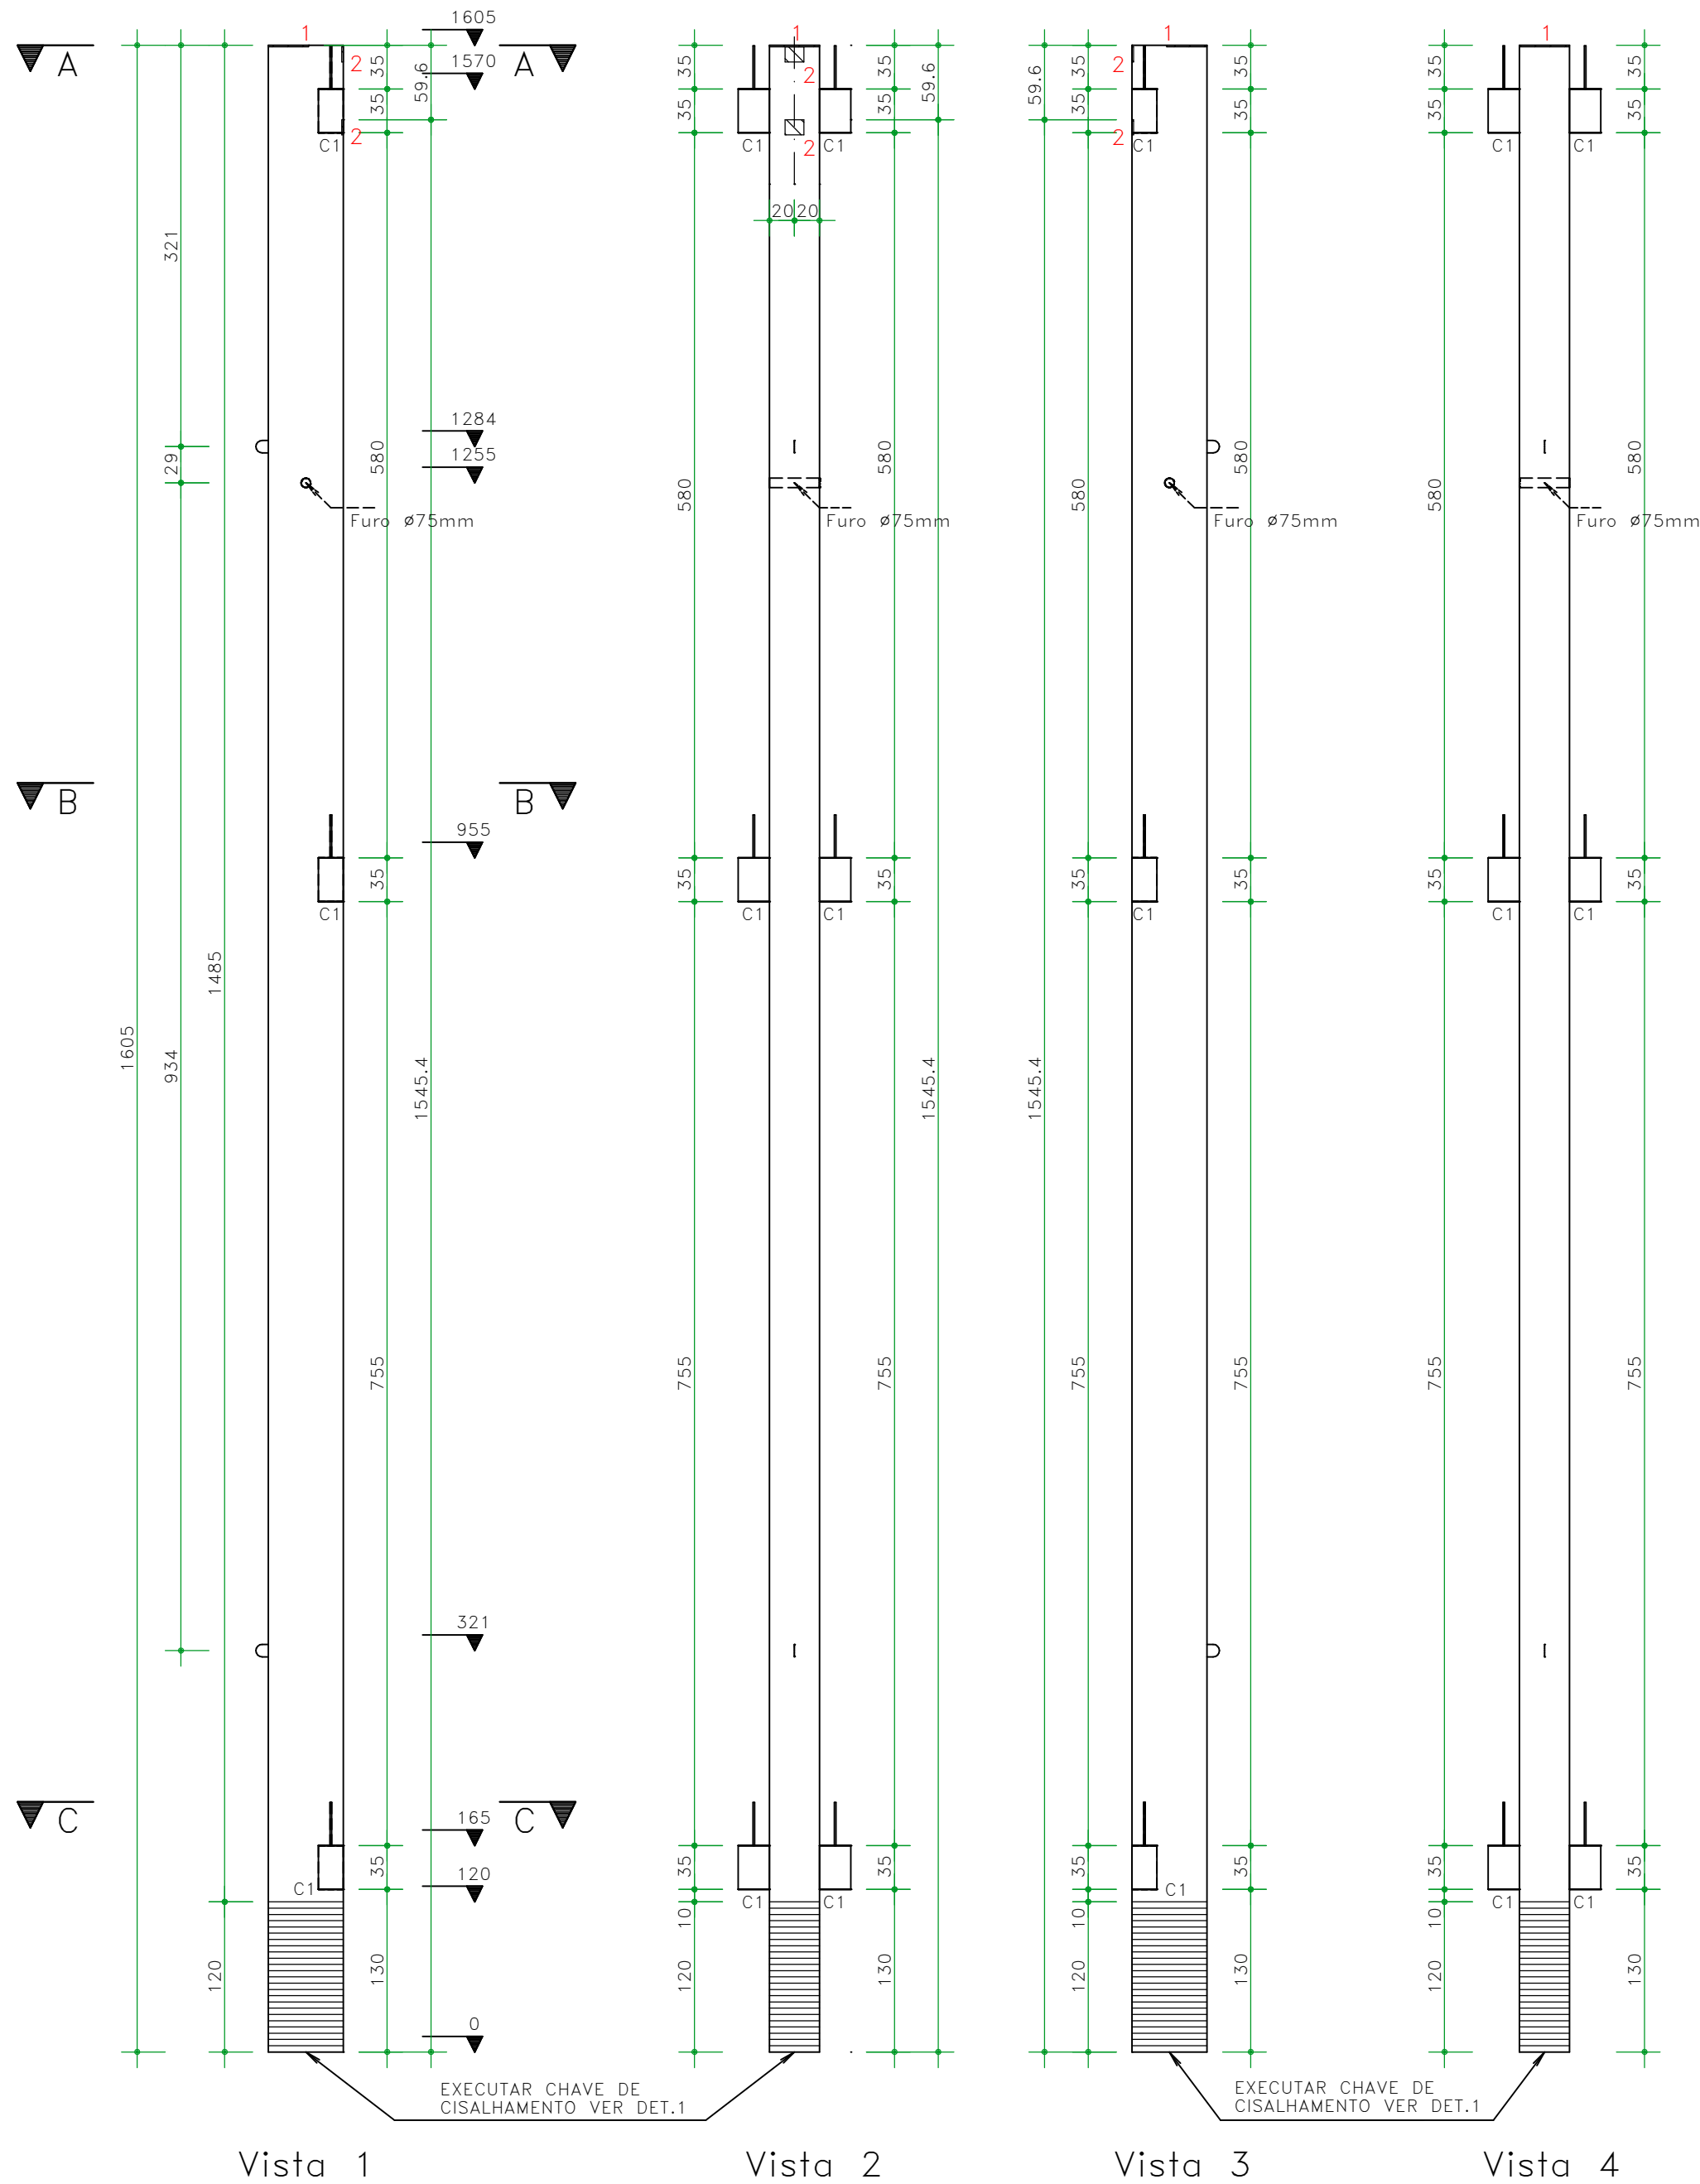



SAUT-BE 2019, ENG. DE ESTRUTURAS S/C LTDA PL F105-CEC-PV2-P48-R01.PLT

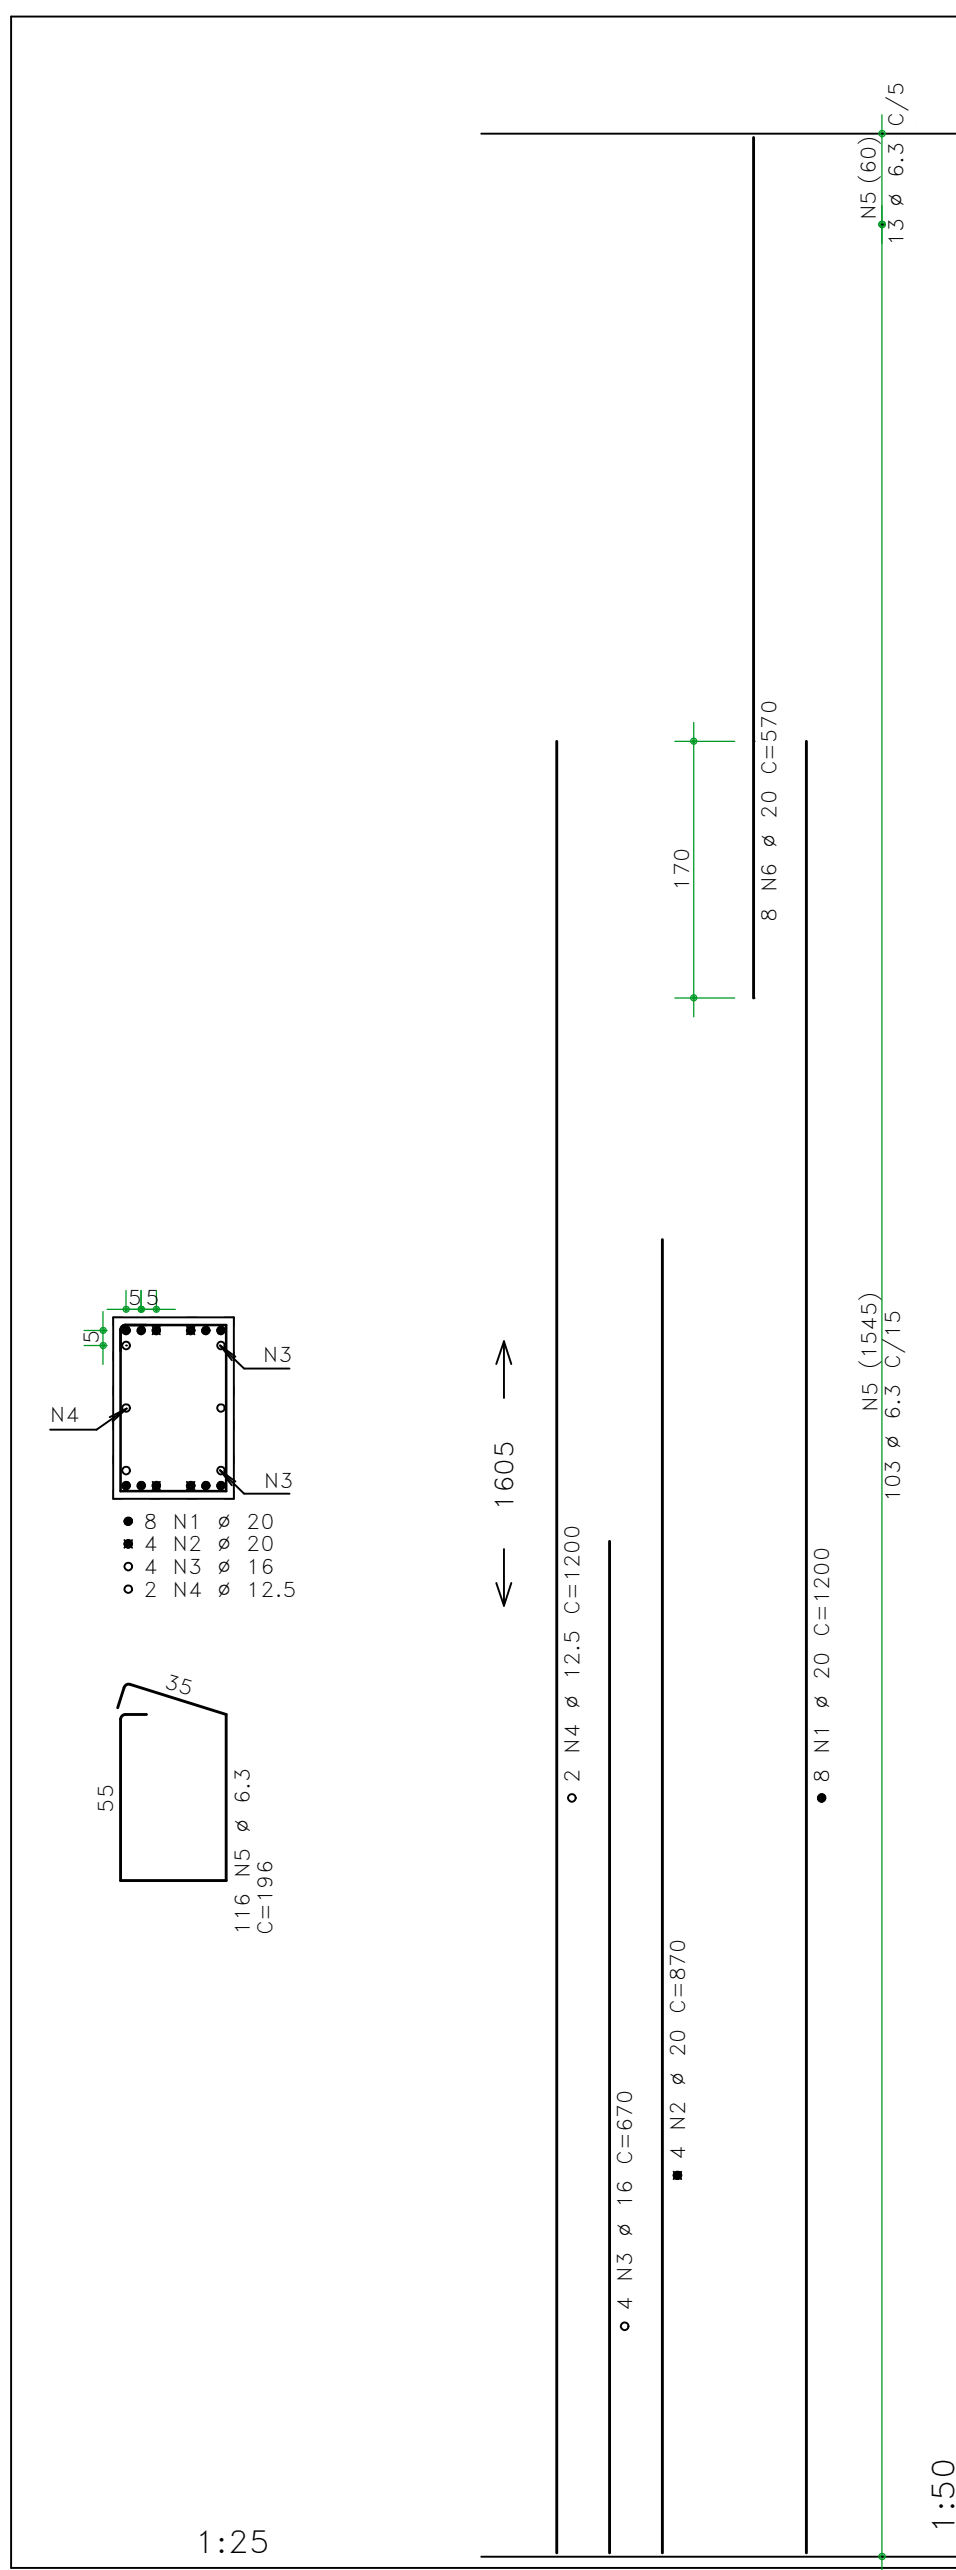


LEGENDA INSERTOS	
1	MG-INS-106
2	MG-INS-105

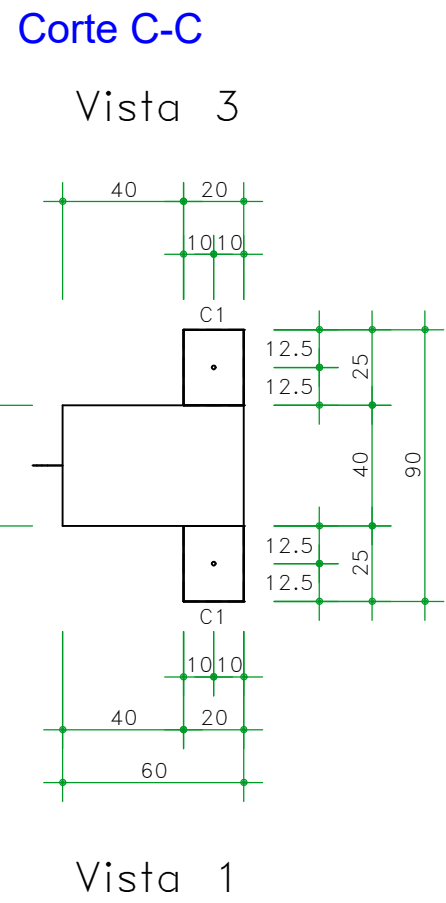

DETALHE 1

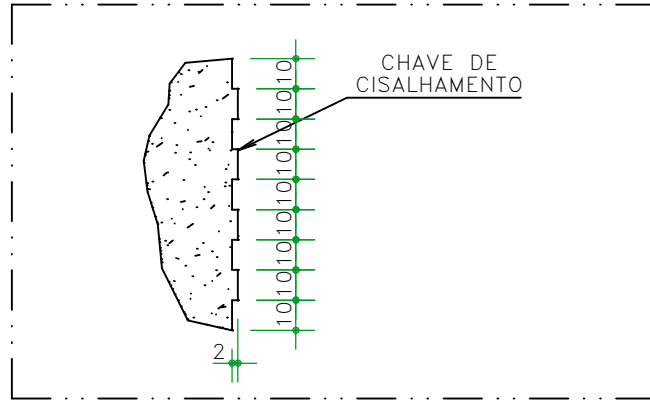

DETALHE ALÇA

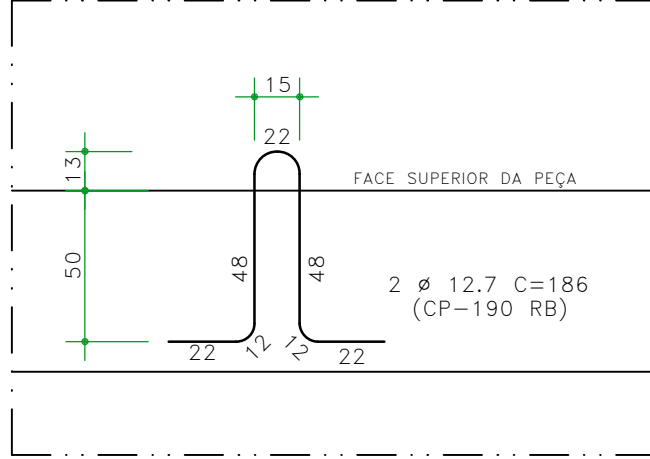

RESUMO AÇO CP 190			
AÇO	BIT	COMPR	PESO
CP-190 RB	12.7	3.72	3
Peso Total		CP =	3 kg

NOTAS E OBSERVAÇÕES

- MEDIDAS EM "cm"
- CARACTERÍSTICAS DO CONCRETO (CLASSE DE AGRESSIVIDADE AMBIENTAL CAA II)
CLASSE (NBR-8953): **C 40** $E_c > 30$ GPa; Relação $a/c < 0.45$
NA DESFORMA E/OU DESPOTENSÃO: $f_{cj} = 15$ MPa e $E_c = 20$ GPa
- VOLUME / PESO DA PEÇA = **3,950** m³ / **9.890** Kg/m
- TAXA DE AÇO NA PEÇA = **142** Kg/m³
- COBRIMENTO SOBRE A ARMAÇÃO = **2,5** cm



TÍTULO
PAVILHÃO 2 - P48=P65
FORMA E ARMAÇÃO (2x)

CLIENTE
INBRAC
OBRA
CENTRO DE EVENTOS CUIABÁ

OBRA N.
25/016

FOLHA N.
2

REVISÃO
0

VERIFICAÇÃO
RFB

ESCALA
1:25

DATA
24/03/2026

DESENHO
CM

+55 (11) 98199-8507

@ruybentes.engest

/ruybentes.engest