

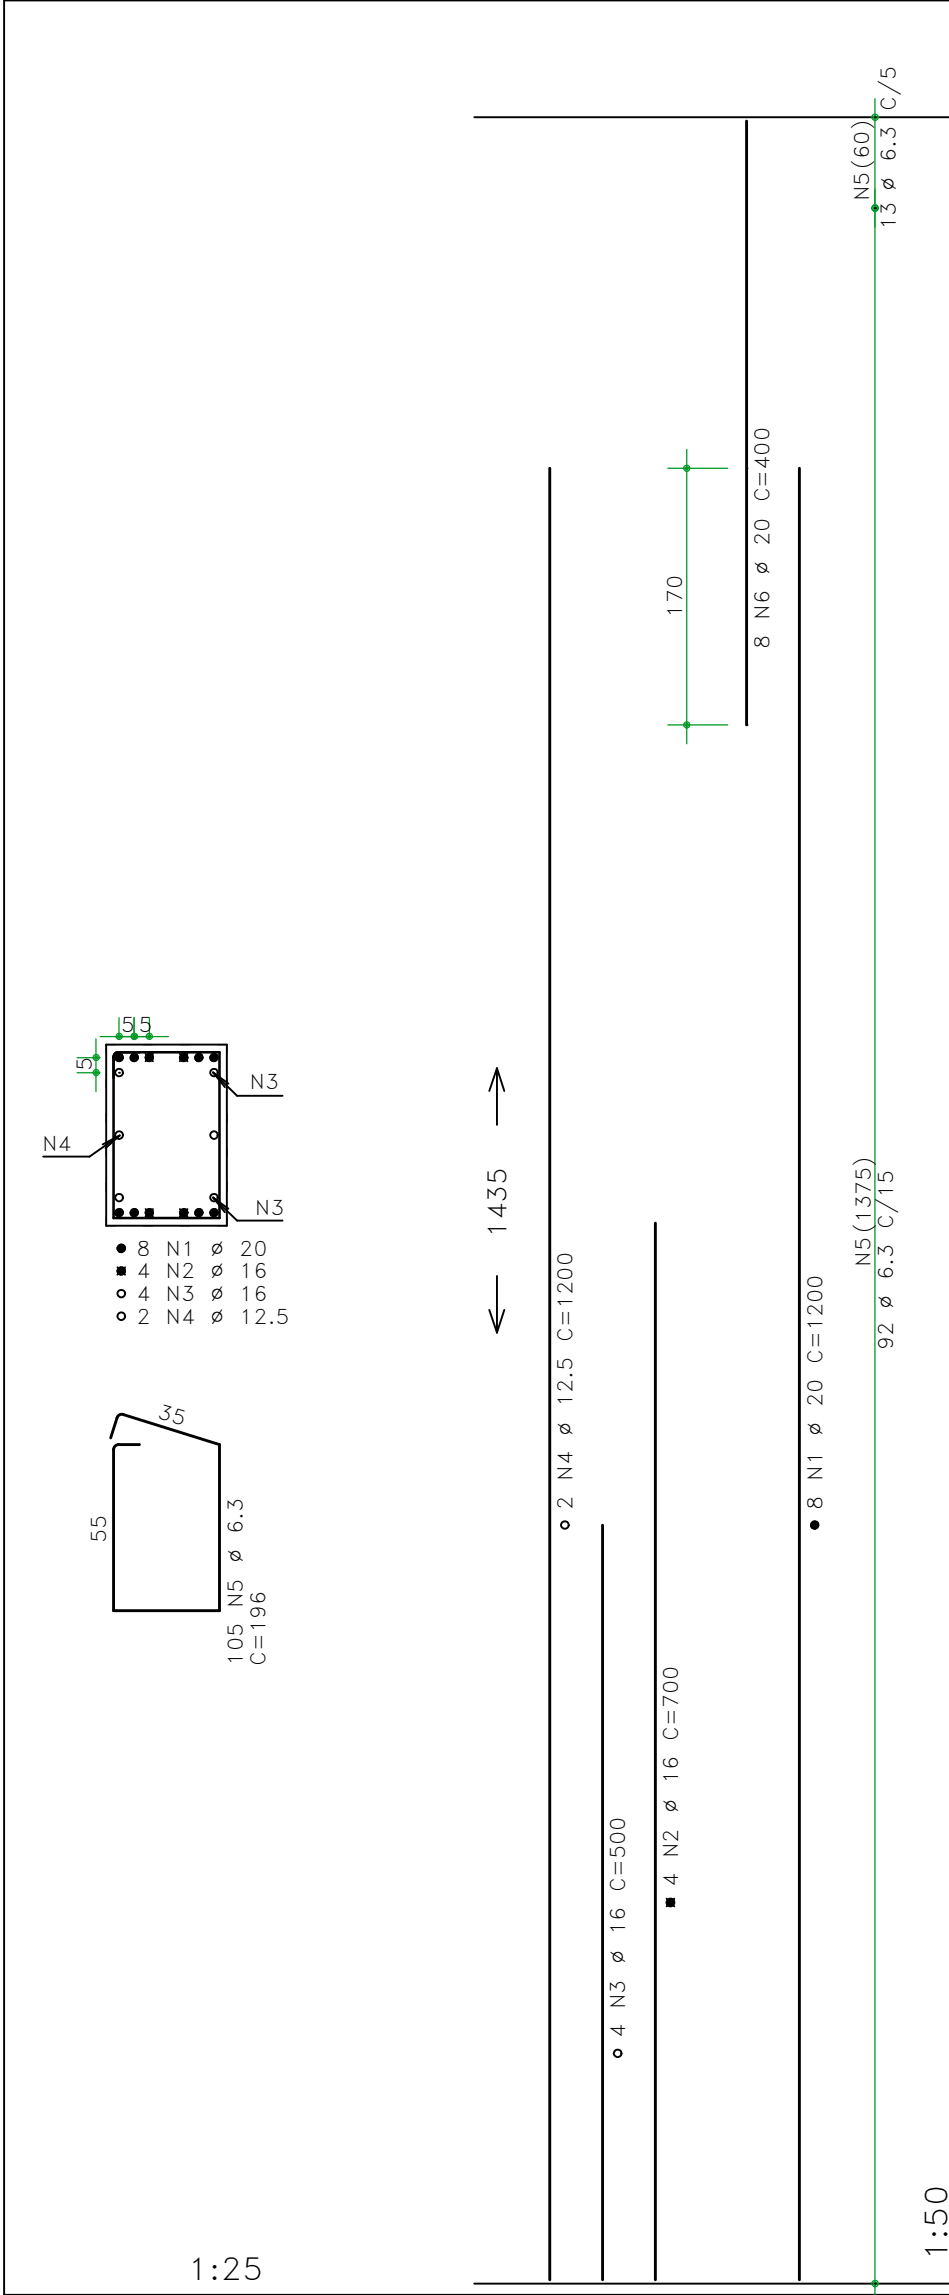
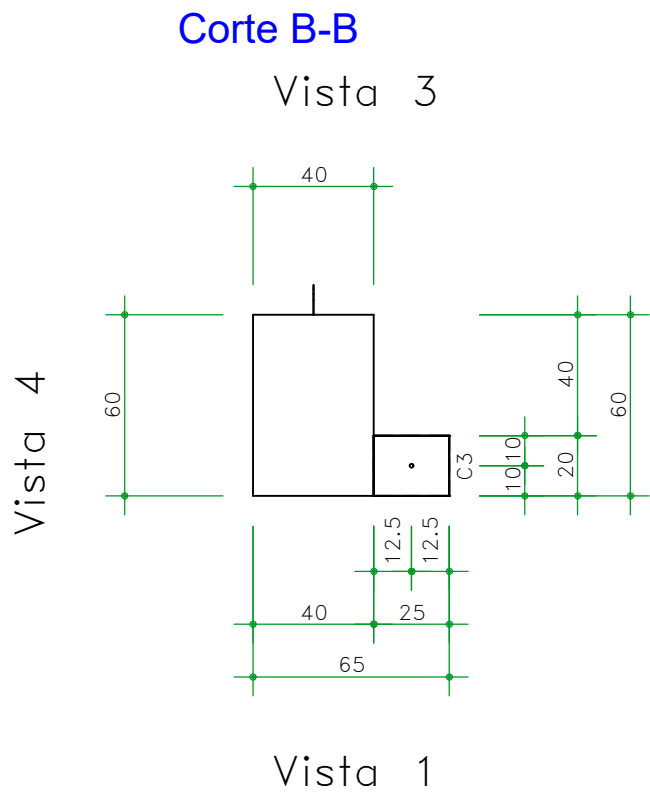


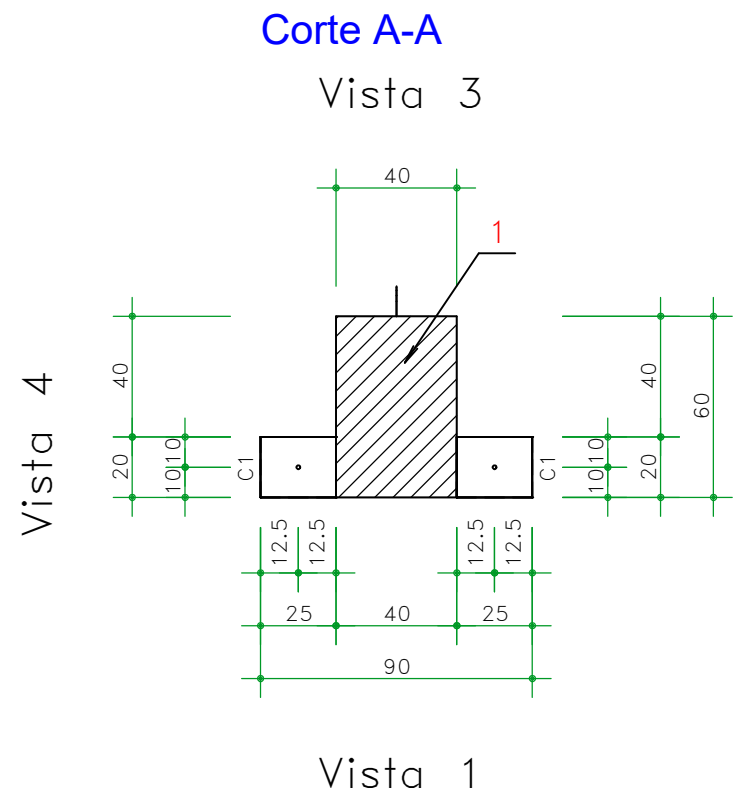




AÇO	POS	BIT	QUANT	COMPRIMENTO	
				UNIT	TOTAL
		mm		cm	cm
50A	1	20	8	1200	9600
50A	2	16	4	700	2800
50A	3	16	4	500	2000
50A	4	12.5	2	1200	2400
50A	5	6.3	105	196	20580
50A	6	20	8	400	3200

RESUMO DE AÇO			
AÇO	BIT	COMPR	PESO
	mm	m	kgf
50A	6.3	206	50
50A	12.5	24	23
50A	16	48	76
50A	20	128	316
Peso Total	50A =		465 kgf

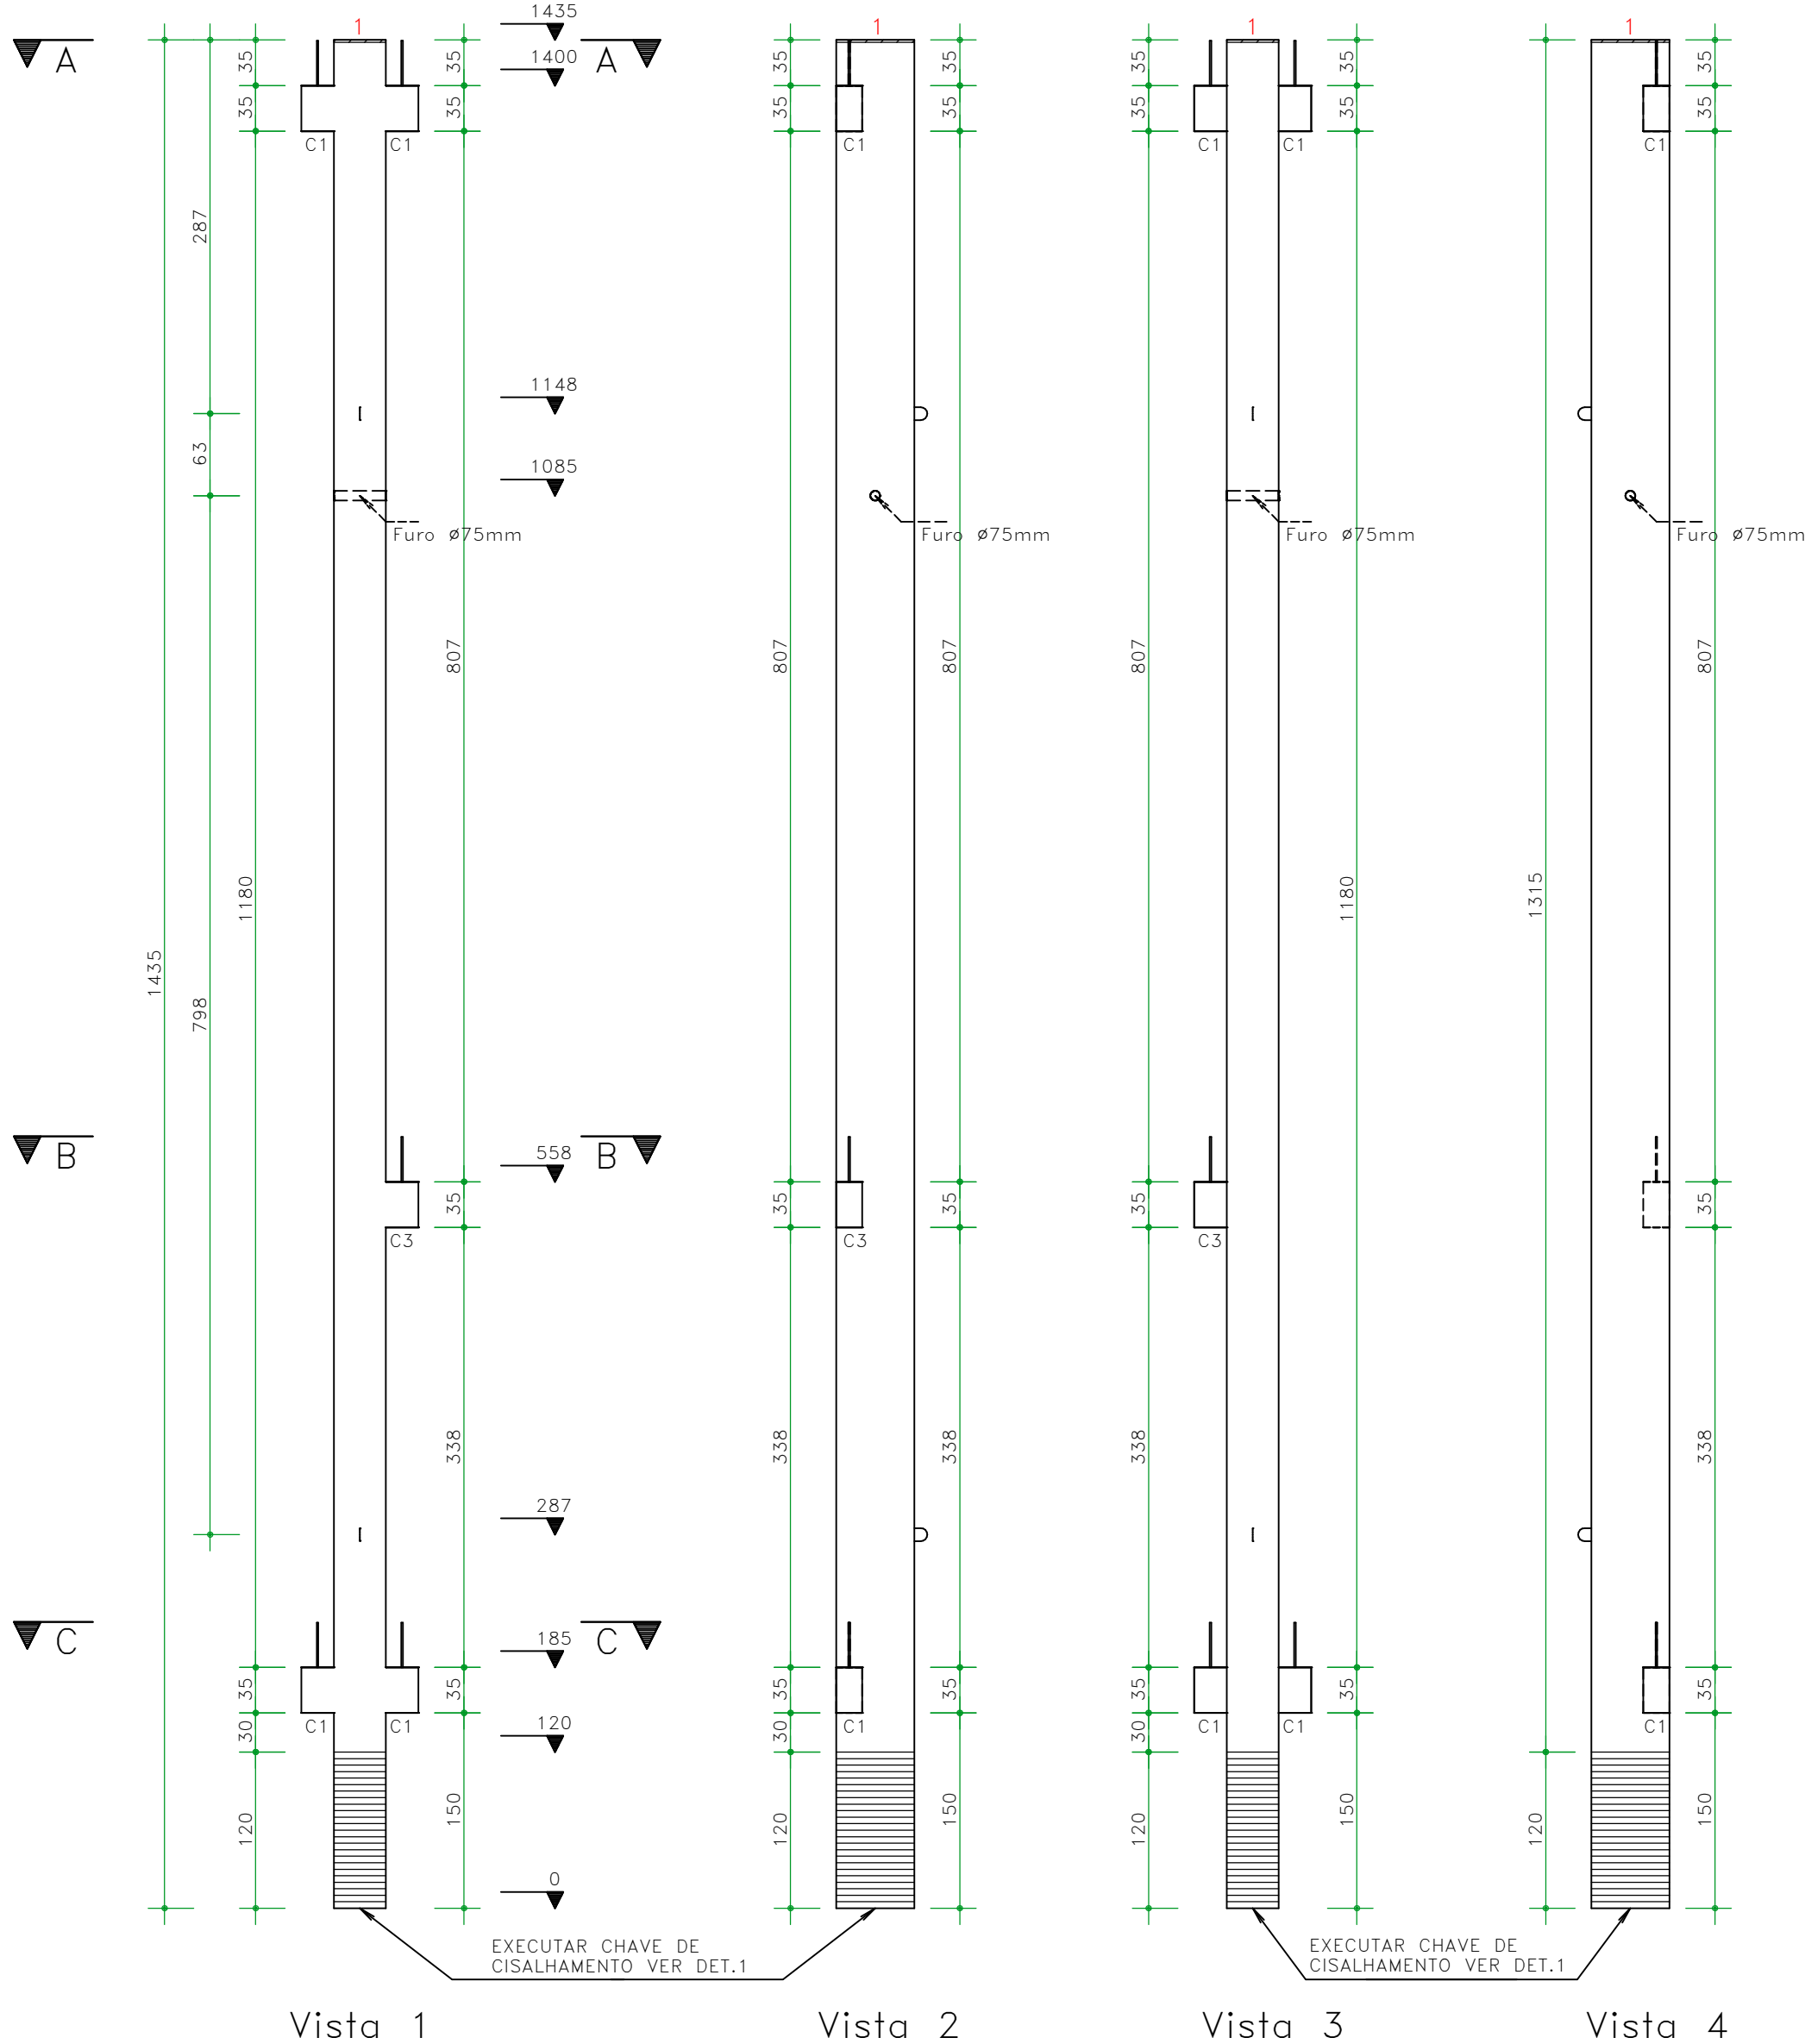

LEGENDA INSERTOS

1	MG-INS-101
---	------------

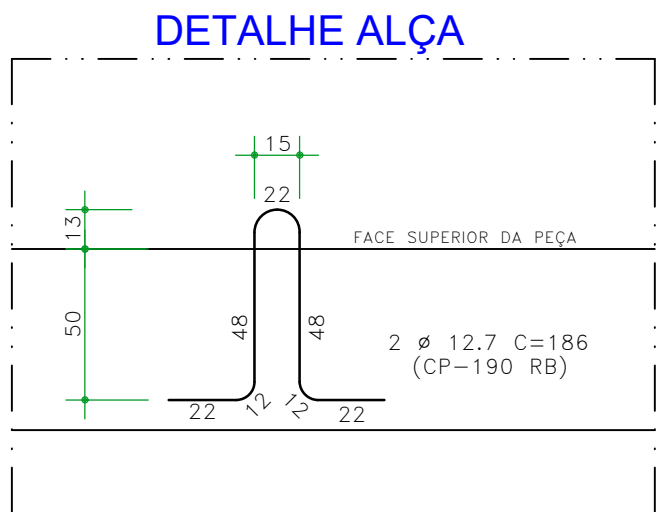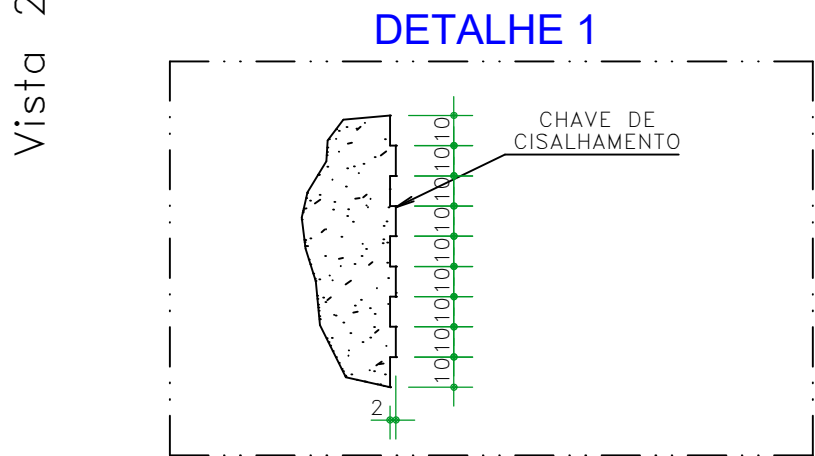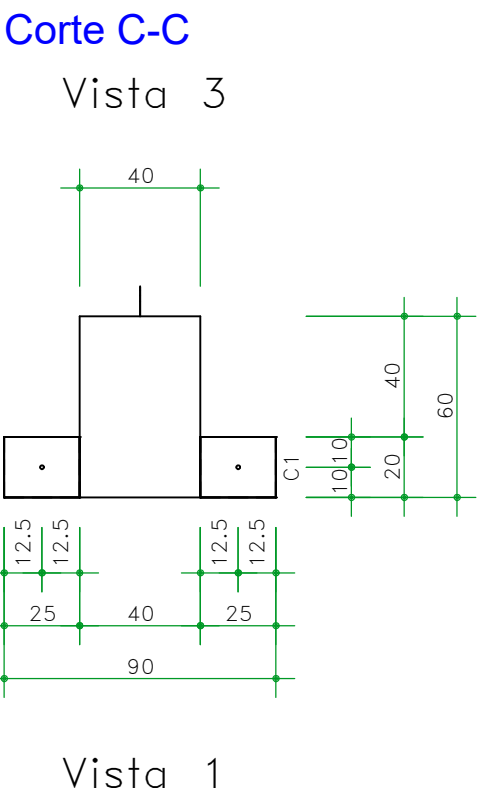

RESUMO AÇO CP 190			
AÇO	BIT	COMPR	PESO
	mm	m	kgf
CP-190 RB	12.7	3.72	3
Peso Total	CP =		3 kg

NOTAS E OBSERVAÇÕES

- 1 - MEDIDAS EM "cm"
- 2 - CARACTERÍSTICAS DO CONCRETO (CLASSE DE AGRESSIVIDADE AMBIENTAL CAA II)
CLASSE (NBR-8953): **C 40** $E_c > 30$ GPa; Relação $a/c < 0.45$
NA DESFORMA E/OU DESPOTENSÃO: $f_{cj} = 15$ MPa e $E_c = 20$ GPa
- 3 - VOLUME / PESO DA PEÇA = **3,530** m³ / **8.830** Kg/m³
- 4 - TAXA DE AÇO NA PEÇA = **133** Kg/m³
- 5 - COBRIMENTO SOBRE A ARMAÇÃO = **2,5** cm



	CLIENTE		ESCALA	
	INBRAC		1:25	
TÍTULO	OBRA		DATA	
	CENTRO DE EVENTOS CUIABÁ		25/03/2026	
PAVILHÃO 2 - P81 FORMA E ARMAÇÃO (1x)	OBRA N.		DESENHO	
			CM	
	FOLHA N.		REVISÃO	
			0	
			VERIFICAÇÃO	
			RFB	
 +55 (11) 98199-8507  @ruybentes.engest  /ruybentes.engest				