

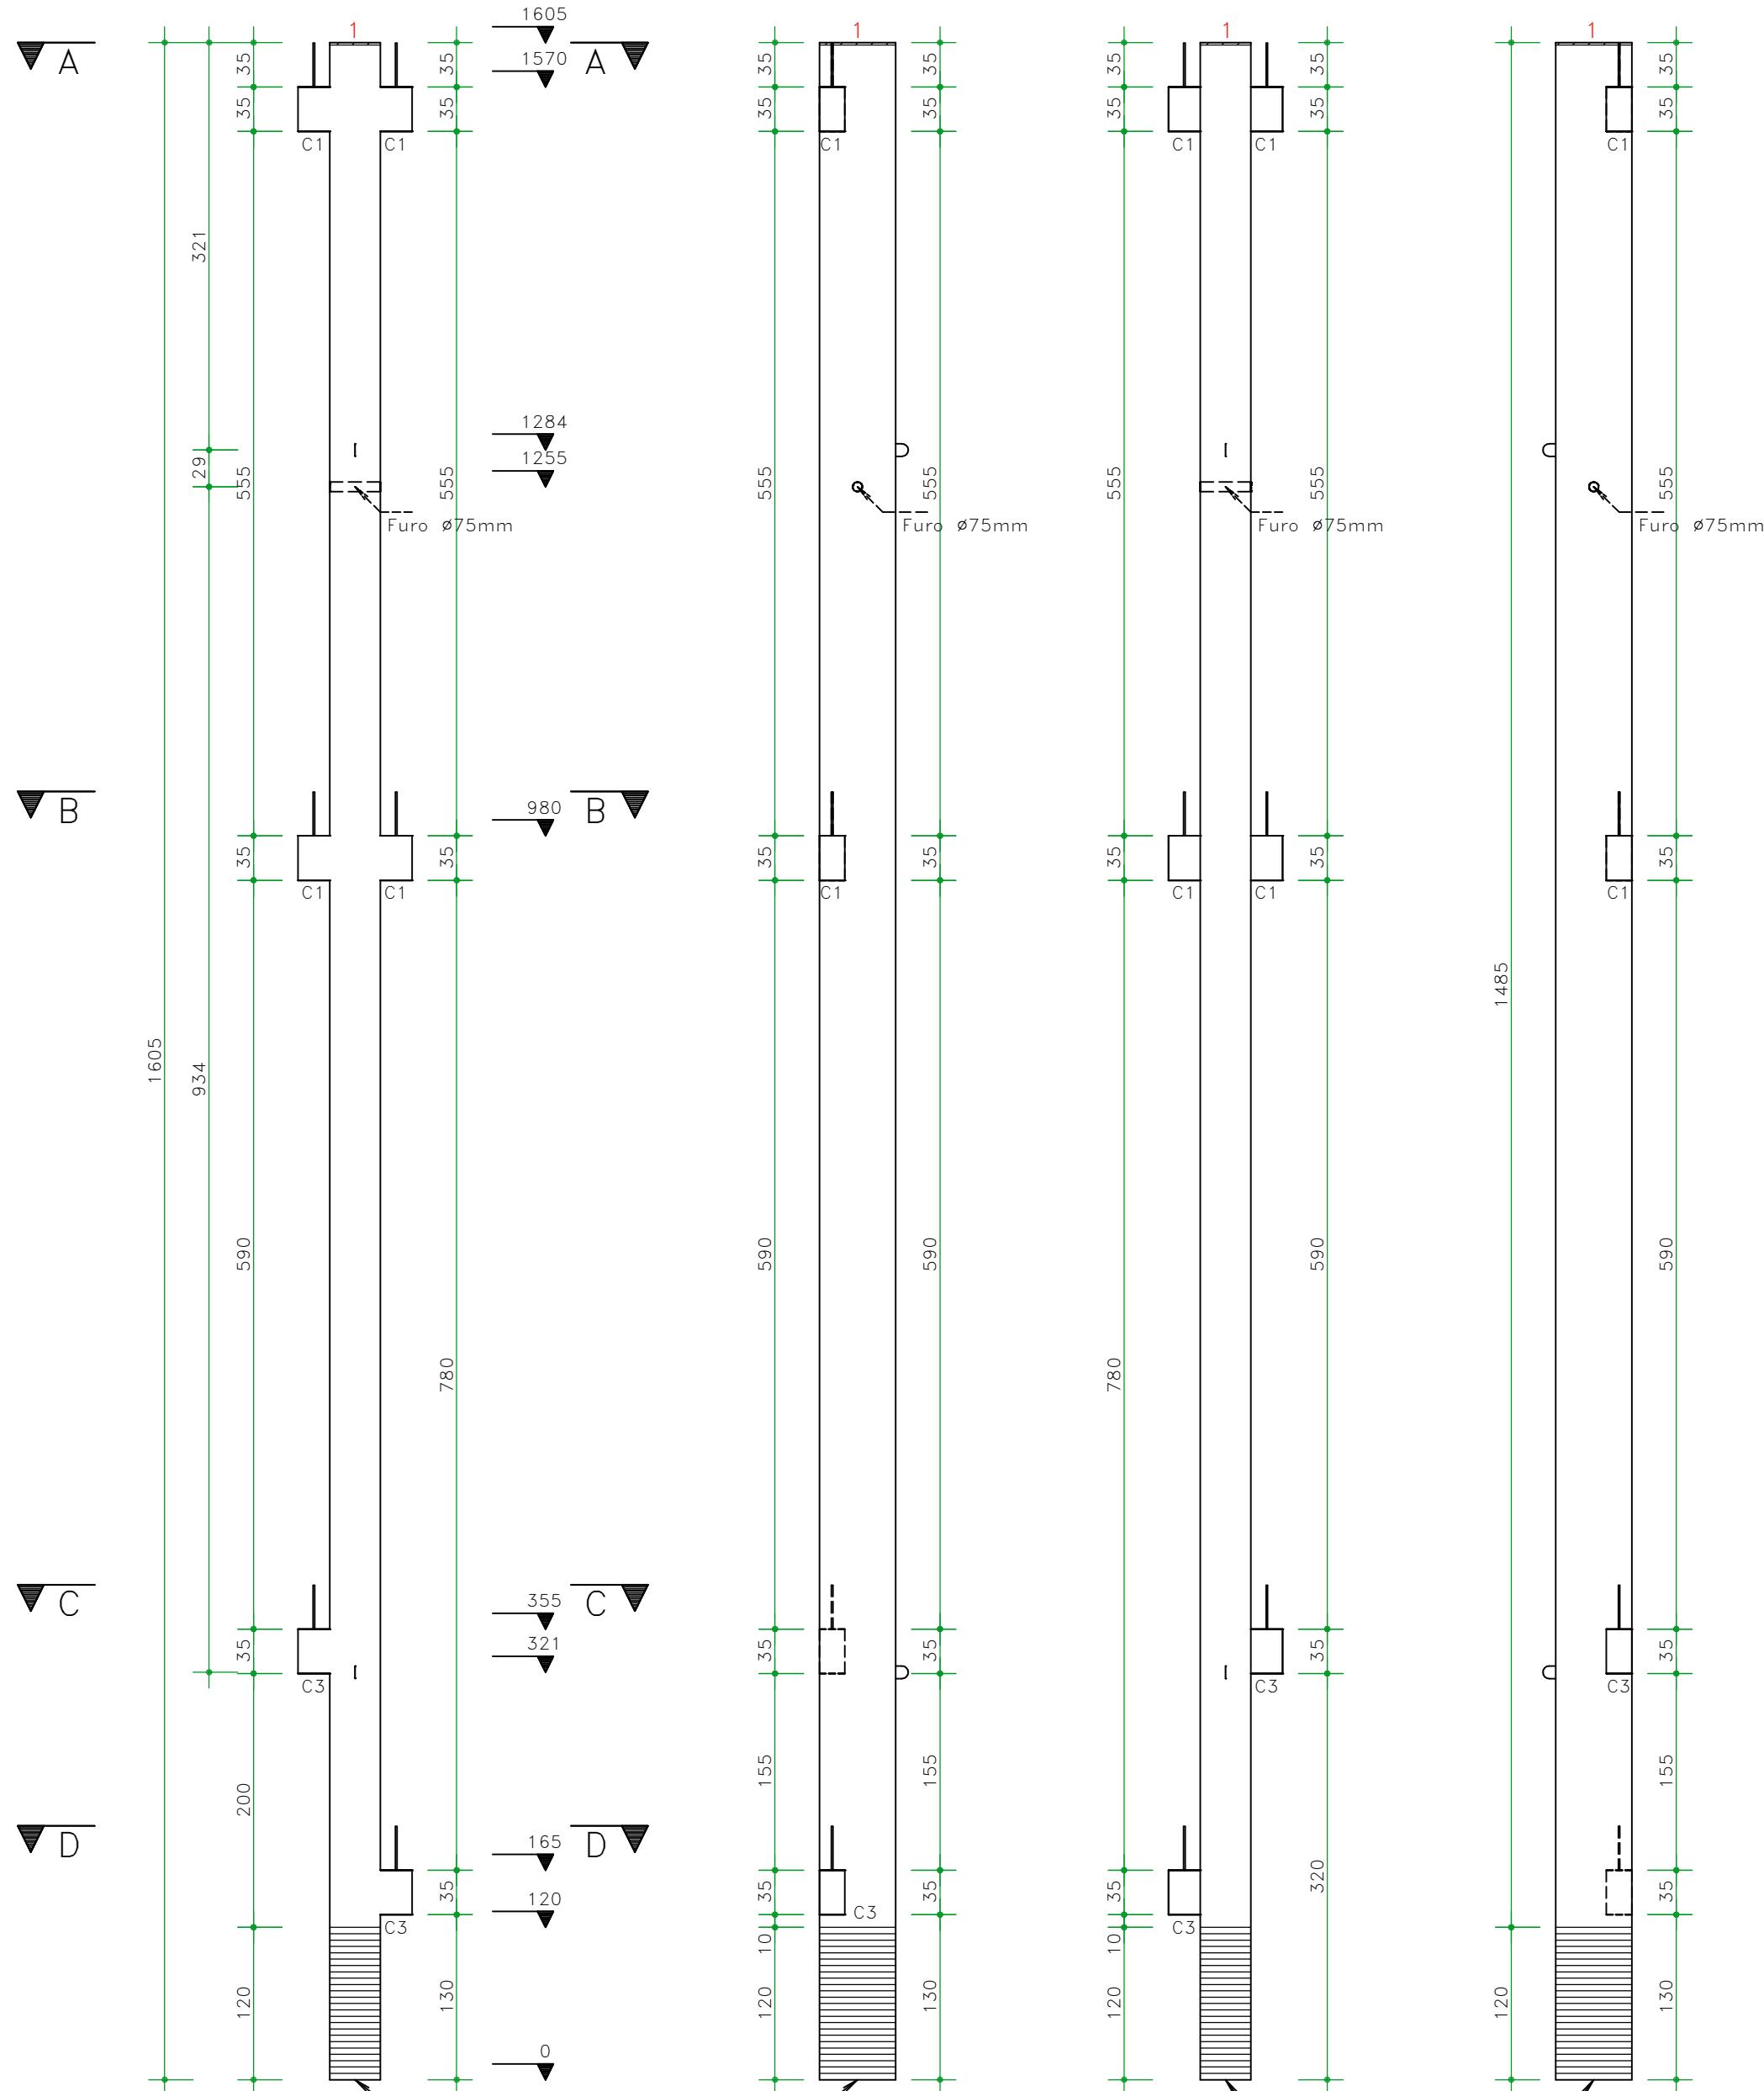
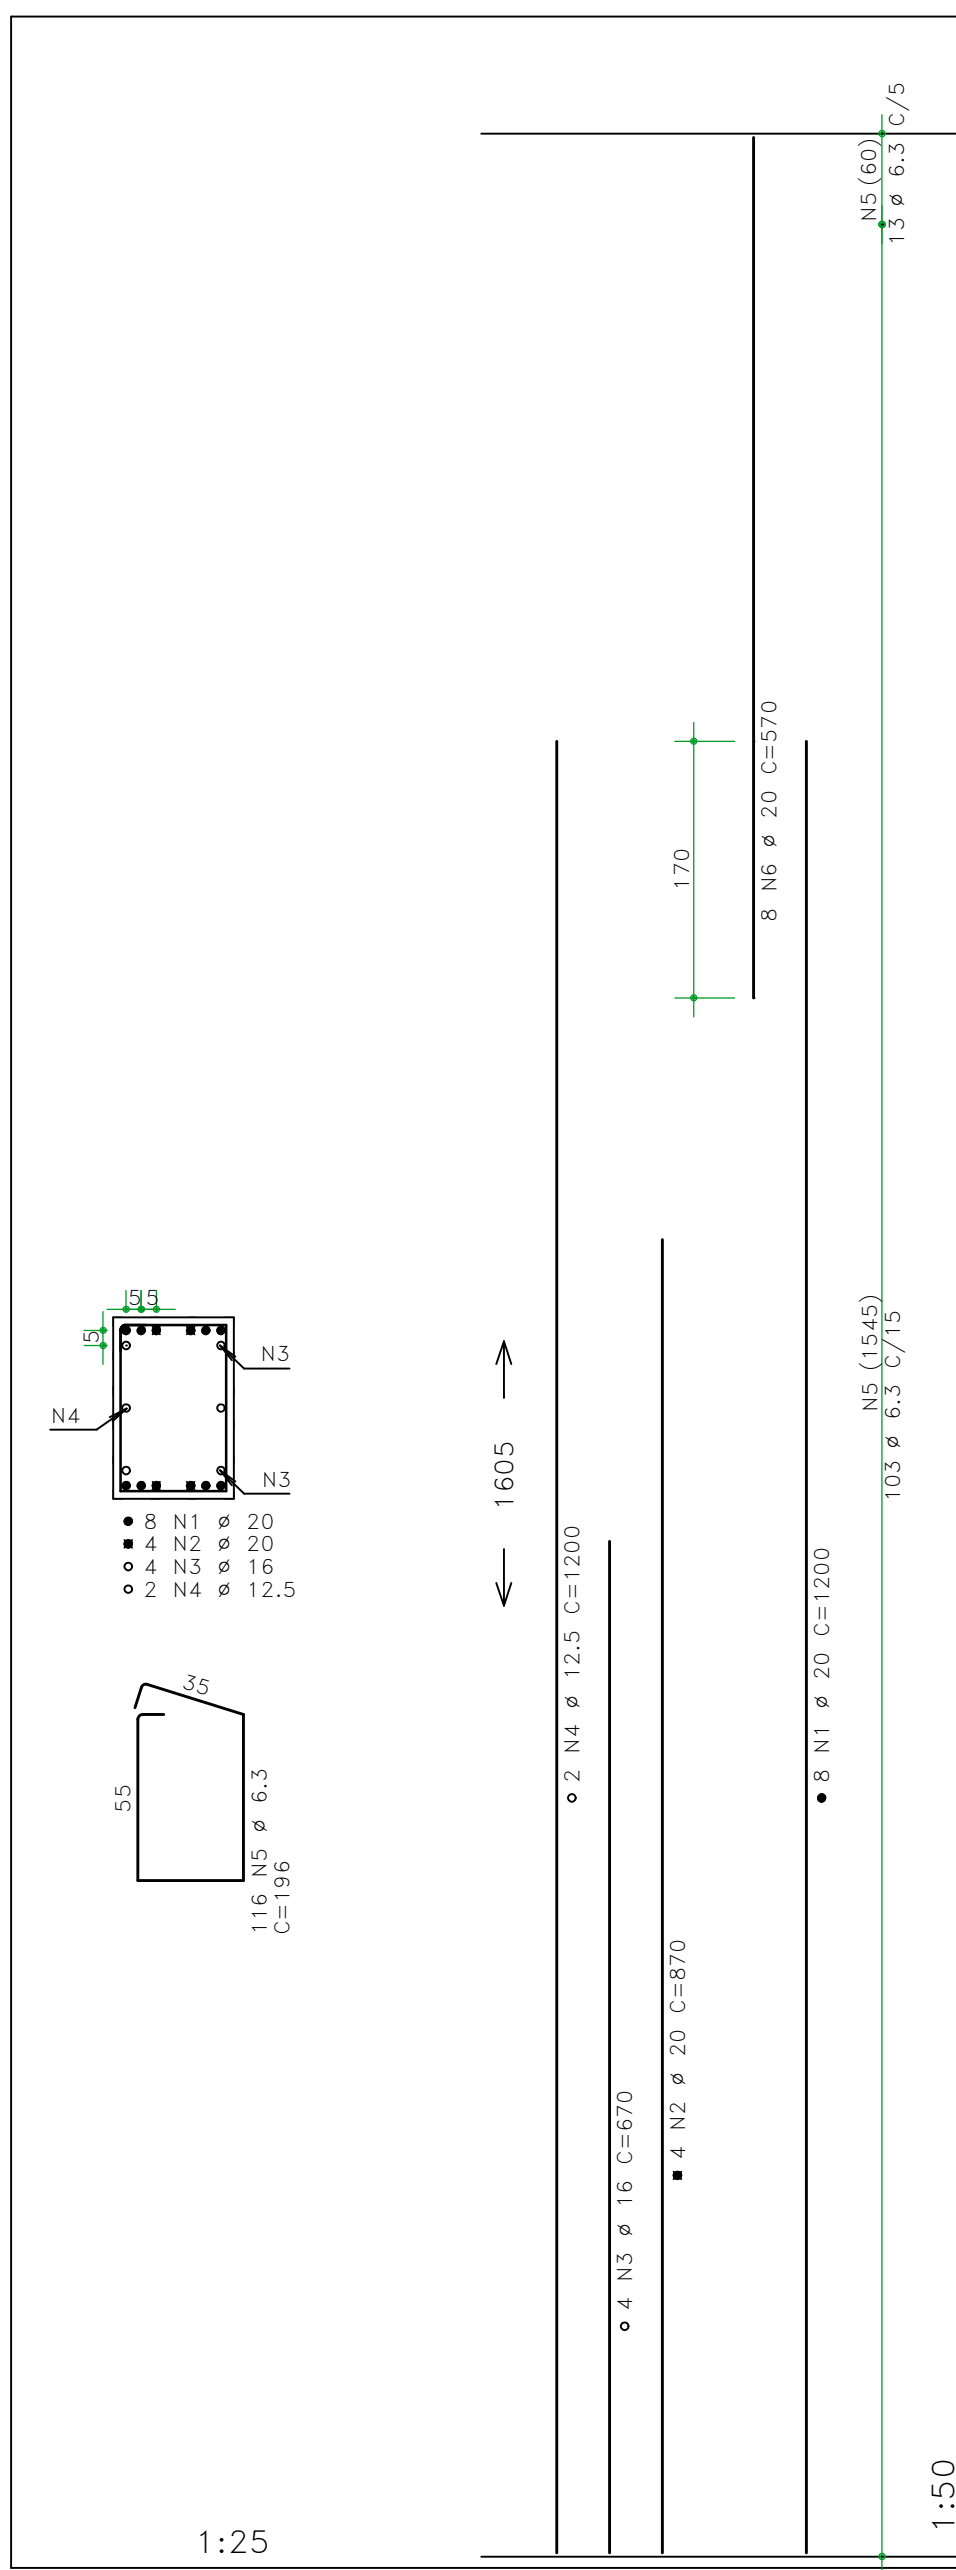
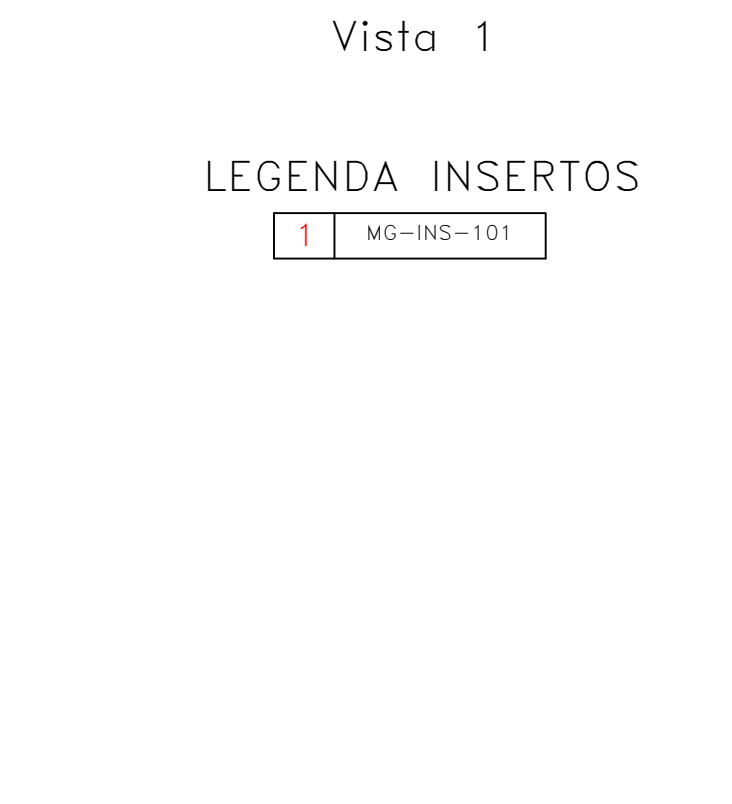


SAUT, BE 24mm, ENG. DE ESTRUTURAS S/C LTDA PL F108-CEC-PV2-P83-ROJLJ

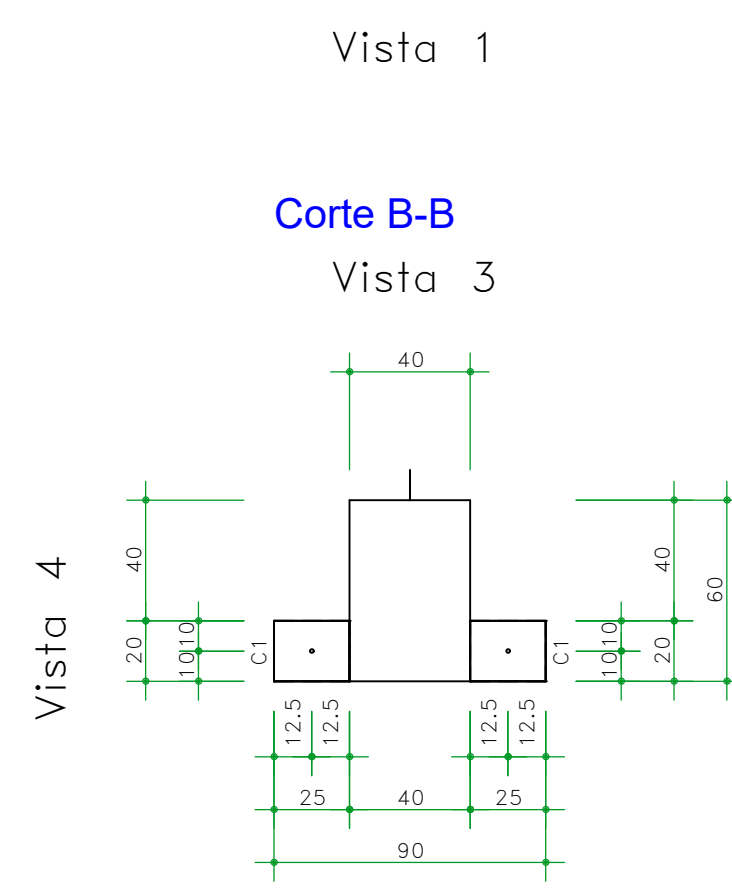

Vista 1 Vista 2 Vista 3 Vista 4

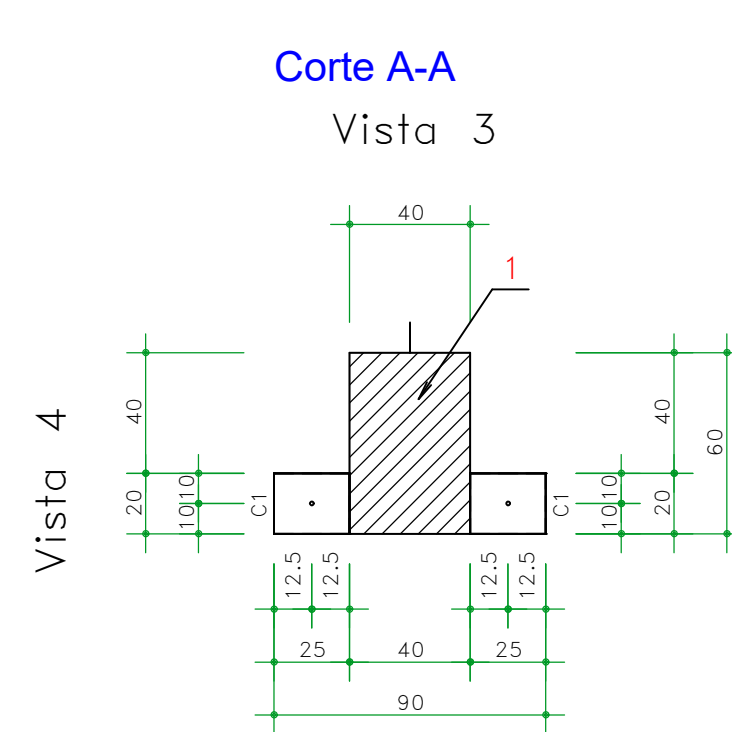

LEGENDA INSERTOS
1 MG-INS-101



CLIENTE

INBRAC

OBRA

CENTRO DE EVENTOS CUIABÁ

TÍTULO

PAVILHÃO 2 - P83
FORMA E ARMAÇÃO (1x)

OBRA N.

FOLHA N.

REVISÃO

VERIFICAÇÃO

ESCALA

1:25

DATA

24/03/2026

DESENHO

CM

REVISÃO

0

VERIFICAÇÃO

RFB



+55 (11) 98199-8507

@ruybentes.engest

/ruybentes.engest

AÇO	POS	BIT	QUANT	COMPRIMENTO	
				UNIT	TOTAL
		mm		cm	cm
50A	1	20	8	1200	9600
50A	2	20	4	870	3480
50A	3	16	4	670	2680
50A	4	12.5	2	1200	2400
50A	5	6.3	116	196	22736
50A	6	20	8	570	4560

RESUMO DE AÇO			
AÇO	BIT	COMPR	PESO
50A	6.3	227	56
50A	12.5	24	23
50A	16	27	42
50A	20	176	435
Peso Total 50A =			556 kgf

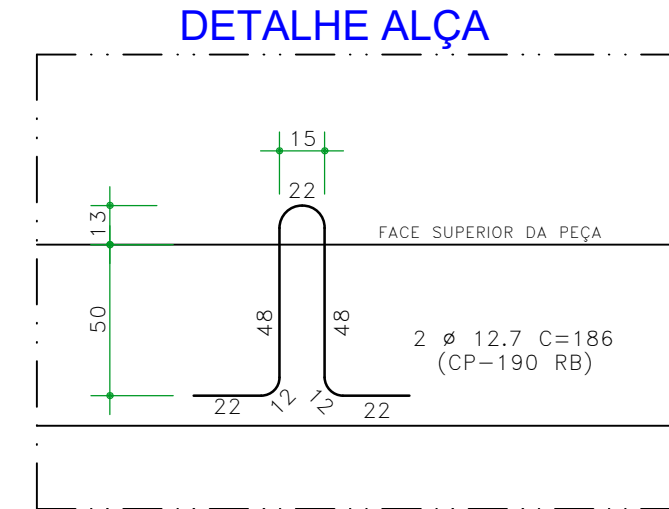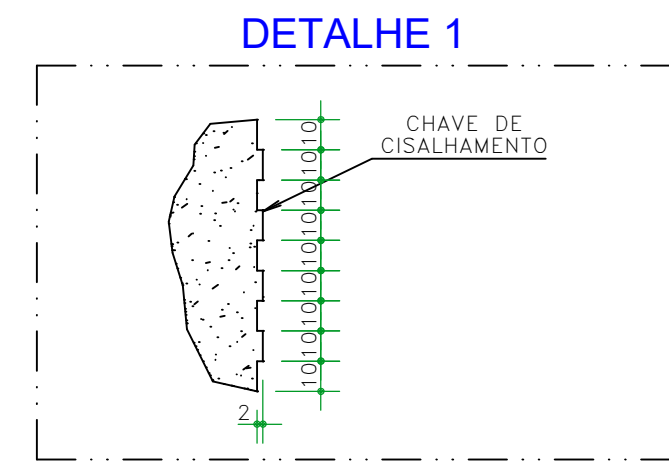

RESUMO AÇO CP 190			
AÇO	BIT	COMPR	PESO
CP-190 RB	12.7	3.72	3
Peso Total CP =			3 kg

NOTAS E OBSERVAÇÕES

- MEDIDAS EM "cm"
- CARACTERÍSTICAS DO CONCRETO (CLASSE DE AGRESSIVIDADE AMBIENTAL CAA II)
CLASSE (NBR-8953): **C 40** $E_c > 30$ GPa; Relação $a/c < 0.45$
NA DESFORMA E/OU DESPOTENSÃO: $f_{cj} = 15$ MPa e $E_c = 20$ GPa
- VOLUME / PESO DA PEÇA = **3,960** m³ / **9.890** Kg/m³
- TAXA DE AÇO NA PEÇA = **141** Kg/m³
- COBRIMENTO SOBRE A ARMAÇÃO = **2,5** cm