

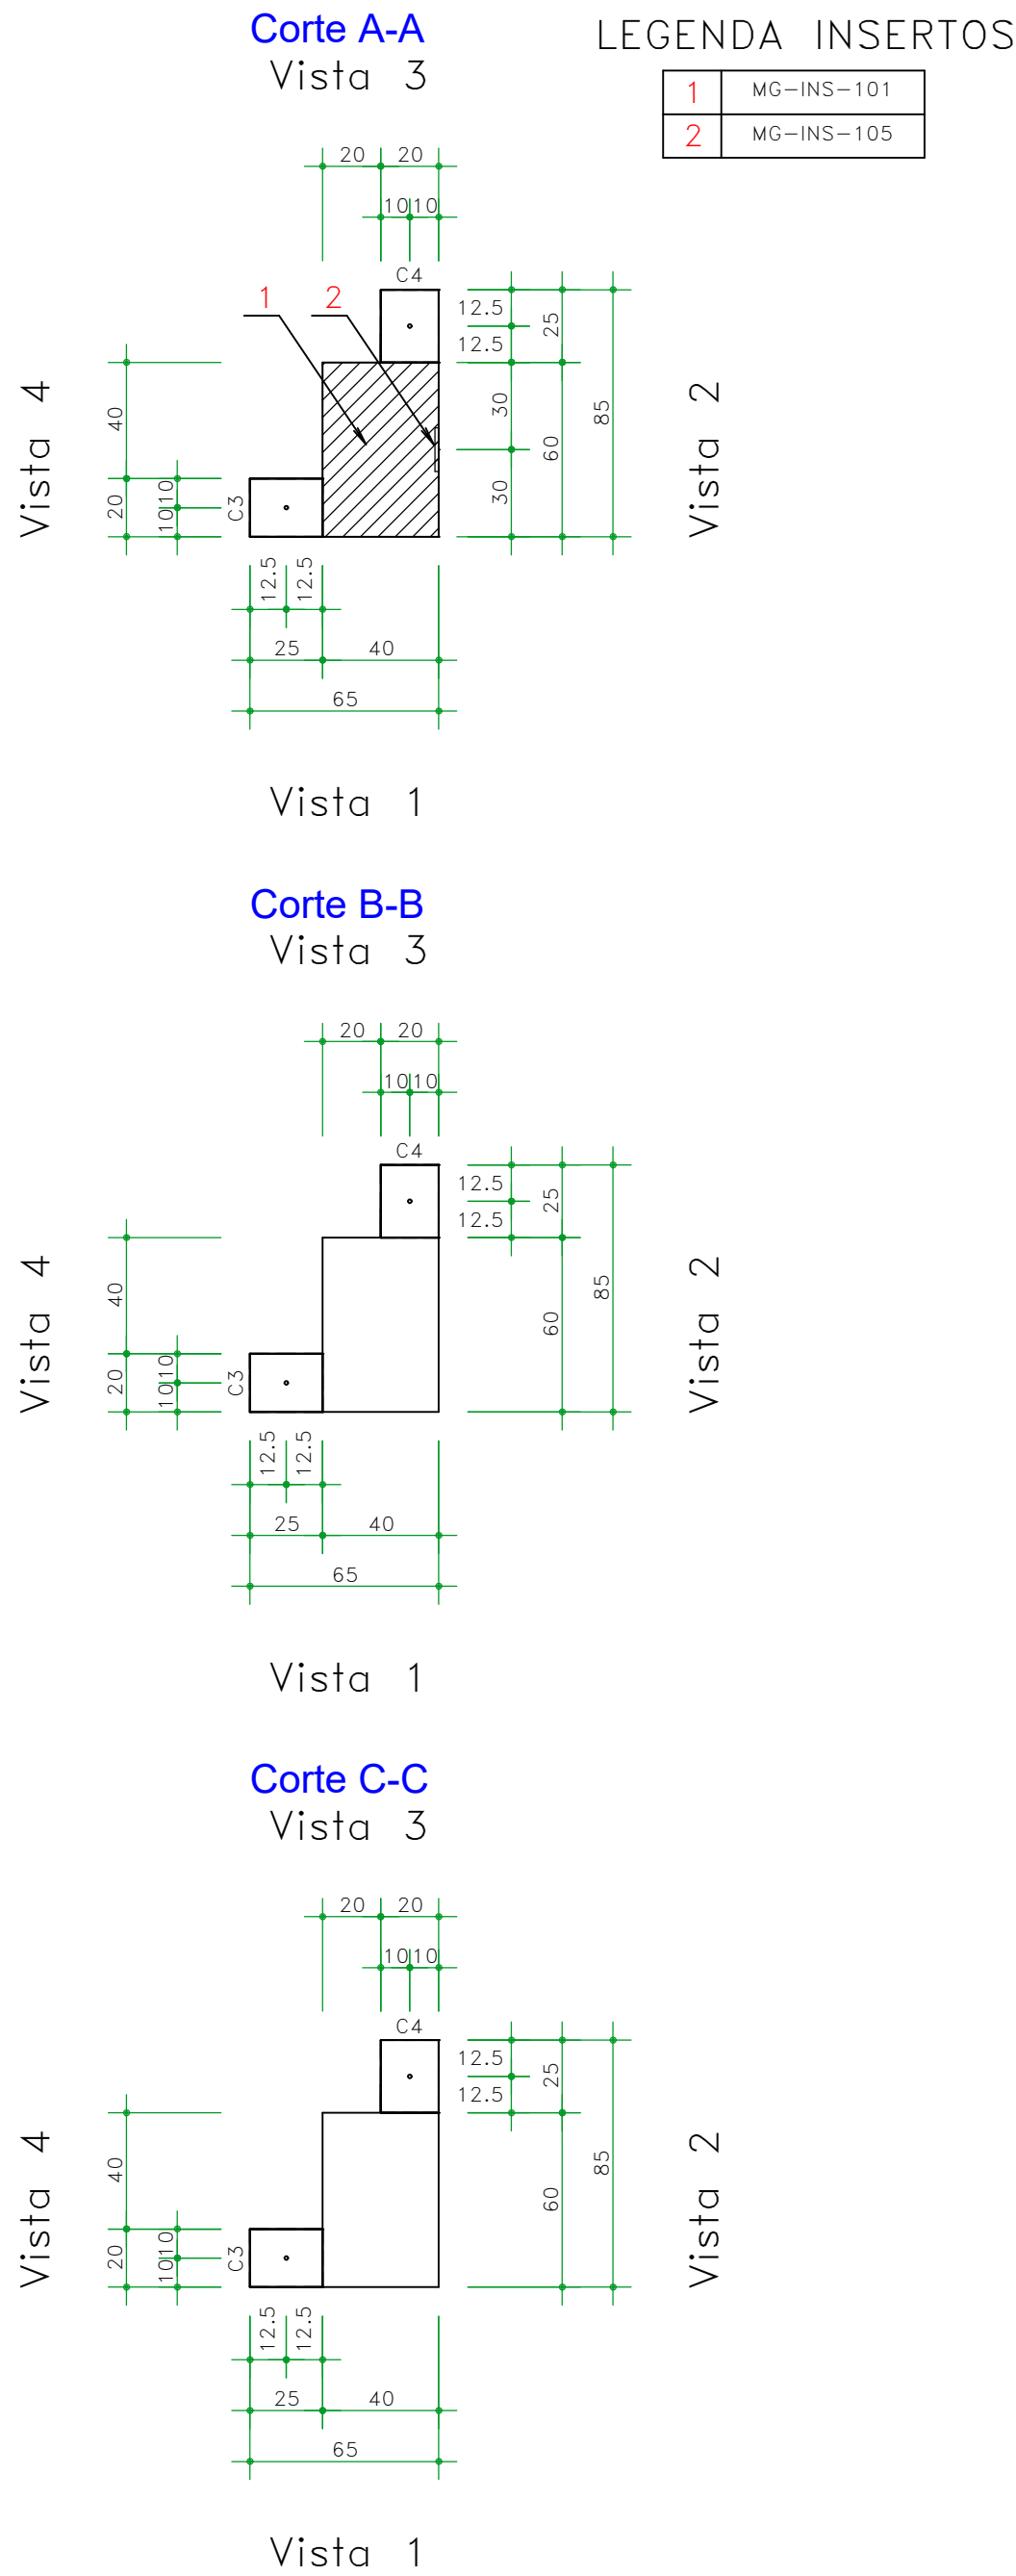
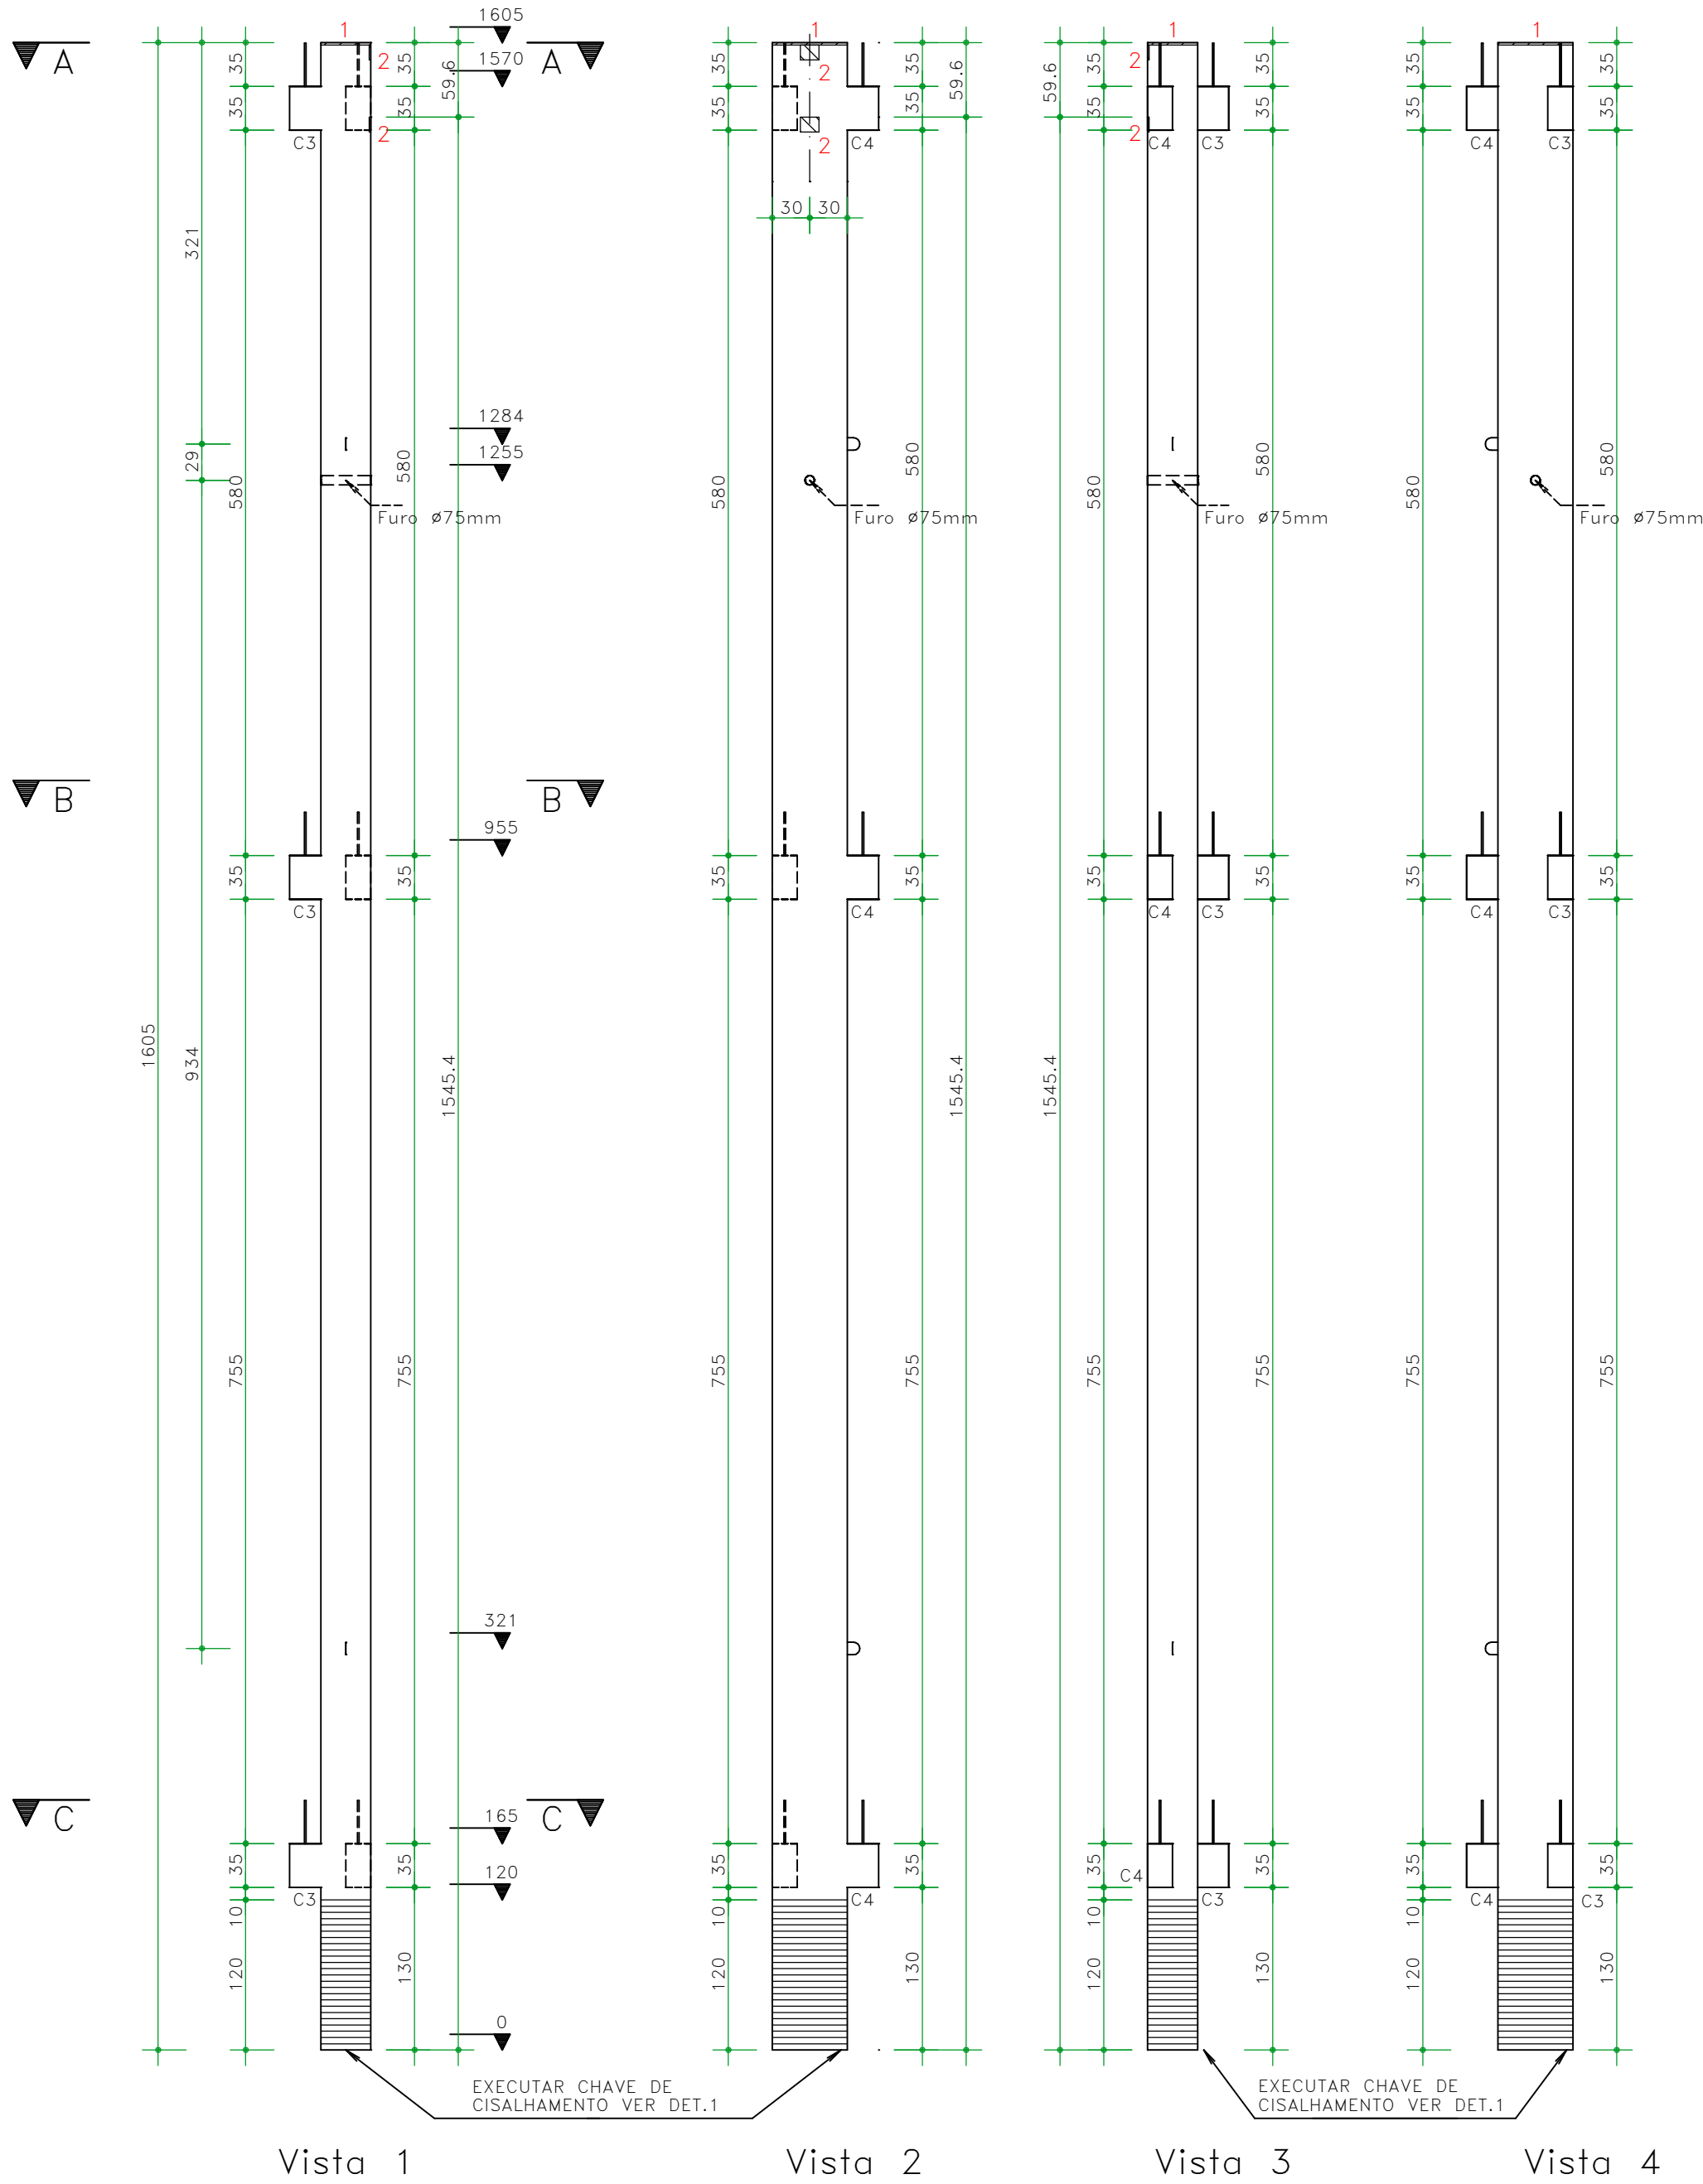
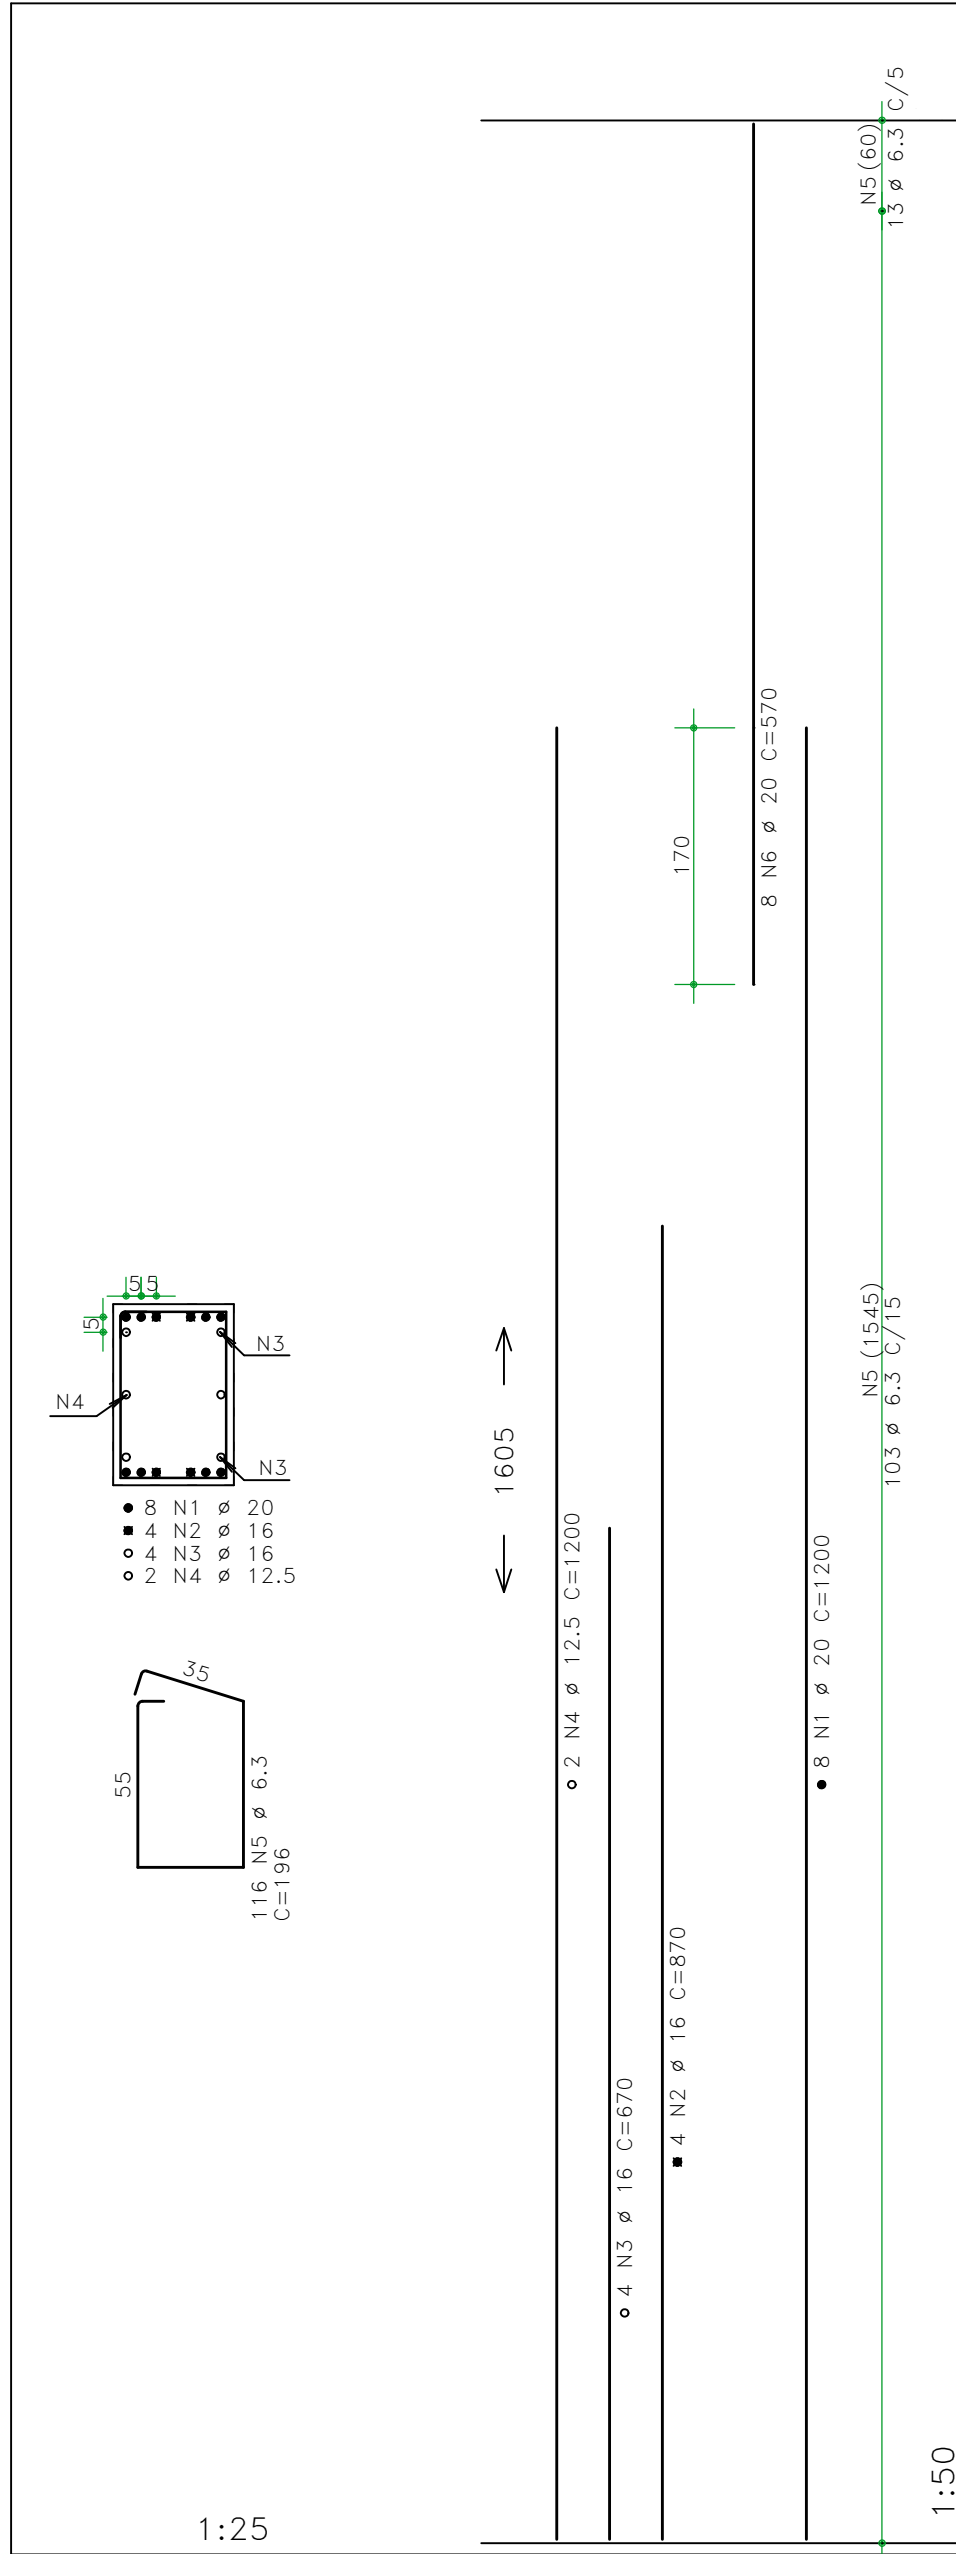


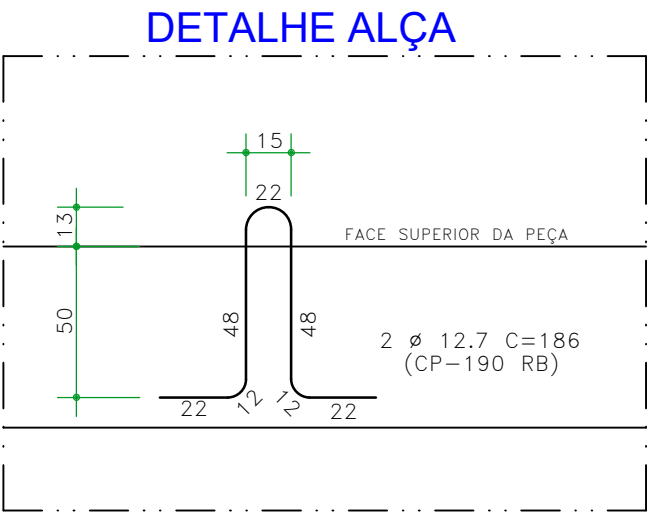

AÇO	POS	BIT mm	QUANT	COMPRIMENTO	
				UNIT cm	TOTAL cm
50A	1	20	8	1200	9600
50A	2	16	4	870	3480
50A	3	16	4	670	2680
50A	4	12.5	2	1200	2400
50A	5	6.3	116	196	22736
50A	6	20	8	570	4560

RESUMO DE AÇO			
AÇO	BIT mm	COMPR m	PESO kgf
50A	6.3	227	56
50A	12.5	24	23
50A	16	62	97
50A	20	142	349
Peso Total		50A =	525 kgf

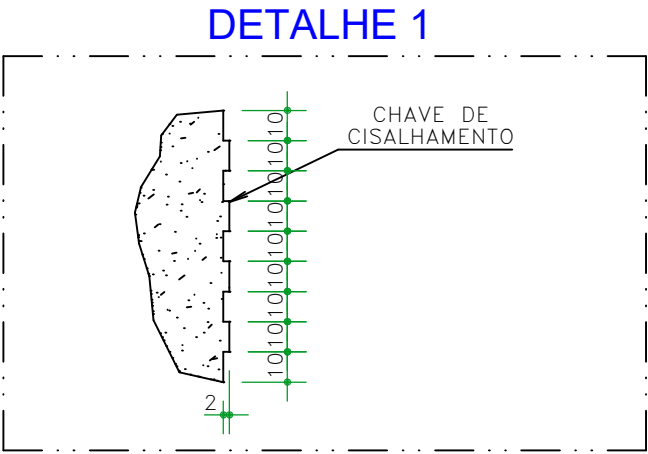

RESUMO AÇO CP 190			
AÇO	BIT mm	COMPR m	PESO kgf
CP-190 RB	12.7	3.72	3
Peso Total		CP =	3 kg

NOTAS E OBSERVAÇÕES

- MEDIDAS EM "cm"
- CARACTERÍSTICAS DO CONCRETO (CLASSE DE AGRESSIVIDADE AMBIENTAL CAA II)
CLASSE (NBR-8953): **C 40** $E_c > 30$ GPa; Relação $a/c < 0.45$
NA DESFORMA E/OU DESPOTENSÃO: $f_{cj} = 15$ MPa e $E_c = 20$ GPa
- VOLUME / PESO DA PEÇA = **3,960** m³ / **9.890** Kg/m³
- TAXA DE AÇO NA PEÇA = **133** Kg/m³
- COBRIMENTO SOBRE A ARMAÇÃO = **2,5** cm



	CLIENTE	INBRAC		ESCALA	1:25	
	OBRA	CENTRO DE EVENTOS CUIABÁ		DATA	25/03/2026	
				DESENHO	CM	
		OBRA N.	25/016	FOLHA N.	0	
				VERIFICAÇÃO	RFB	
TÍTULO		PAVILHÃO 2 - P86 FORMA E ARMAÇÃO (1x)		F112		
 +55 (11) 98199-8507		 @ruybentes.engest		 /ruybentes.engest		