




ELEVAÇÃO

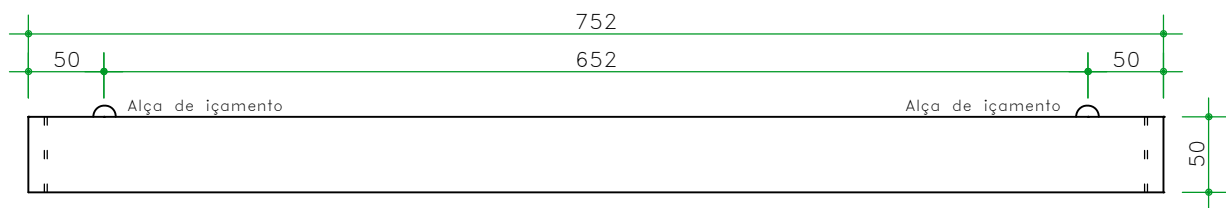


SEÇÃO

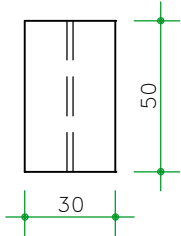


FUROS INICIAIS
(20 mm)

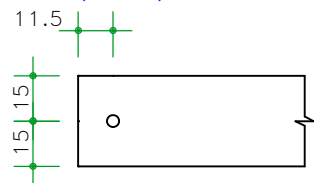


FUROS FINAIS
(20 mm)

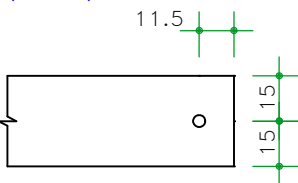













PLANTA

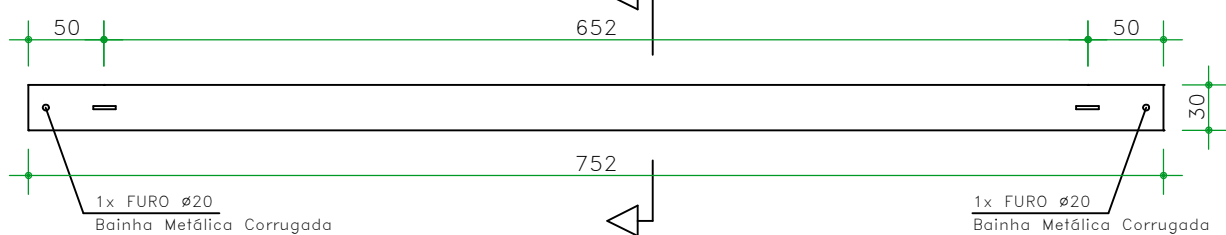


DETALHE INICIAL

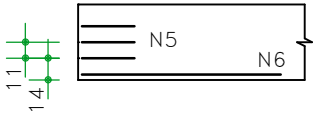


DETALHE FINAL

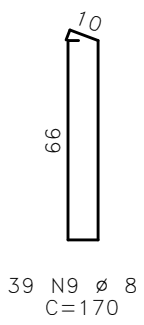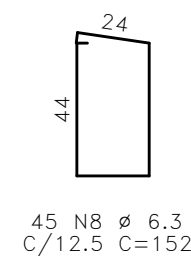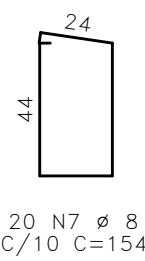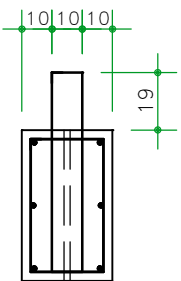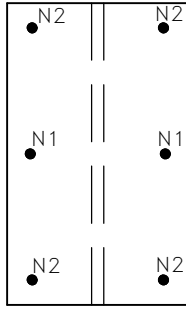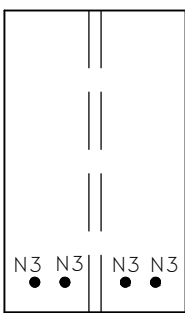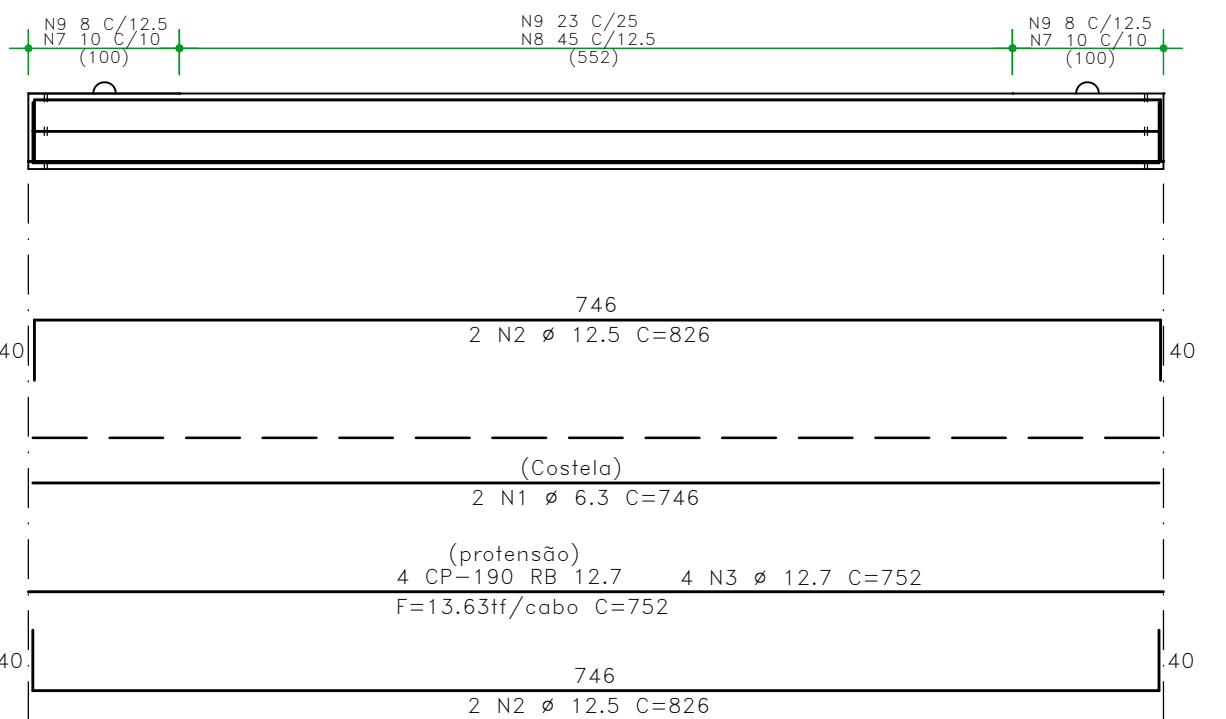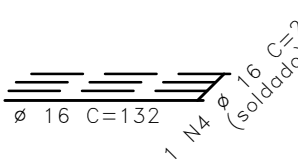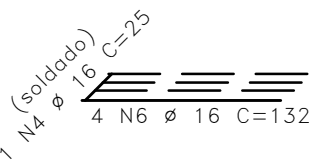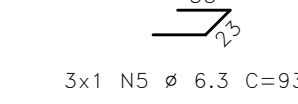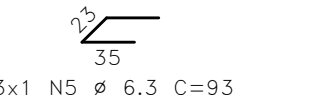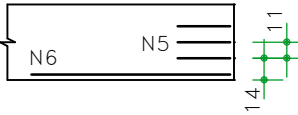

CABOS INF.

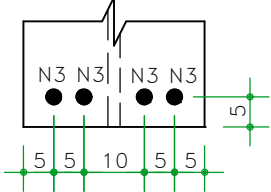

DETALHE ALÇA (2x)

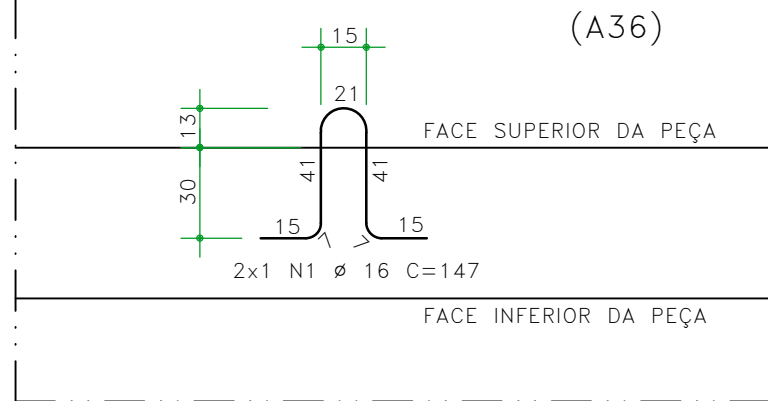


AÇO	POS	BIT	QUANT	COMPRIMENTO	
				UNIT	TOTAL
		mm		cm	cm
A36	1	16	2	147	294

RESUMO DE AÇO			
AÇO	BIT	COMPR	PESO
A36	16	3	5
Peso Total	A36	=	5 kgf

DET. SOLDA

Sem esc.

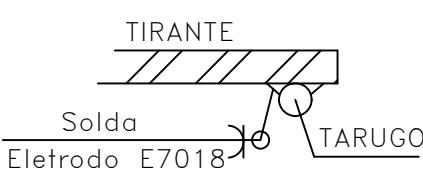

NOTAS E OBSERVAÇÕES

- 1 - MEDIDAS EM "cm"
- 2 - CARACTERÍSTICAS DO CONCRETO (CLASSE DE AGRESSIVIDADE AMBIENTAL CAA II)
CLASSE (NBR-8953): **C 40** $E_c > 30$ GPa; Relação a/c **< 0.45**
NA DESFORMA E/OU DESPROTENSÃO: $f_{cj} = 20$ MPa e $E_c = 22$ GPa
- 3 - VOLUME / PESO DA PEÇA = **1,128** m³ / **2.820** Kg
- 4 - TAXA DE AÇO NA PEÇA = **89** Kg/m³ (CA-50/60); **21** Kg/m³ (CP190-RB)
- 5 - COBRIMENTO SOBRE A ARMAÇÃO = **3,0** cm



TÍTULO
VIGA - V235
FORMA E ARMAÇÃO (1x)

CLIENTE INBRAC	ESCALA 1:50
OBRA ESCOLA ADVENTISTA	DATA 29/05/2026
OBRA N. 25/009	FOLHA N. 0
REVISÃO RFB	VERIFICAÇÃO RFB